


ANTAL	MONTAGEDEL
1	B/17

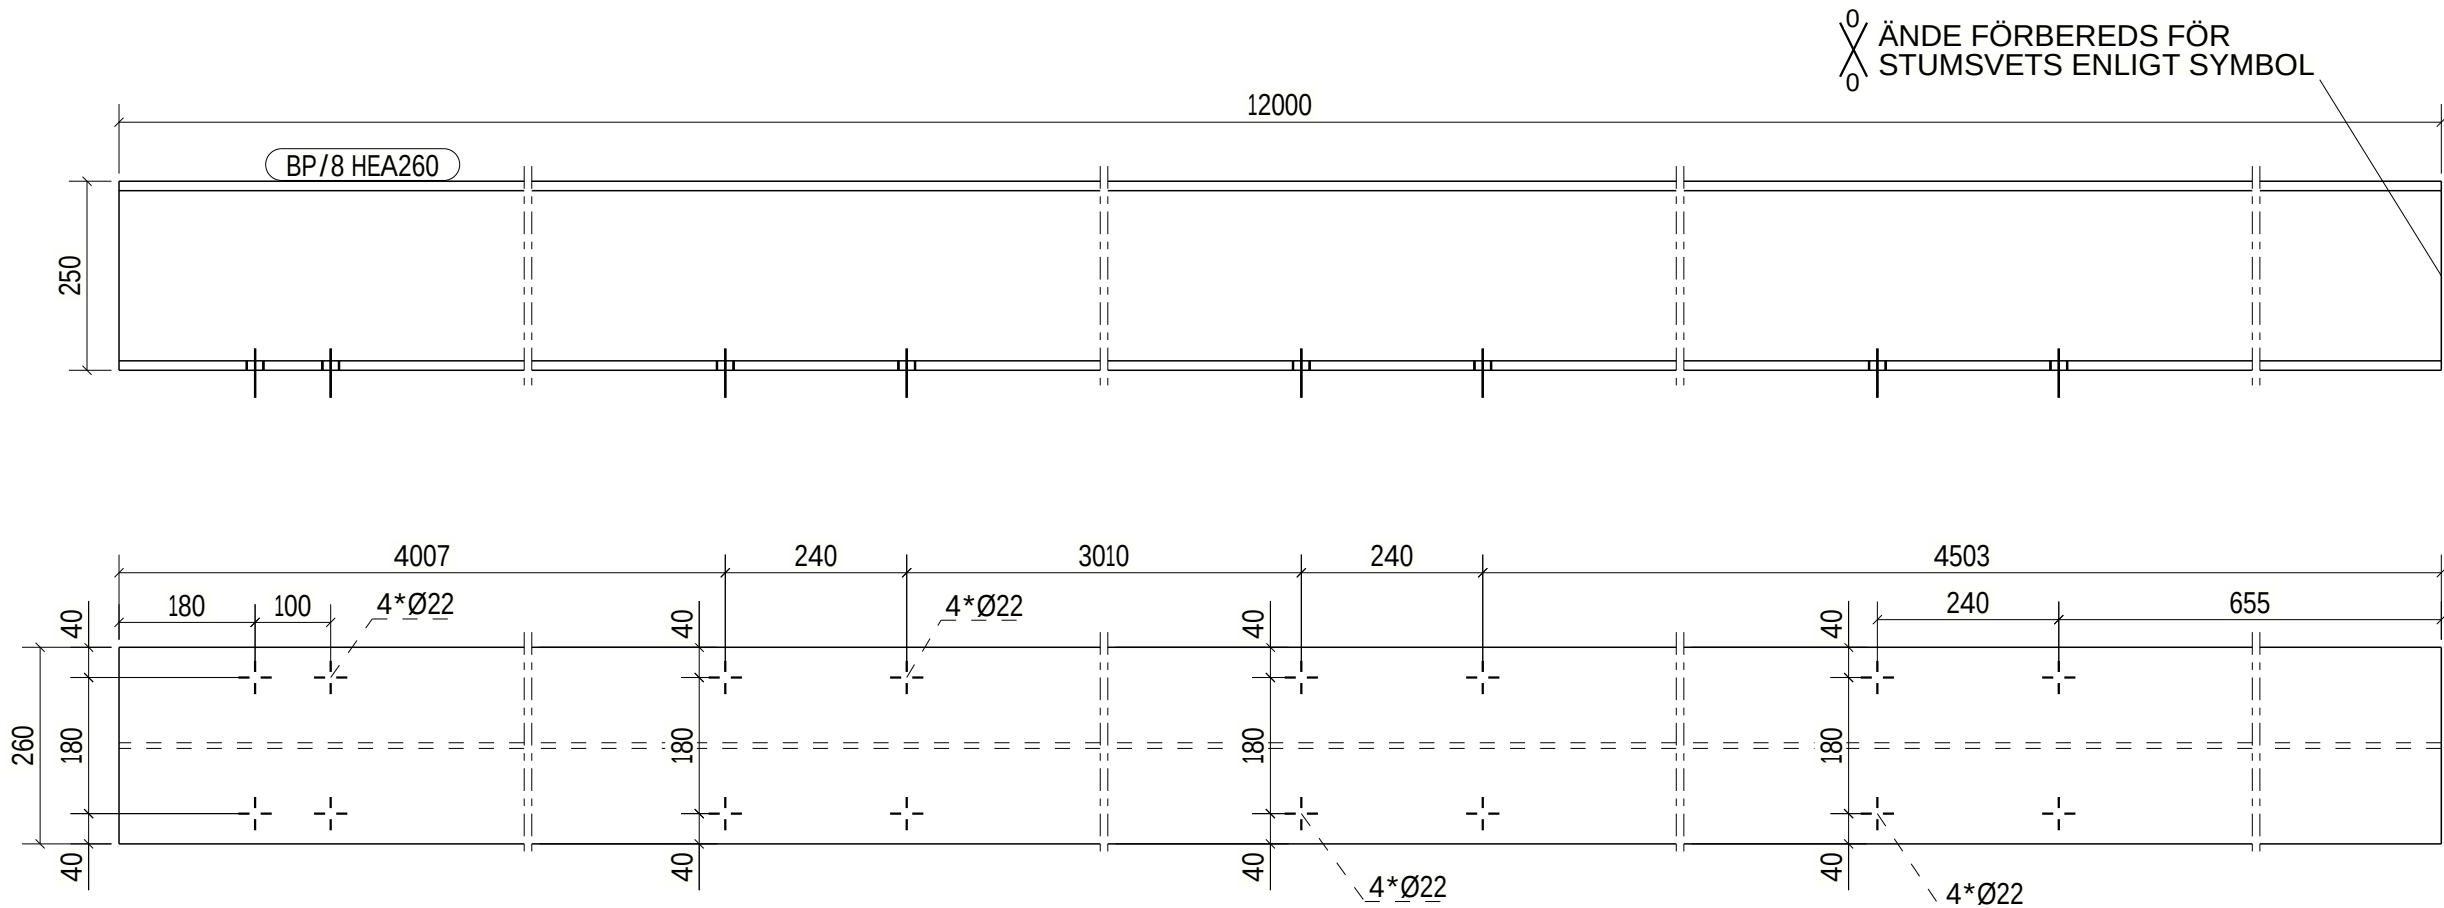

BP/8	HEA260	S355J2	1	12000.0	17.81	817.8
MÄRKE	PROFIL	MATERIAL	ANTAL	LÄNGD	AREA	VIKT
MATERIALLISTA				TOTALT	17.81	817.8

Norconsult 		ANSVARIG PART	PROJEKT		FÖRFRÅGNINGSUNDERLAG				STATUS	
BJÖRN LIDSTRÖM			CENTRAALKÖK ROBERTSFORS KOMMUN		BYGGHANDLING					HANDLING
			TILLVERKNINGSRITNINGAR STÅL		RITNINGSKATEGORI				ÄNDRING	FORMAT
					INNEHÅLL				DATUM	SKALA
			BJÖRN LIDSTRÖM		GODKÄND AV			2024-12-20	1:10	NUMMER
ARVID WENNERBERG		SKAPAD AV	PARTS		BP/8					