


ANTAL	MONTAGEDEL
1	B/18

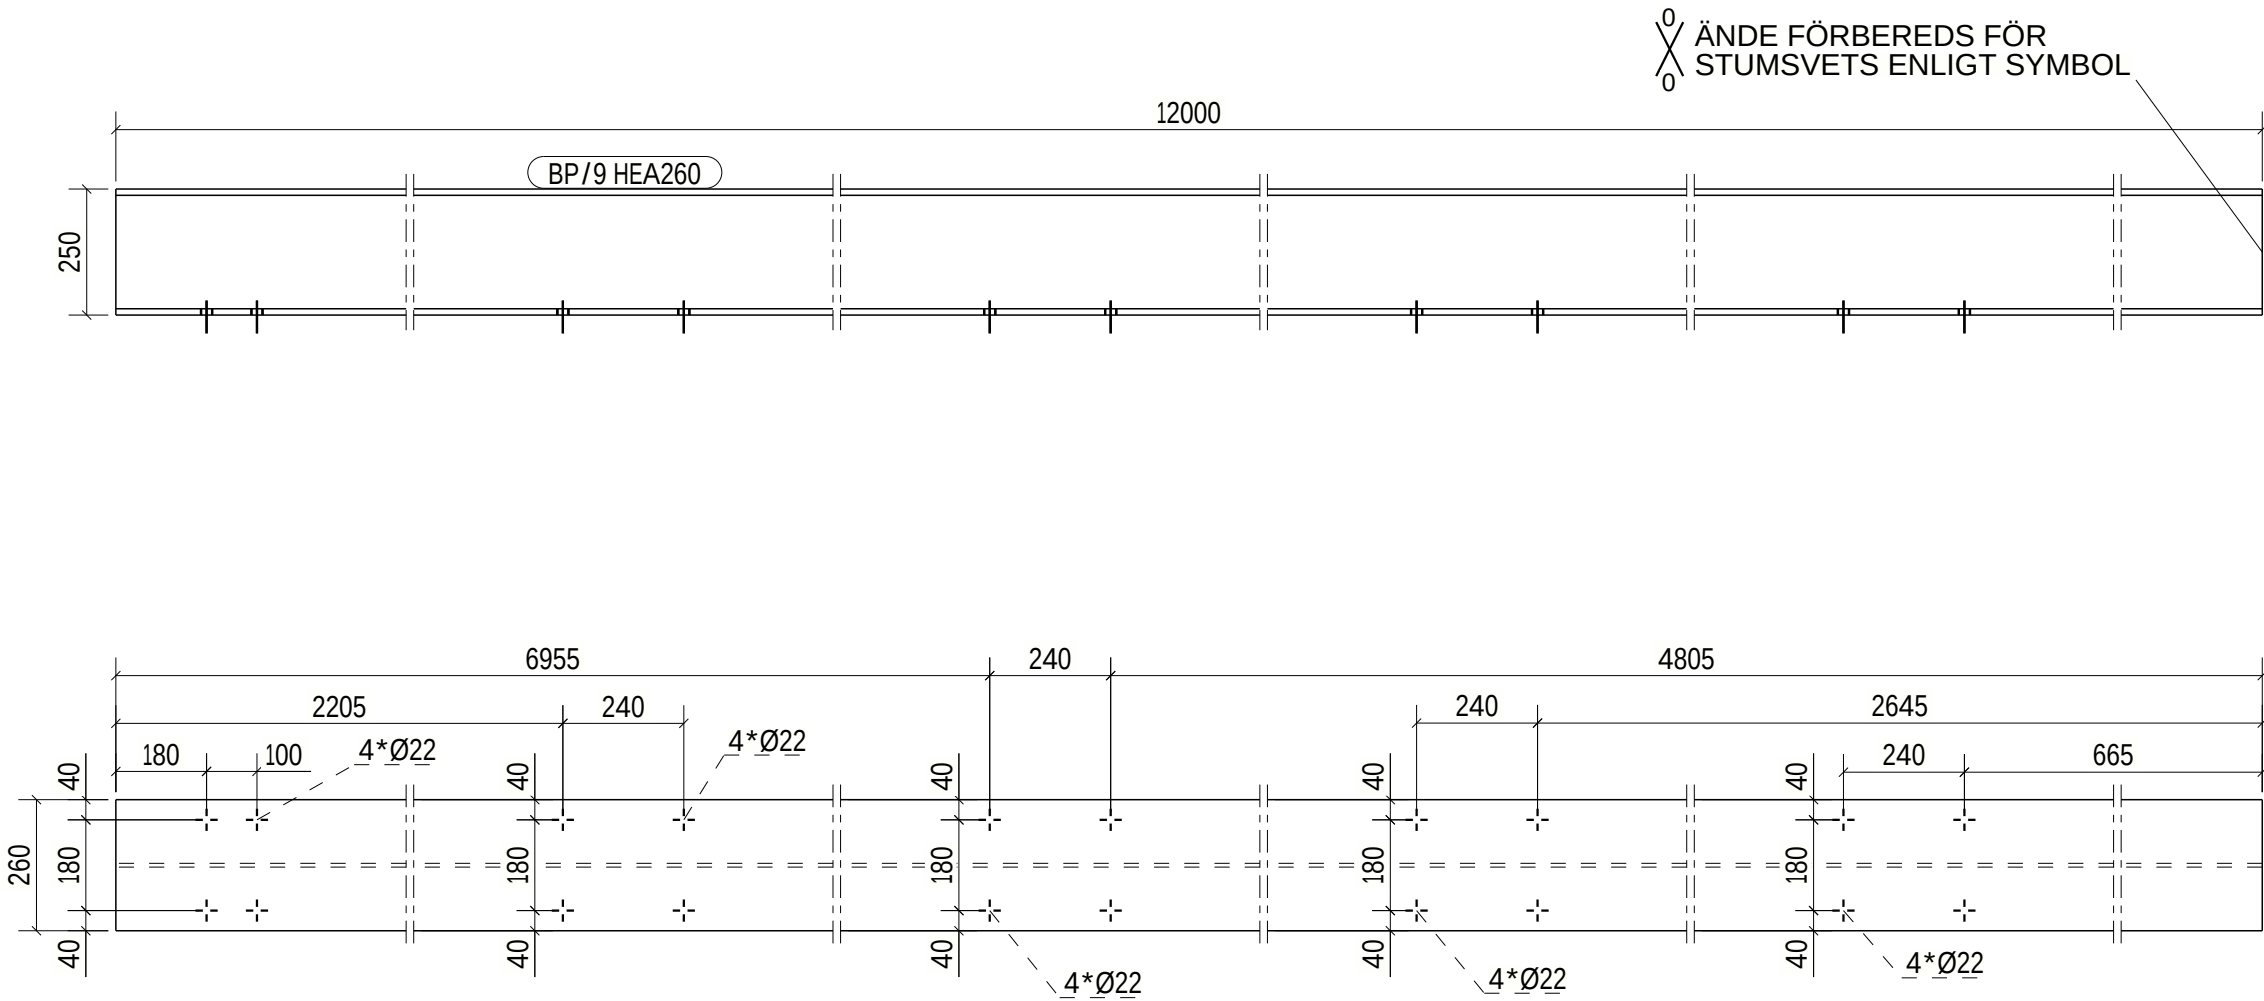

BP/9	HEA260	S355J2	1	12000.0	17.81	817.8
MÄRKE	PROFIL	MATERIAL	ANTAL	LÄNGD	AREA	VIKT
MATERIALLISTA				TOTALT	17.81	817.8

Norconsult		ANSVARIG PART	CENTRALEKÖ ROBERTSFORS KOMMUN		PROJEKT	FÖRFRÅGNINGSUNDERLAG		STATUS
BJÖRN LIDSTRÖM		KONTAKTPERSON	TILLVERKNINGSRITNINGAR STÅL		RITNINGSKATEGORI	BYGGHANDLING		HANDLING
BJÖRN LIDSTRÖM		GODKÄND AV				ÄNDRING	FORMAT	A3
ARVID WENNERBERG		SKAPAD AV	PARTS		INNEHÅLL	2024-12-20	DATUM	SKALA
						BP/9	NUMMER	BET