
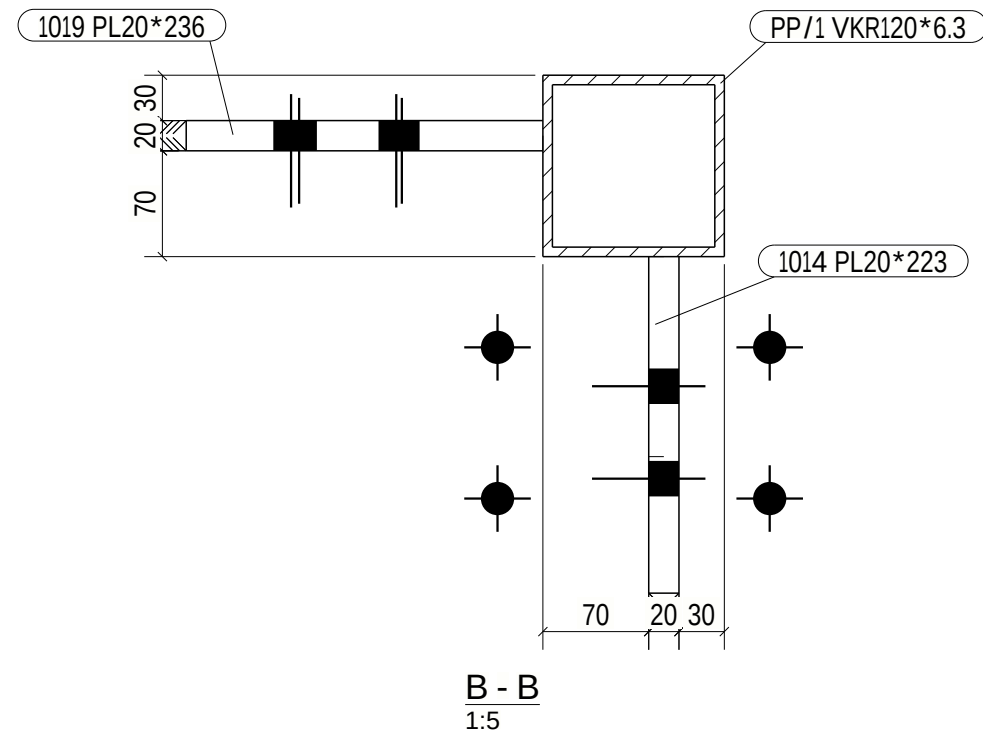
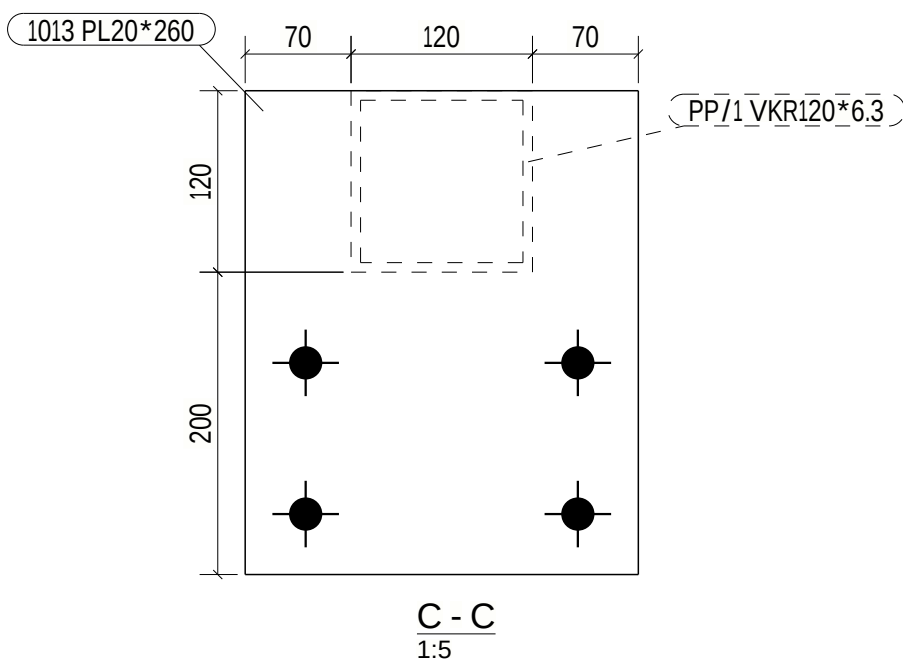
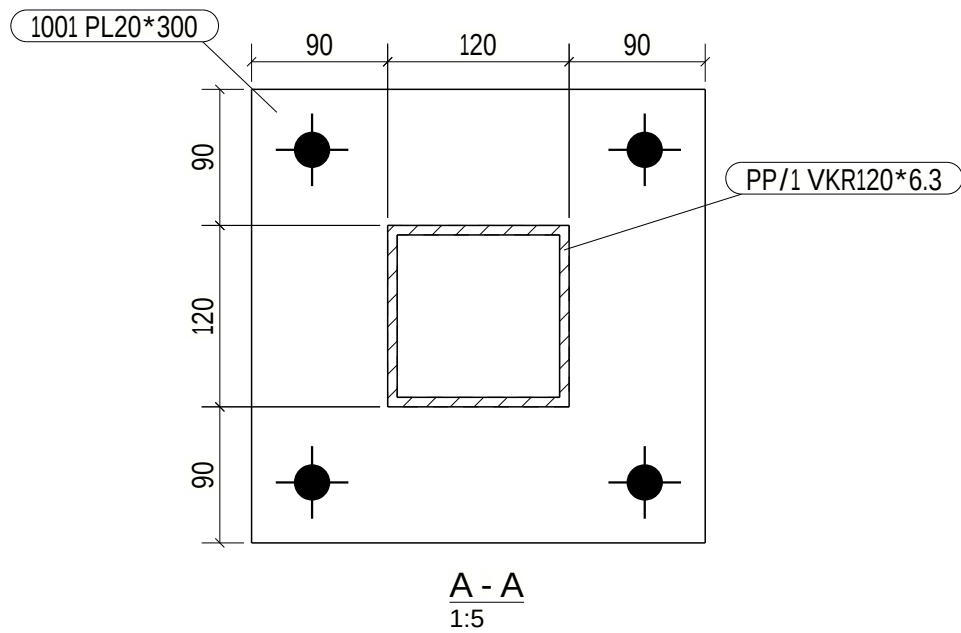


PLACERING I STOMNÄT	
NUMMER	SYSTEMLINJE
P/1	3/A

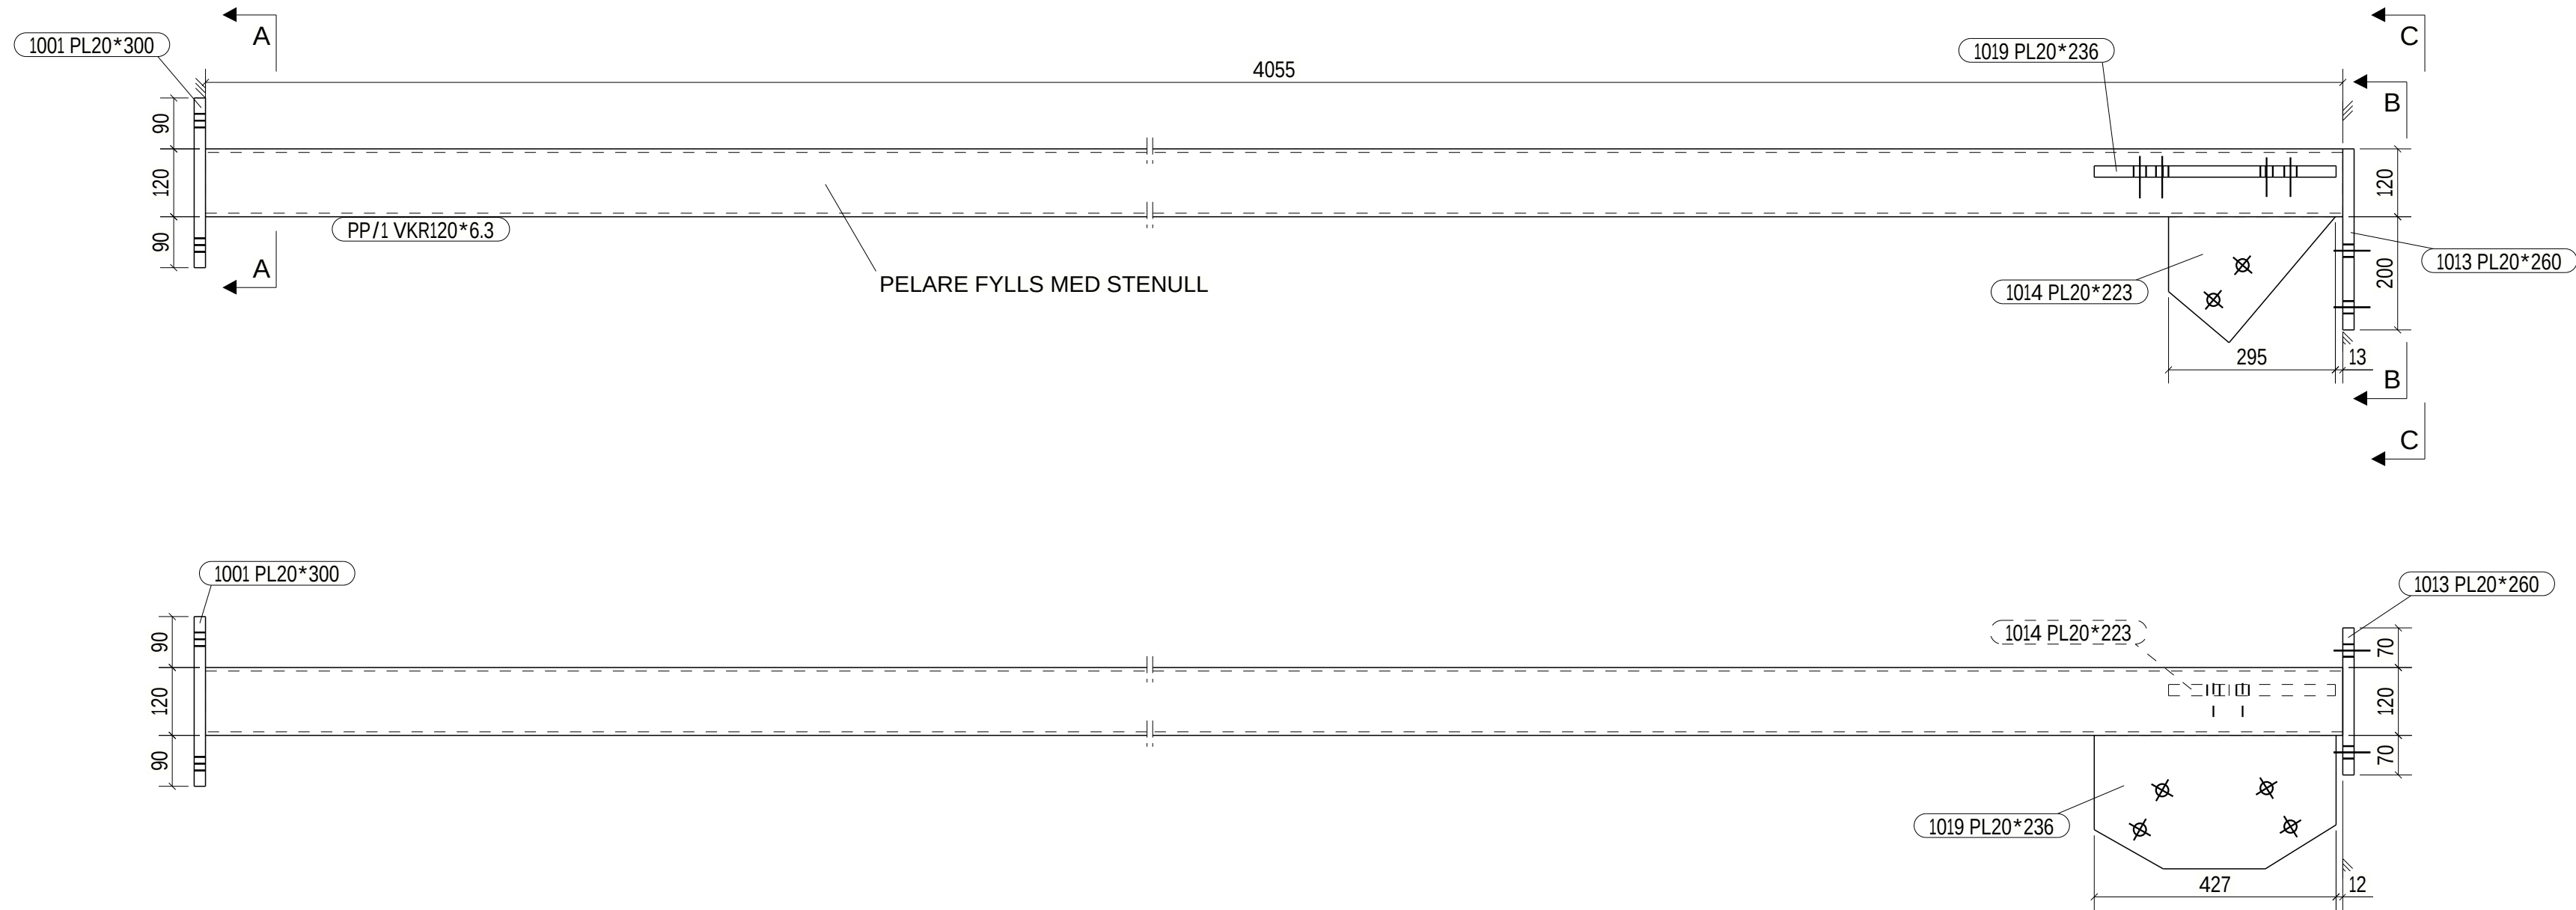

ALLMÄNNA NOTERINGAR:

ALLA HÅL ÄR 22mm OM EJ ANNAT ANGES
ALLA SVETSAR ÄR 6.5mm OM EJ ANNAT ANGES

MATERIALLISTA FÖR ETT GODS MÄRKT:		P/1	1 st. TILLVERKAS			
STYCKLIT.	PROFIL	MATERIAL	ANT.	LÅNGD	AREA/st	VIKT/st
PP/1	VKR120*6.3	S355J2H	1	4055	1.9	89.8
1019	PL20*236	S355J2	1	427	0.2	14.4
1001	PL20*300	S355J2	1	300	0.2	14.1
1013	PL20*260	S355J2	1	320	0.2	13.1
1014	PL20*223	S355J2	1	295	0.1	6.3
TOTALT					2.6	137.6

Norconsult	ANSVARS PART	PROJEKT	FÖRFRÅGNINGSUNDERLAG		STATUS
	KONTAKTPERSON	CENTRALEKÖB ROBERTSFORS KOMMUN	BYGGHANDLING		HANDLING
	GODKÄND AV	TILLVERKNINGSRITNINGAR STÅL	ANDRING		FORMAT
	SKAPAD AV	INNEHÅLL	2024-12-20		SKALA
PARTS			P/1		BET