


PLACERING I STOMNÄT	
NUMMER	SYSTEMLINJE
P/11	3/A-B
P/11	3/B
P/11	5/A-B

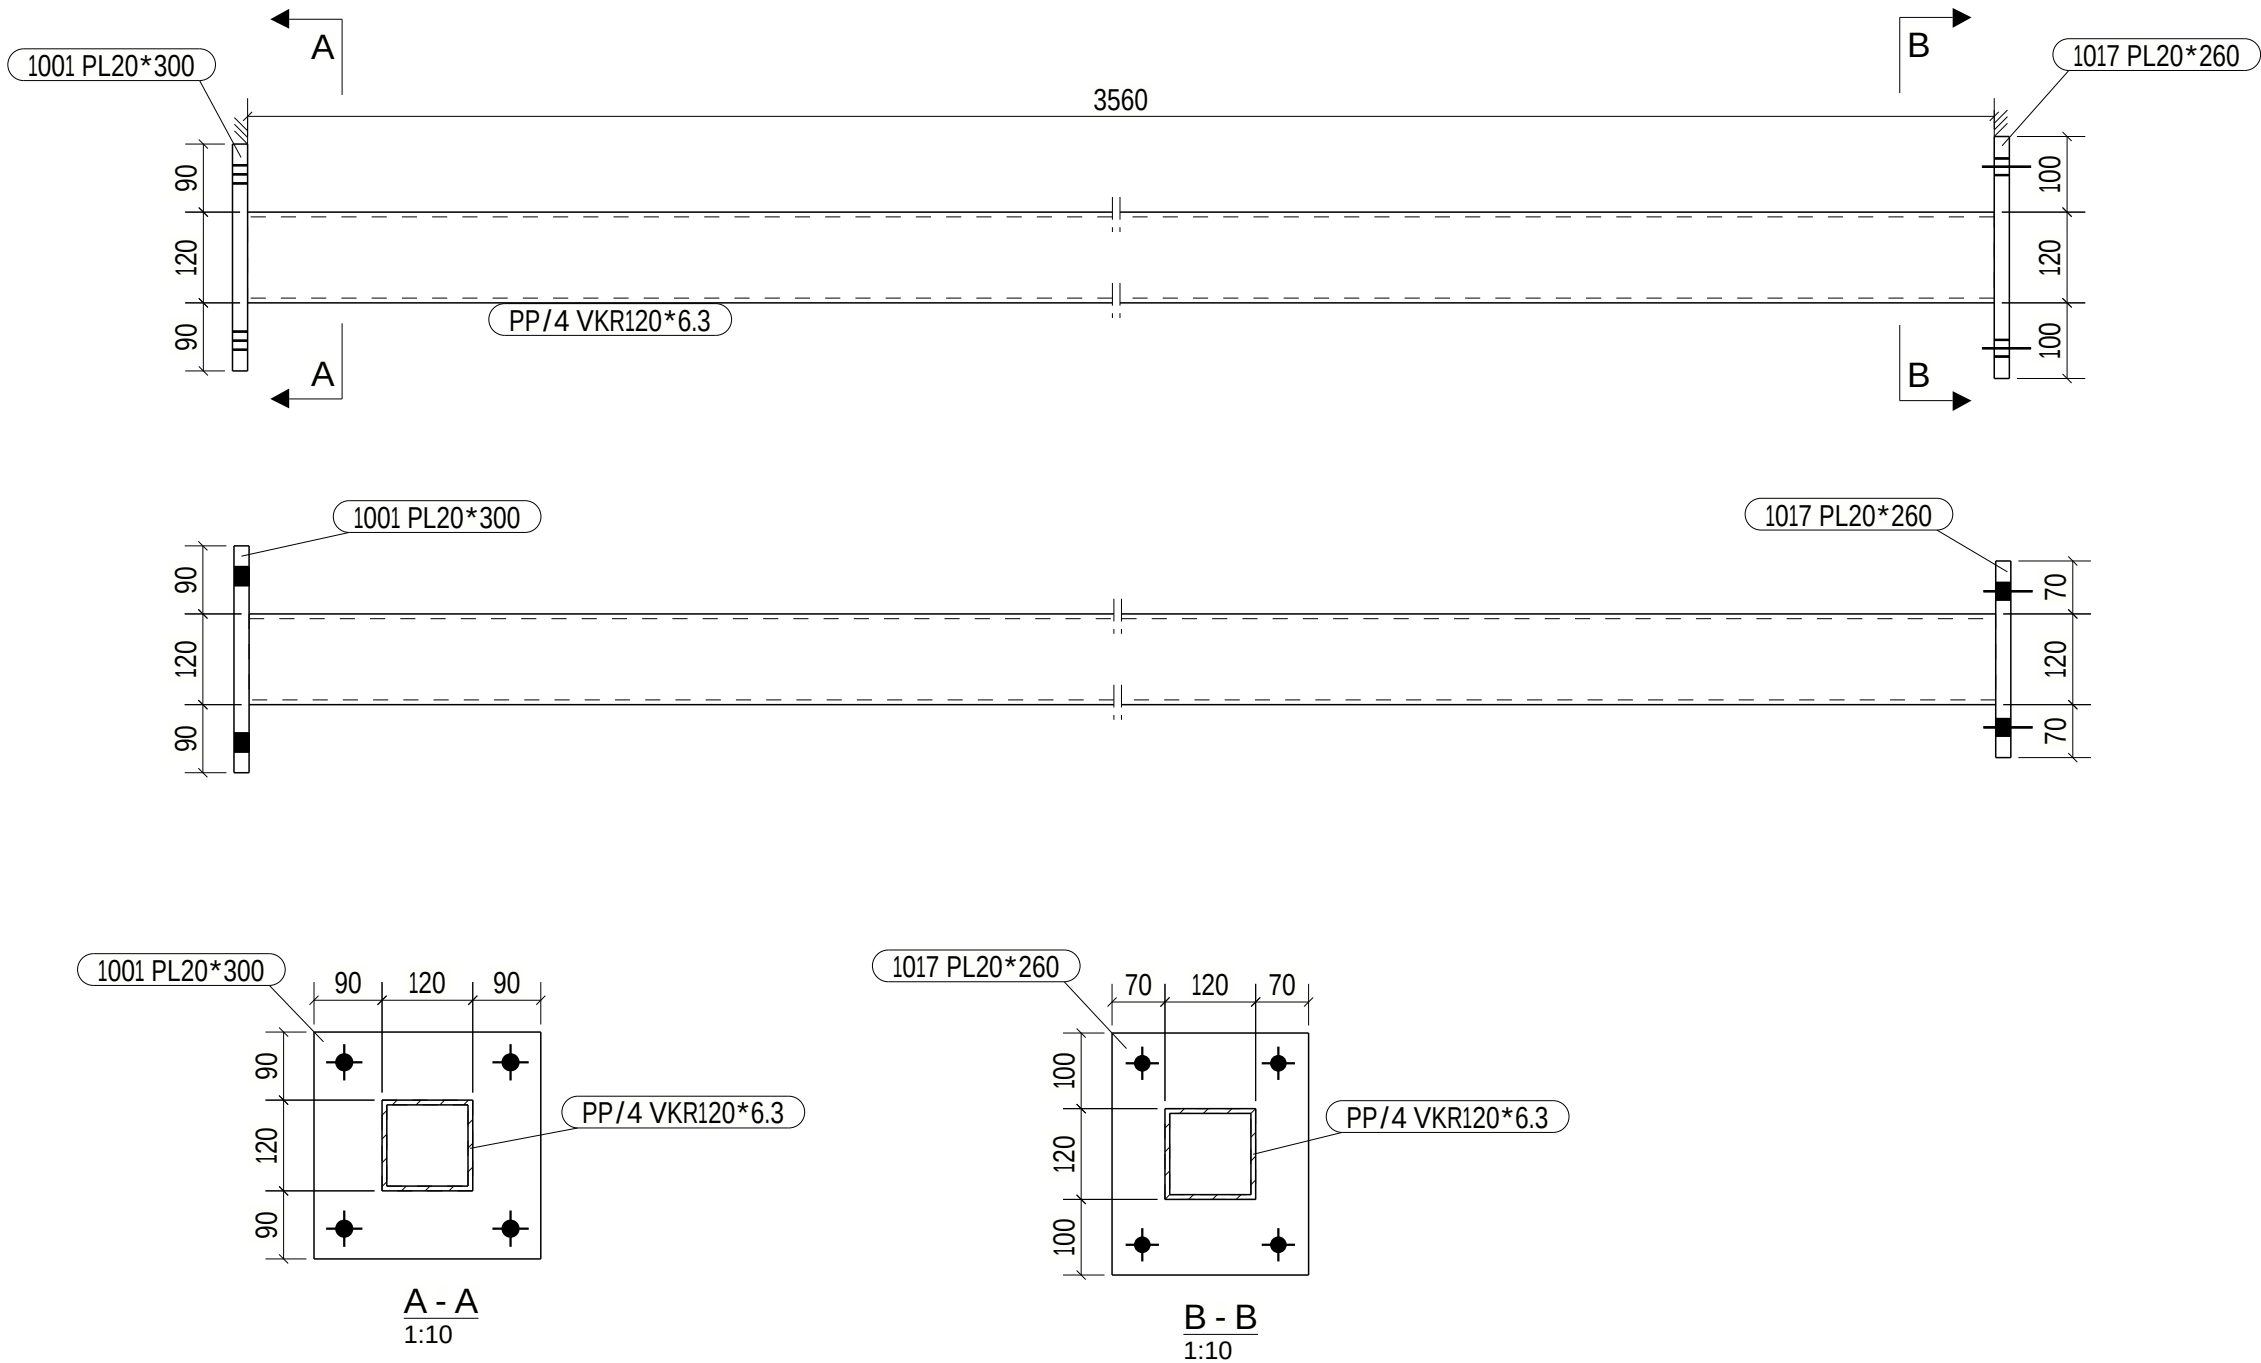

ALLMÄNNA NOTERINGAR: ALLA SVETSAR ÄR KÄLSVETS a5 OM EJ ANNAT ANGES

MATERIALLISTA FÖR ETT GODS MÄRKT: P/11						5 st. TILLVERKAS
STYCKLIT.	PROFIL	MATERIAL	ANT.	LÄNGD	AREA/st	VIKT/st
PP/4	VKR120*6.3	S355J2H	1	3560	1.6	78.8
1001	PL20*300	S355J2	1	300	0.2	14.1
1017	PL20*260	S355J2	1	320	0.2	13.1
TOTALT					2.0	106.0

Norconsult 	ANSVARIG PART	CENTRALE KÖK ROBERTSFORS KOMMUN	PROJEKT	FÖRFRÅGNINGSUNDERLAG		STATUS
	KONTAKTPERSON		BYGGHANDLING		HANDLING	
	BJÖRN LIDSTRÖM	TILLVERKNINGSRITNINGAR STÅL	RITNINGSKATEGORI	ÄNDRING	FORMAT	
	BJÖRN LIDSTRÖM		INNEHÅLL	DATUM	SKALA	
	ARVID WENNERBERG			2024-12-20	1:10	
	PARTS	NUMMER	BET			
		P/11				