
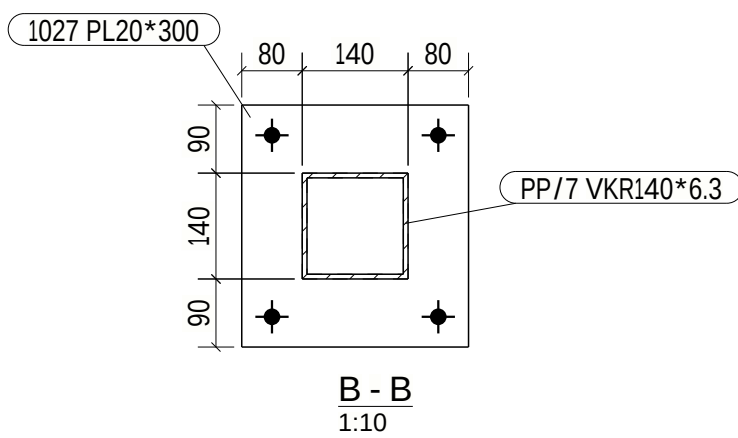
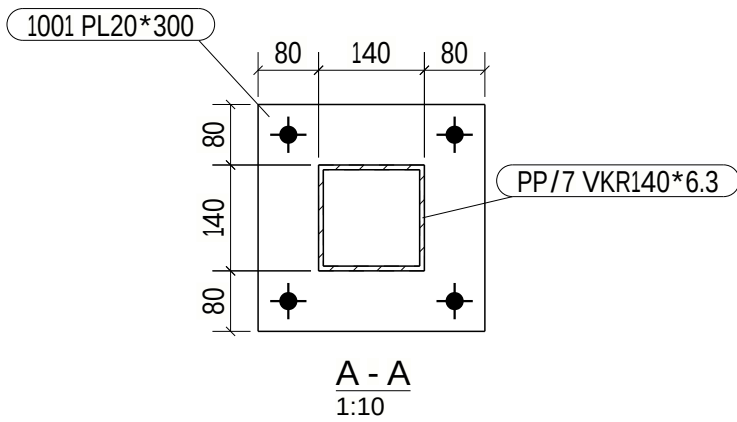


PLACERING I STOMNÄT	
NUMMER	SYSTEMLINJE
P/13	4/B-C

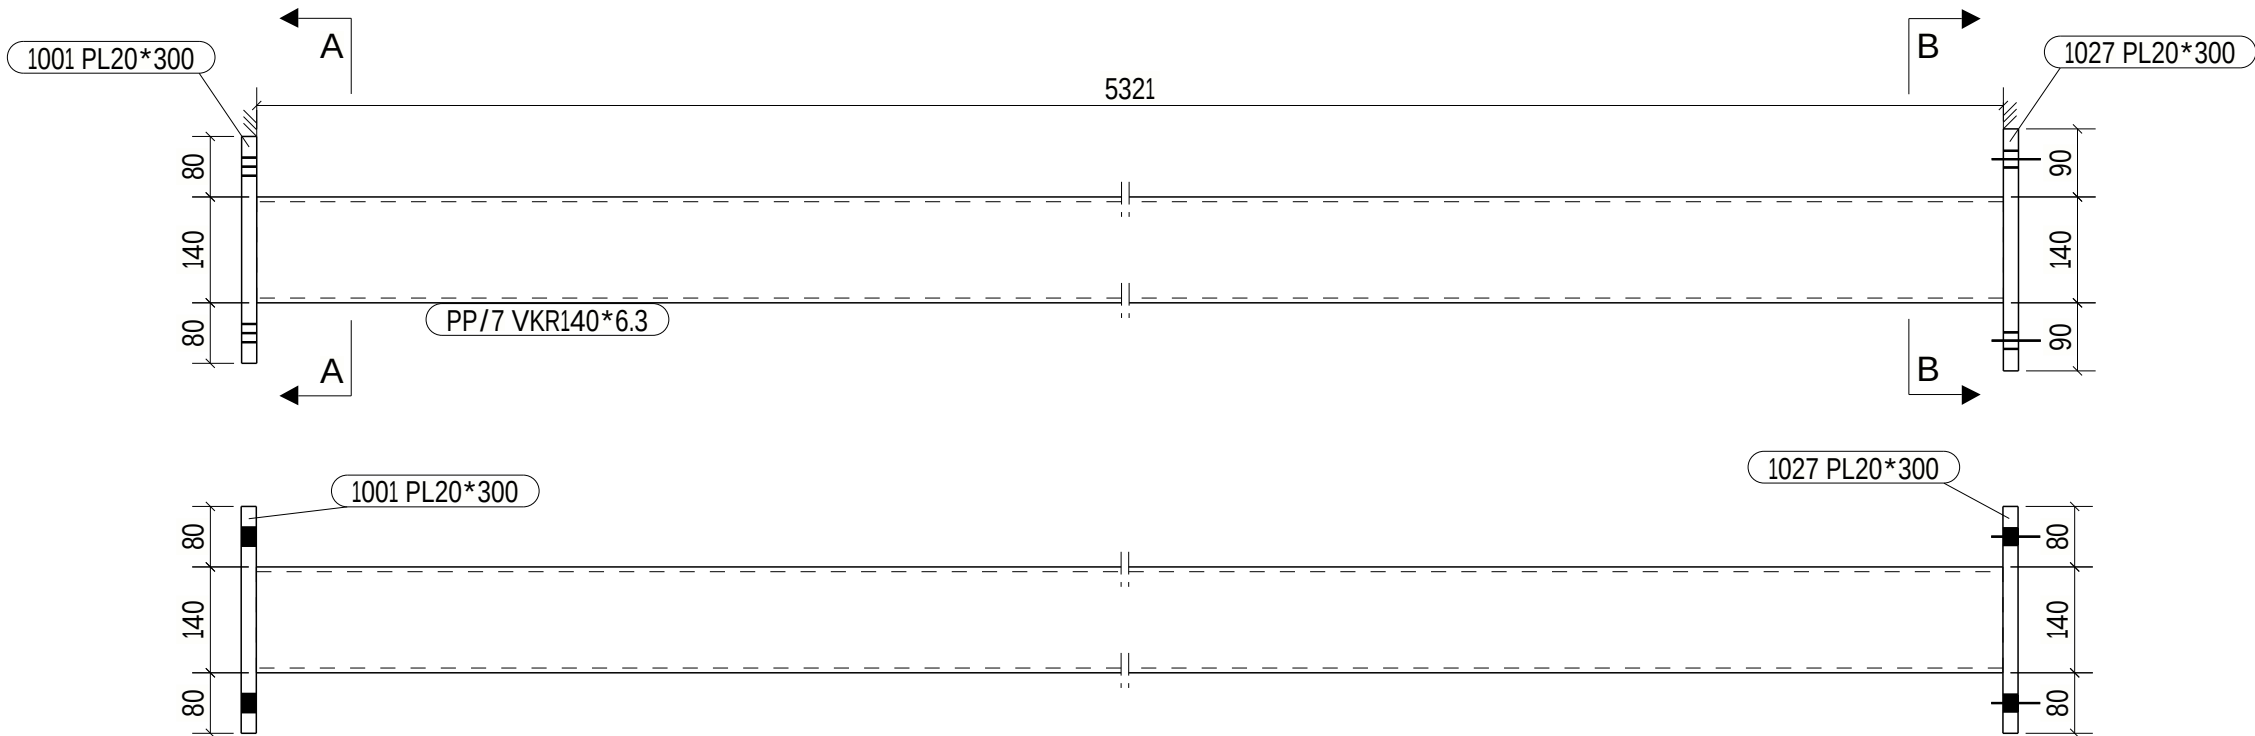

ALLMÄNNA NOTERINGAR: ALLA SVETSAR ÄR KÄLSVETS a5 OM EJ ANNAT ANGES

MATERIALLISTA FÖR ETT GODS MÄRKT: P/13						1 st. TILLVERKAS
STYCKLIT.	PROFIL	MATERIAL	ANT.	LÄNGD	AREA/st	VIKT/st
PP/7	VKR140*6.3	S355J2H	1	5321	2.9	139.1
1027	PL20*300	S355J2	1	320	0.2	15.1
1001	PL20*300	S355J2	1	300	0.2	14.1
TOTALT					3.3	168.3

Norconsult 	ANSVARIG PART	PROJEKT	FÖRFRÅGNINGSUNDERLAG		STATUS
	KONTAKTPERSON	CENTRALEKÖB ROBERTSFORS KOMMUN	BYGGHANDLING		HANDLING
	GODKÄND AV	TILLVERKNINGSRITNINGAR STÅL	ÄNDRING		FORMAT
	SKAPAD AV	PARTS	INNEHÅLL		SKALA
BJÖRN LIDSTRÖM			2024-12-20		A3
BJÖRN LIDSTRÖM			NUMMER		BET
ARVID WENNERBERG			P/13		