


PLACERING I STOMNÄT	
NUMMER	SYSTEMLINJE
P/14	4/B-C

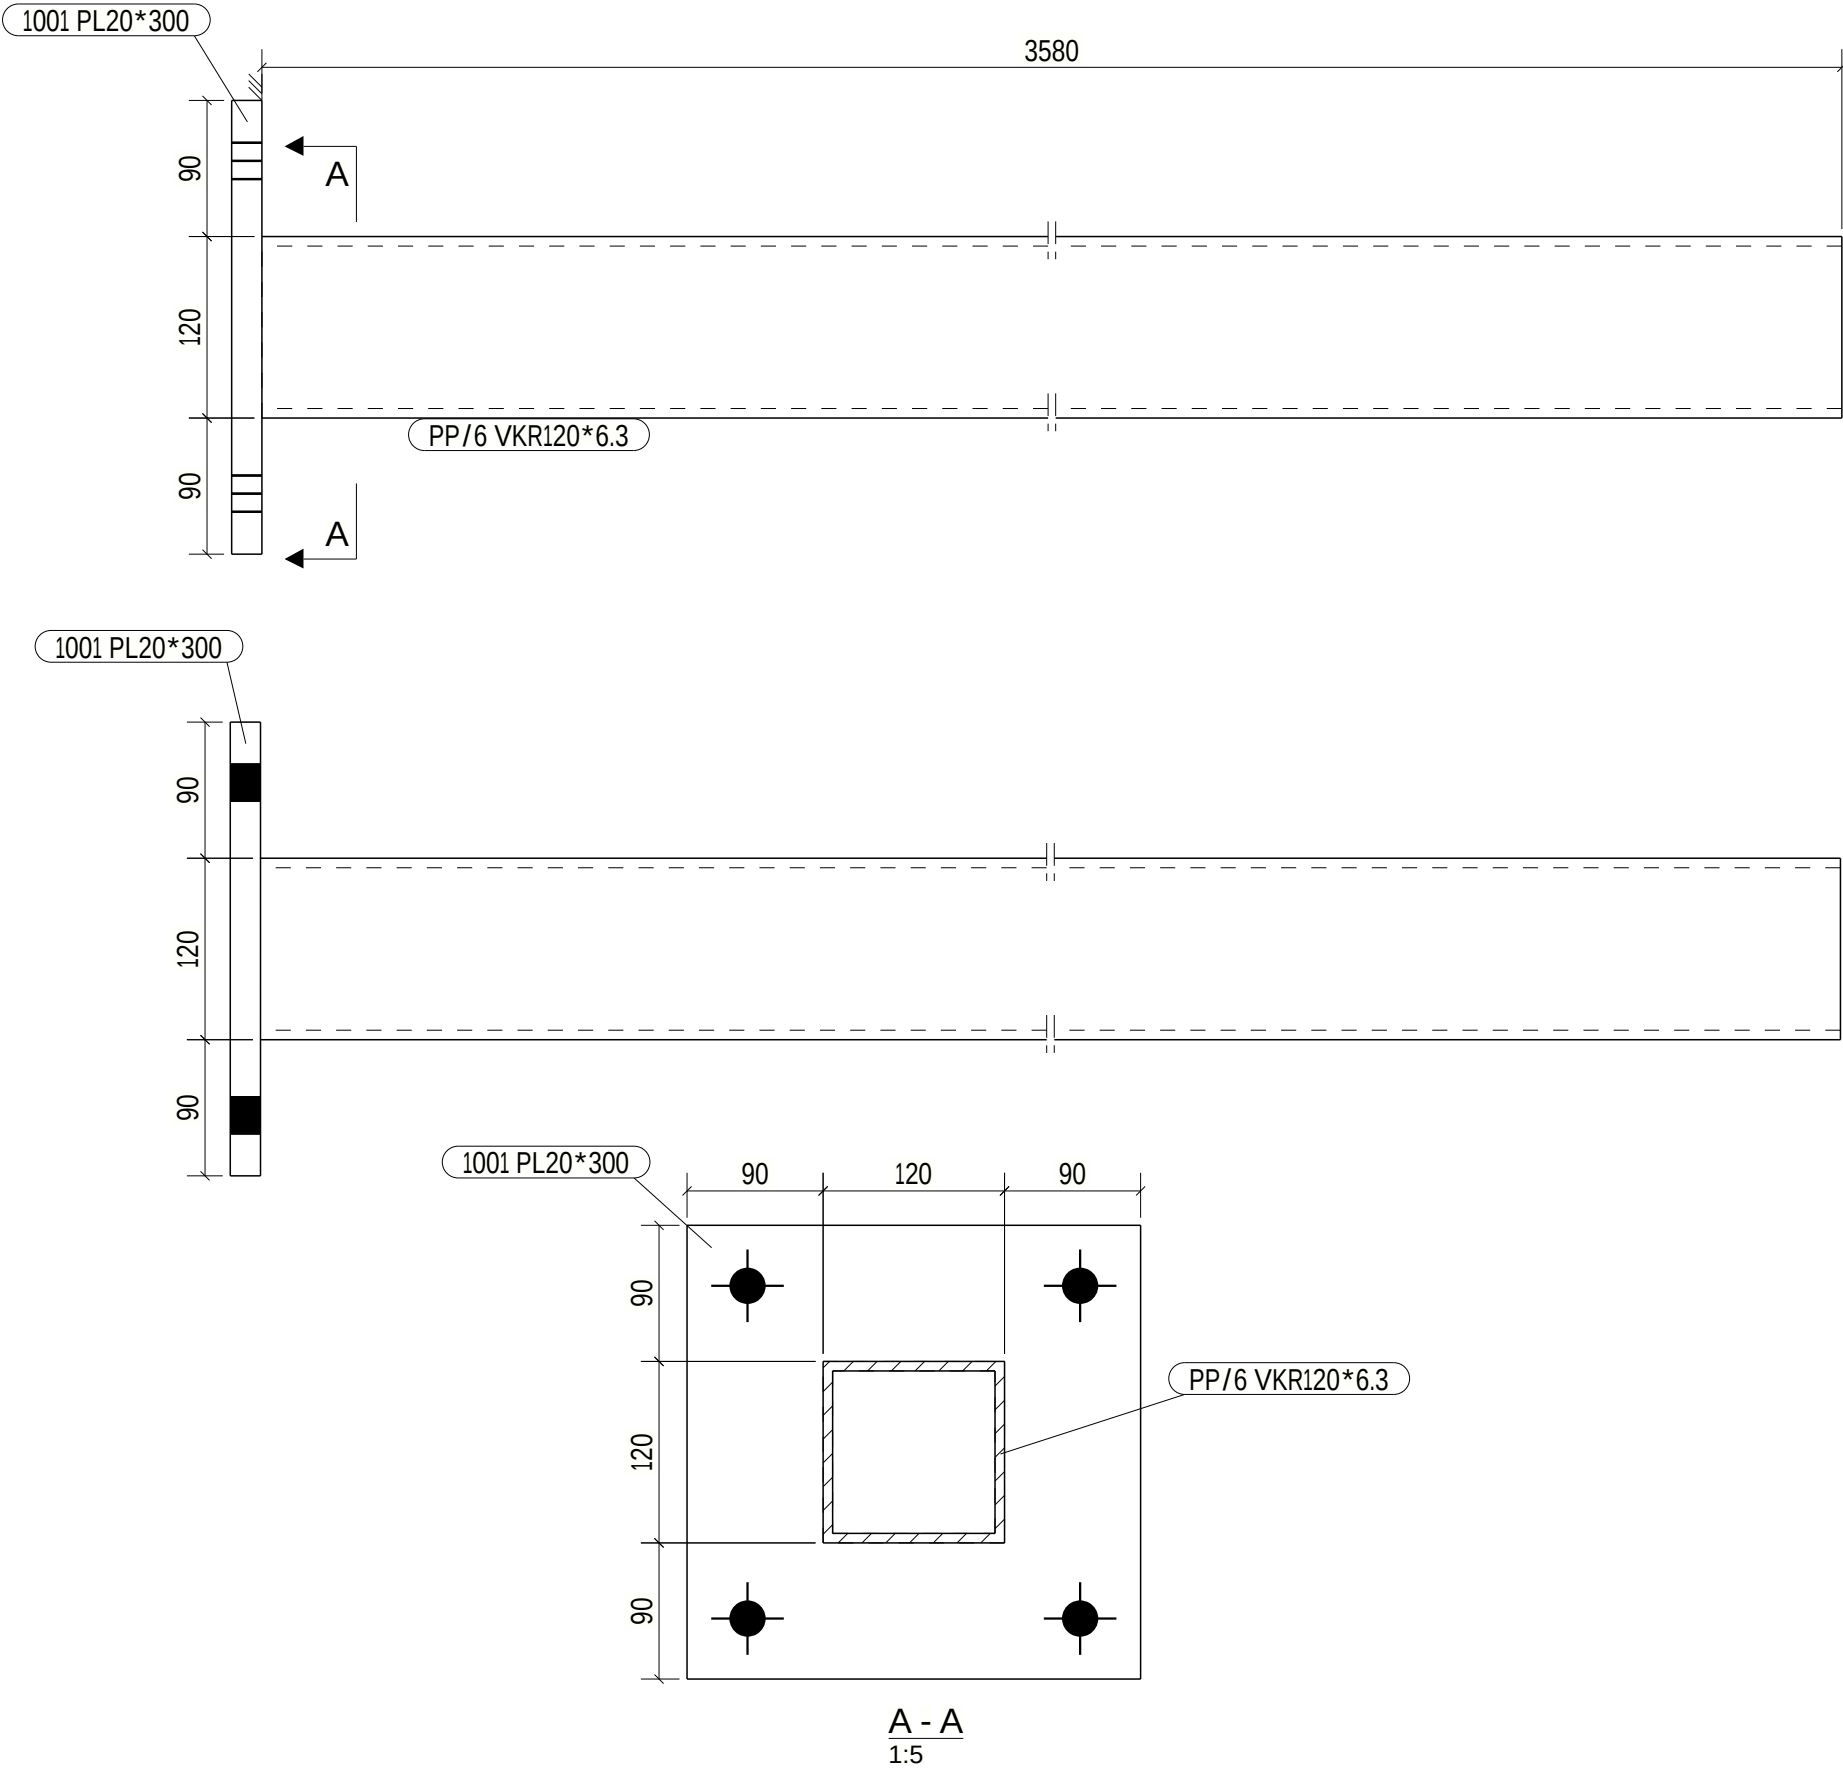

ALLMÄNNA NOTERINGAR: ALLA SVETSAR ÄR KÄLSVETS a5 OM EJ ANNAT ANGES

MATERIALLISTA FÖR ETT GODS MÄRKT: P/14 1 st. TILLVERKAS						
STYCKLIT.	PROFIL	MATERIAL	ANT.	LÄNGD	AREA/st	VIKT/st
PP/6	VKR120*6.3	S355J2H	1	3580	1.6	79.3
1001	PL20*300	S355J2	1	300	0.2	14.1
TOTALT					1.9	93.4

Norconsult	ANSVARIG PART	PROJEKT	FÖRFRÅGNINGSUNDERLAG		STATUS
	KONTAKTPERSON	CENTRALKÖK ROBERTSFORS KOMMUN	BYGGHANDLING		HANDLING
	GODKÄND AV	TILLVERKNINGSRITNINGAR STÅL	ÄNDRING	FORMAT	A3
	SKAPAD AV	INNEHÅLL	2024-12-20	DATUM	1:5
PARTS			P/14	NUMMER	BET