

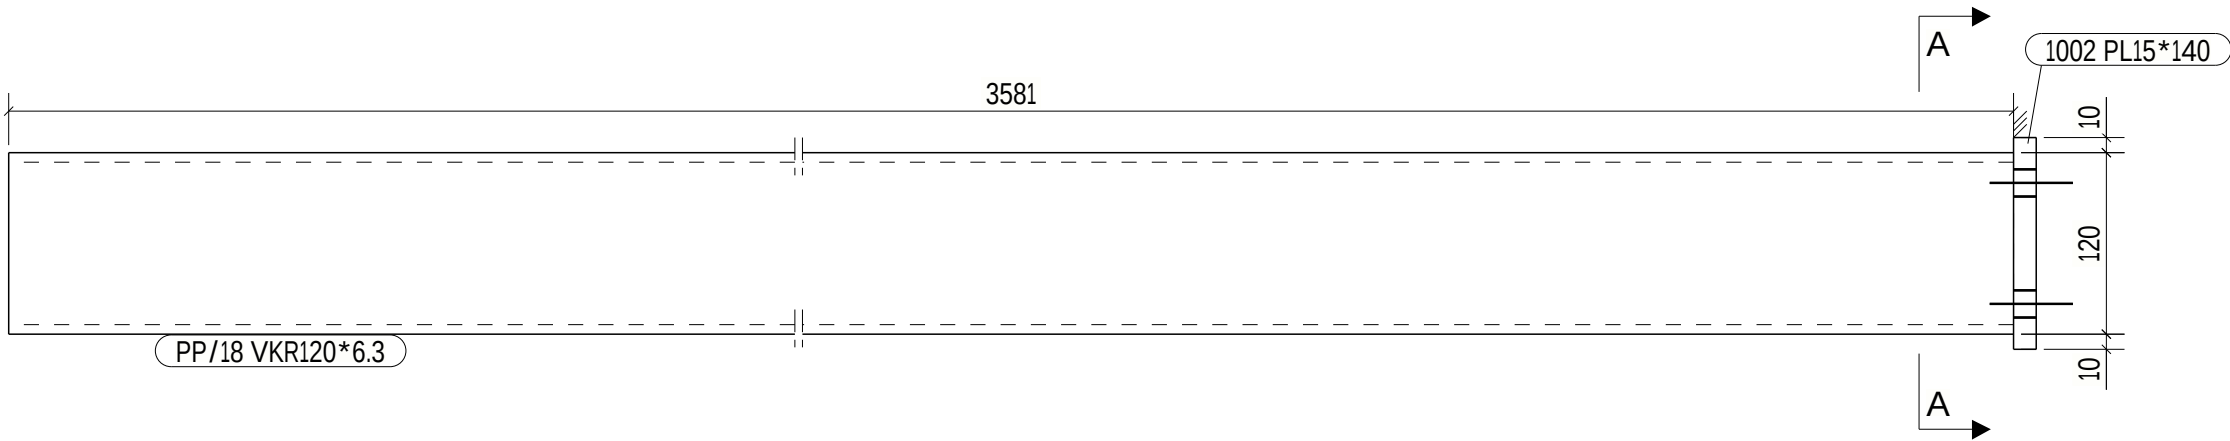


PLACERING I STOMNÄT	
NUMMER	SYSTEMLINJE
P/16	6-7/B-C

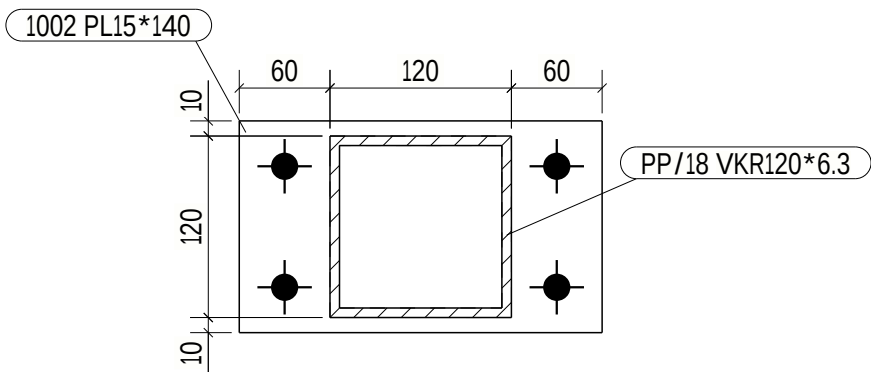

UTVÄNDIGT STÅL VARMFÖRZINKAS ENLIGT ALLMÄNNA FÖRESKRIFTER K-01-0-001 -- 003

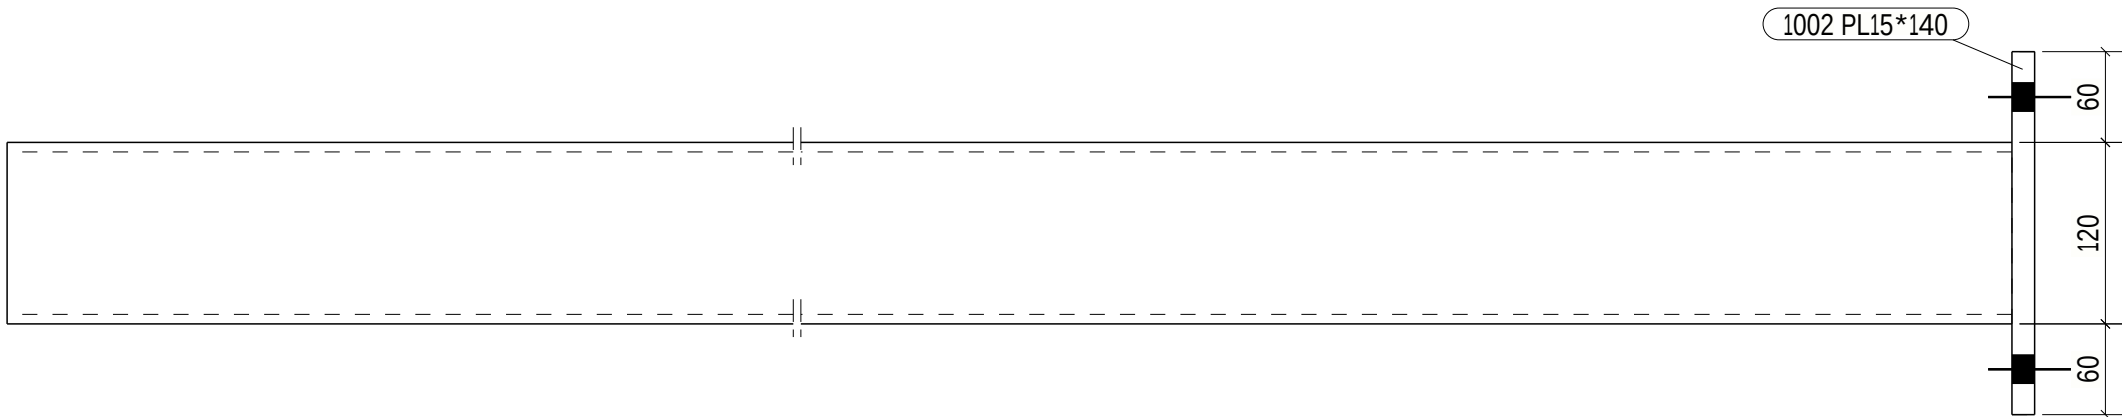

A - A
1:5

ALLMÄNNA NOTERINGAR: ALLA SVETSAR ÄR KÄLSVETS a5 OM EJ ANNAT ANGES

MATERIALLISTA FÖR ETT GODS MÄRKT: P/16						1 st. TILLVERKAS
STYCKLIT.	PROFIL	MATERIAL	ANT.	LÄNGD	AREA/st	VIKT/st
PP/18	VKR120*6.3	S355J2H	1	3581	1.6	79.3
1002	PL15*140	S355J2	1	240	0.1	4.0
TOTALT					1.7	83.2

Norconsult	ANSVARIG PART	PROJEKT	FÖRFRÅGNINGSUNDERLAG		STATUS
	KONTAKTPERSON	CENTRALKÖK ROBERTSFORS KOMMUN	BYGGHANDLING		HANDLING
	GODKÄND AV	TILLVERKNINGSRITNINGAR STÅL	ÄNDRING	FORMAT	A3
	SKAPAD AV	INNEHÅLL	2024-12-20	DATUM	1:5
PARTS			NUMMER	BET	P/16