
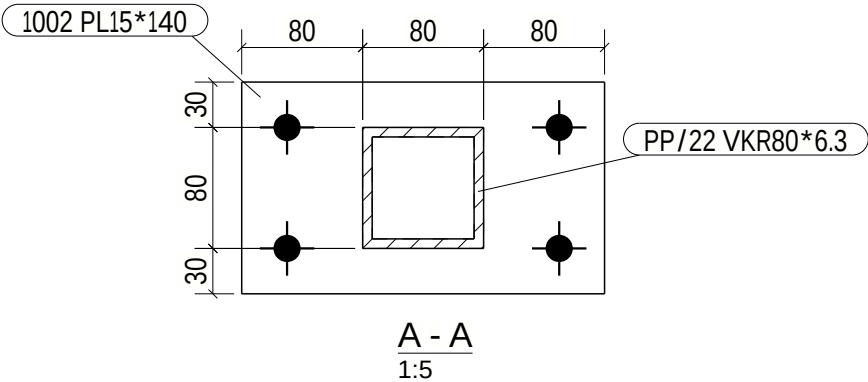


PLACERING I STOMNÄT	
NUMMER	SYSTEMLINJE
P/17	<1/C-D

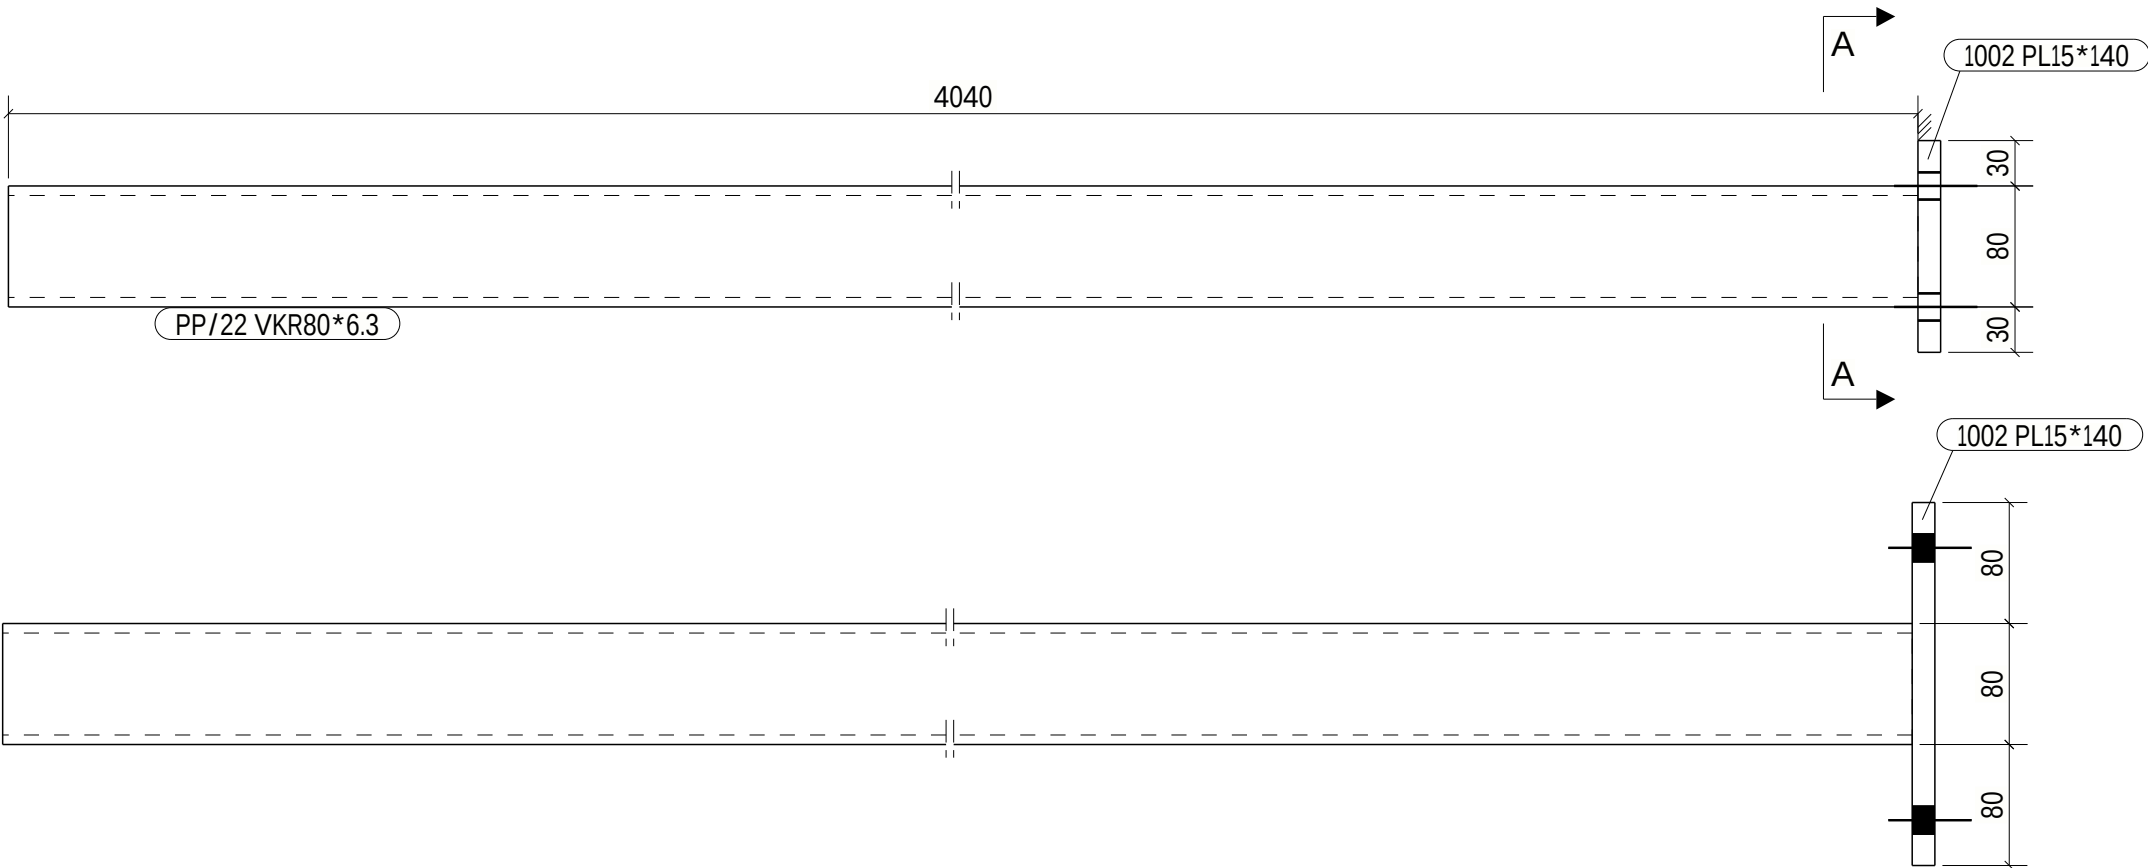

ALLMÄNNA NOTERINGAR: ALLA SVETSAR ÄR KÄLSVETS a5 OM EJ ANNAT ANGES						
MATERIALLISTA FÖR ETT GODS MÄRKT:			P/17 1 st. TILLVERKAS			
STYCKLIT.	PROFIL	MATERIAL	ANT.	LÄNGD	AREA/st	VIKT/st
PP/22	VKR80*6.3	S355J2H	1	4040	1.2	57.4
1002	PL15*140	S355J2	1	240	0.1	4.0
TOTALT					1.3	61.4

Norconsult	ANSVARIG PART	PROJEKT	FÖRFRÅGNINGSUNDERLAG		STATUS
	KONTAKTPERSON	CENTRALKÖK ROBERTSFORS KOMMUN	BYGGHANDLING		HANDLING
	GODKÄND AV	TILLVERKNINGSRITNINGAR STÅL	ÄNDRING	FORMAT	A3
	SKAPAD AV	PARTS	INNEHÅLL	DATUM	SKALA
			2024-12-20	1:5	BET
			NUMMER	P/17	