
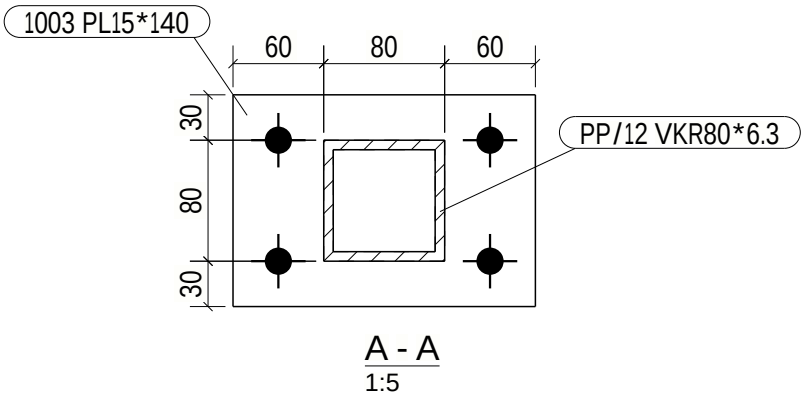


PLACERING I STOMNÄT	
NUMMER	SYSTEMLINJE
P/18	6/B

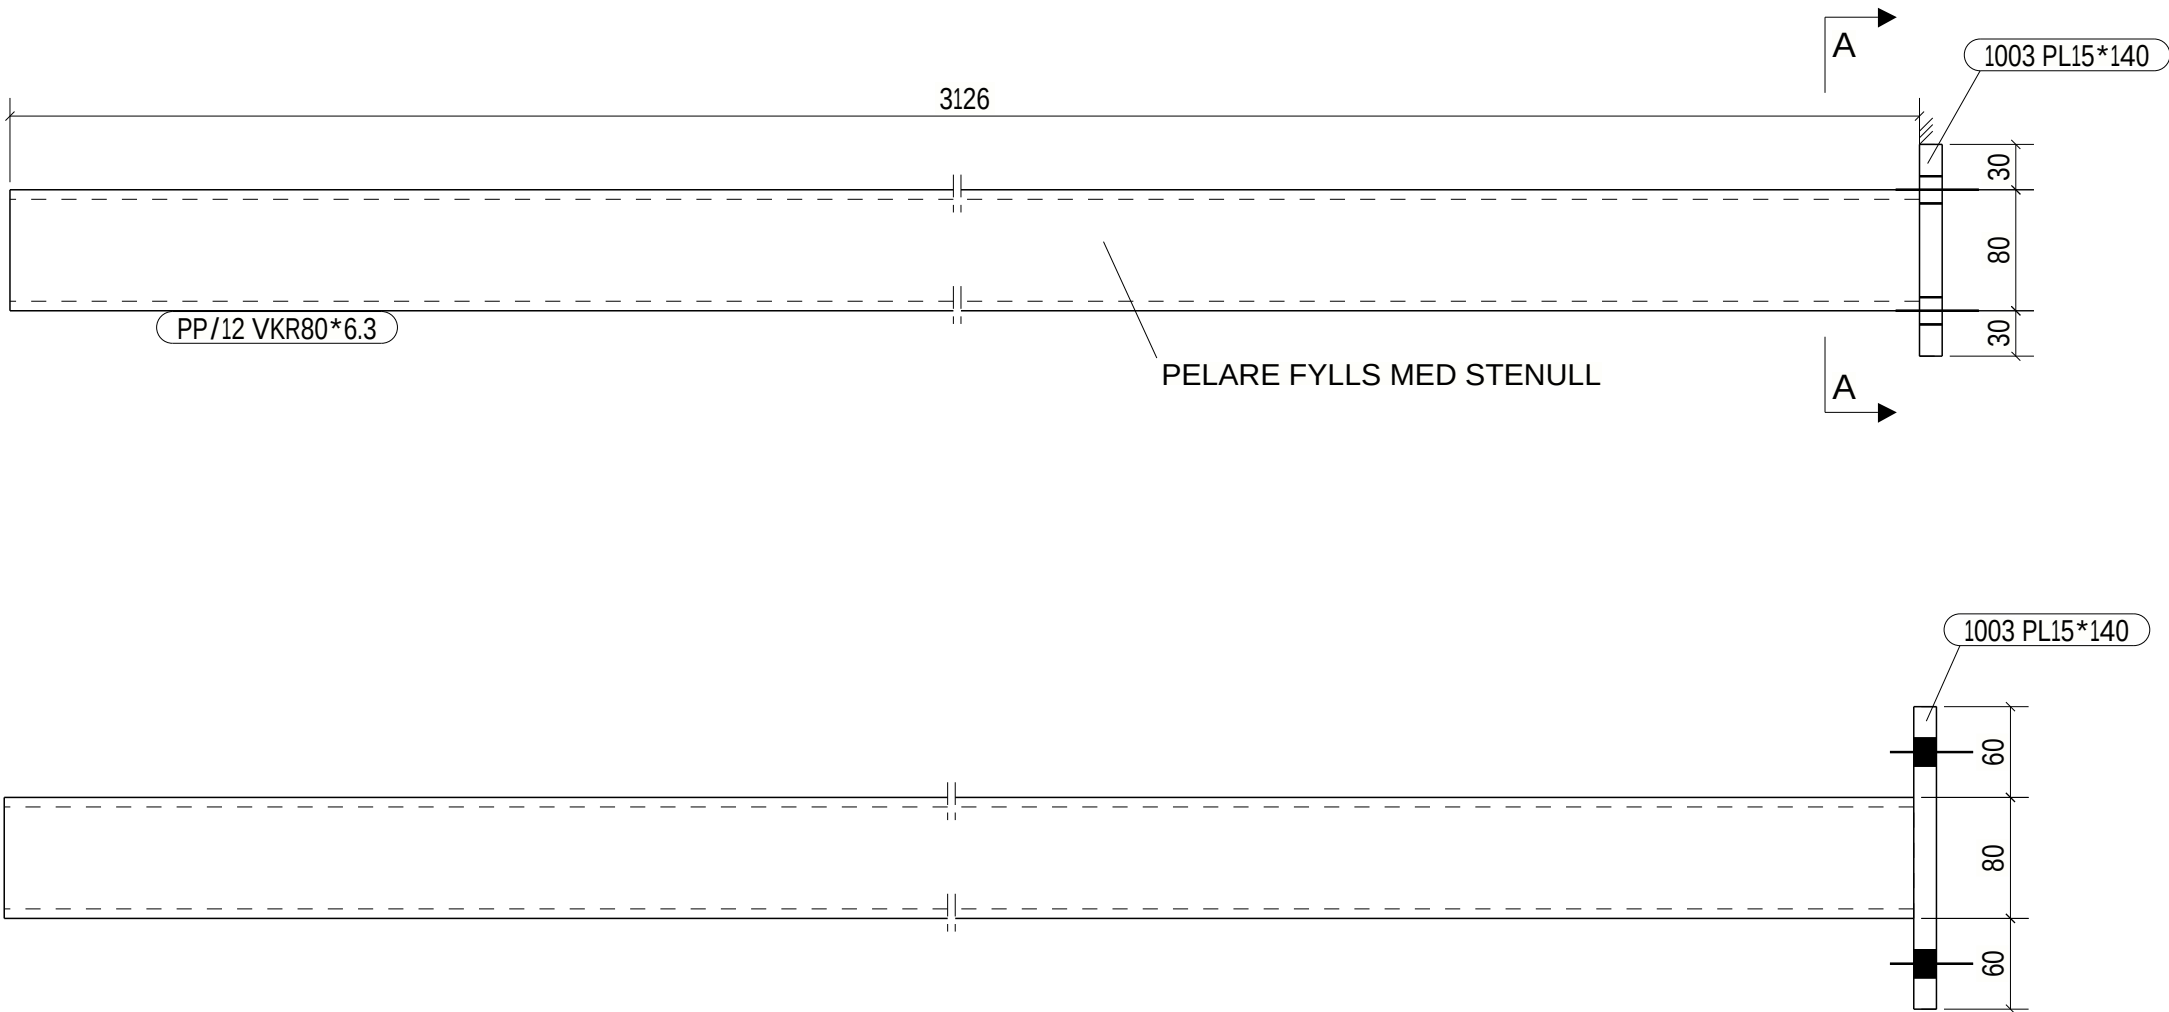

ALLMÄNNA NOTERINGAR: ALLA SVETSAR ÄR KÄLSVETS a5 OM EJ ANNAT ANGES						
MATERIALLISTA FÖR ETT GODS MÄRKT: P/18 1 st. TILLVERKAS						
STYCKLIT.	PROFIL	MATERIAL	ANT.	LÄNGD	AREA/st	VIKT/st
PP/12	VKR80*6.3	S355J2H	1	3126	0.9	44.4
1003	PL15*140	S355J2	1	200	0.1	3.3
TOTALT					1.0	47.7

Norconsult	ANSVARIG PART	PROJEKT	FÖRFRÅGNINGSUNDERLAG		STATUS
	KONTAKTPERSON	CENTRALKÖK ROBERTSFORS KOMMUN	BYGGHANDLING		HANDLING
	GODKÄND AV	TILLVERKNINGSRITNINGAR STÅL	ÄNDRING	FORMAT	A3
	SKAPAD AV	INNEHÅLL	2024-12-20	DATUM	1:5
PARTS			NUMMER	BET	
			P/18		