
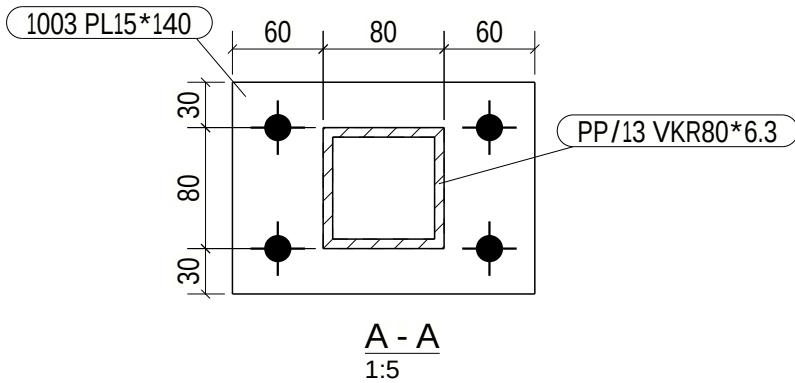
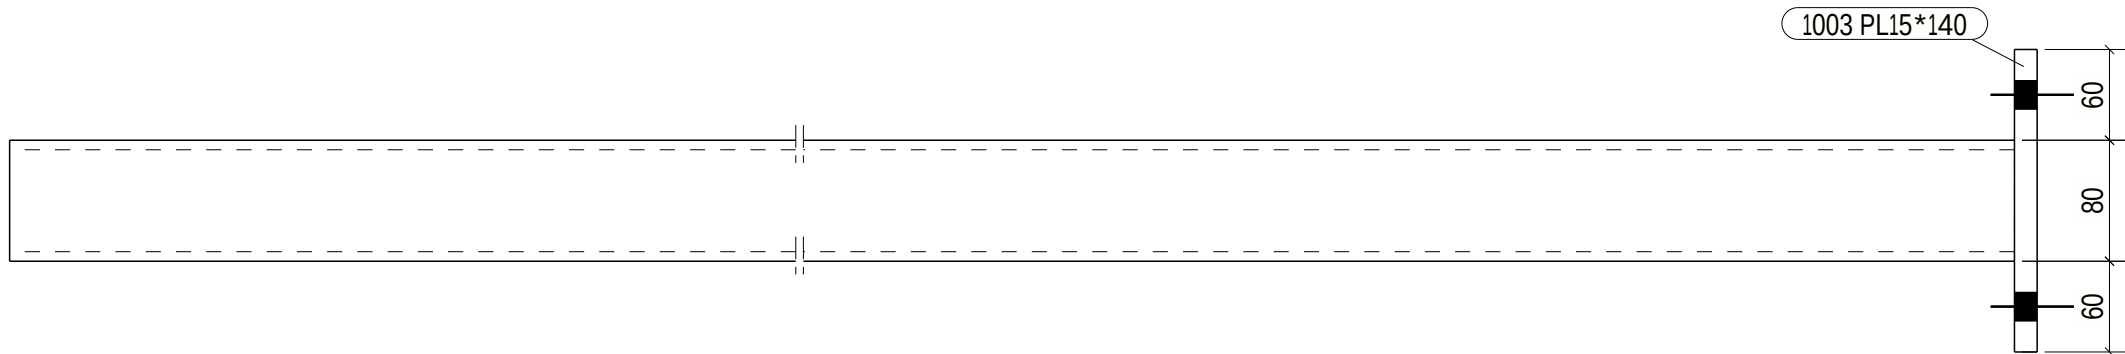


PLACERING I STOMNÄT	
NUMMER	SYSTEMLINJE
P/19	6/B-C

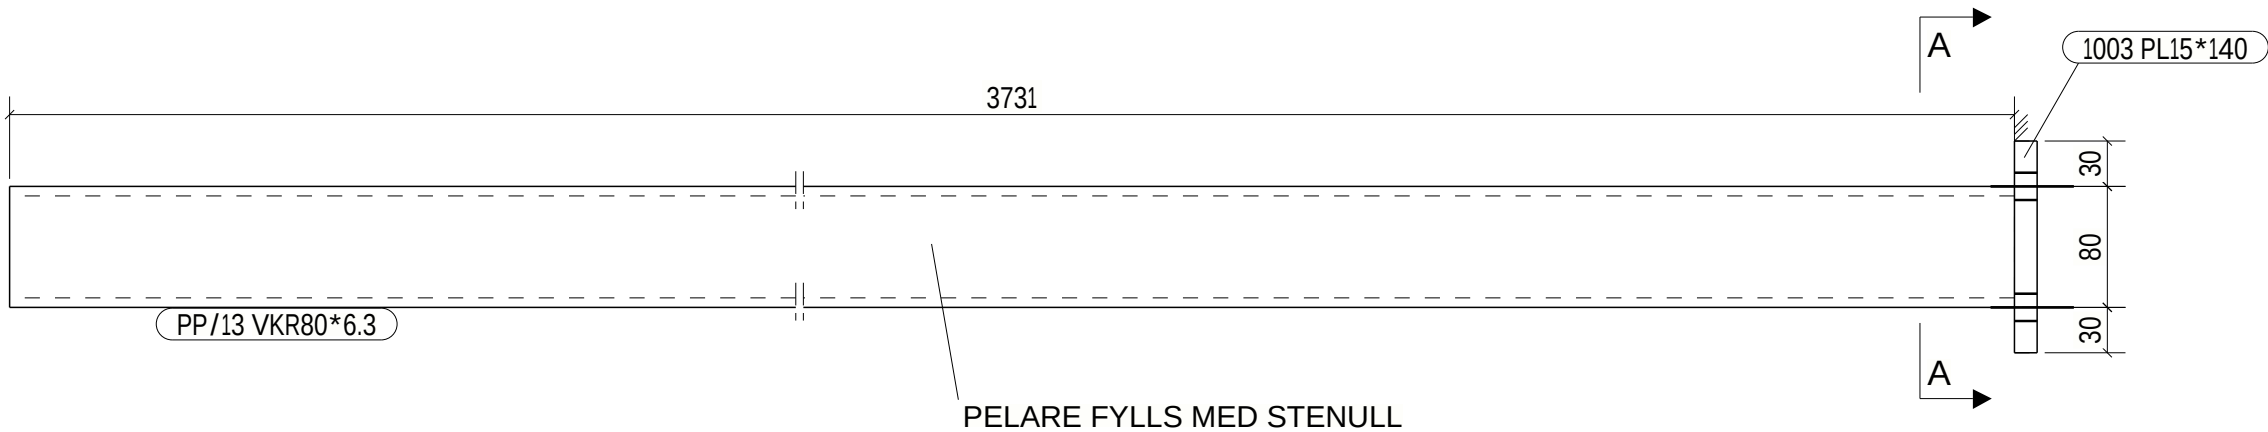

ALLMÄNNA NOTERINGAR: ALLA SVETSAR ÄR KÄLSVETS a5 OM EJ ANNAT ANGES						
MATERIALLISTA FÖR ETT GODS MÄRKT: P/19 1 st. TILLVERKAS						
STYCKLIT.	PROFIL	MATERIAL	ANT.	LÄNGD	AREA/st	VIKT/st
PP/13	VKR80*6.3	S355J2H	1	3731	1.1	53.0
1003	PL15*140	S355J2	1	200	0.1	3.3
TOTALT					1.2	56.3

Norconsult	ANSVARIG PART	PROJEKT	FÖRFRÅGNINGSUNDERLAG		STATUS
	KONTAKTPERSON	CENTRALEKÖB ROBERTSFORS KOMMUN	BYGGHANDLING		HANDLING
	GODKÄND AV	TILLVERKNINGSRITNINGAR STÅL	ÄNDRING		FORMAT
	SKAPAD AV	INNEHÅLL	2024-12-20		SKALA
PARTS			NUMMER	P/19	BET