

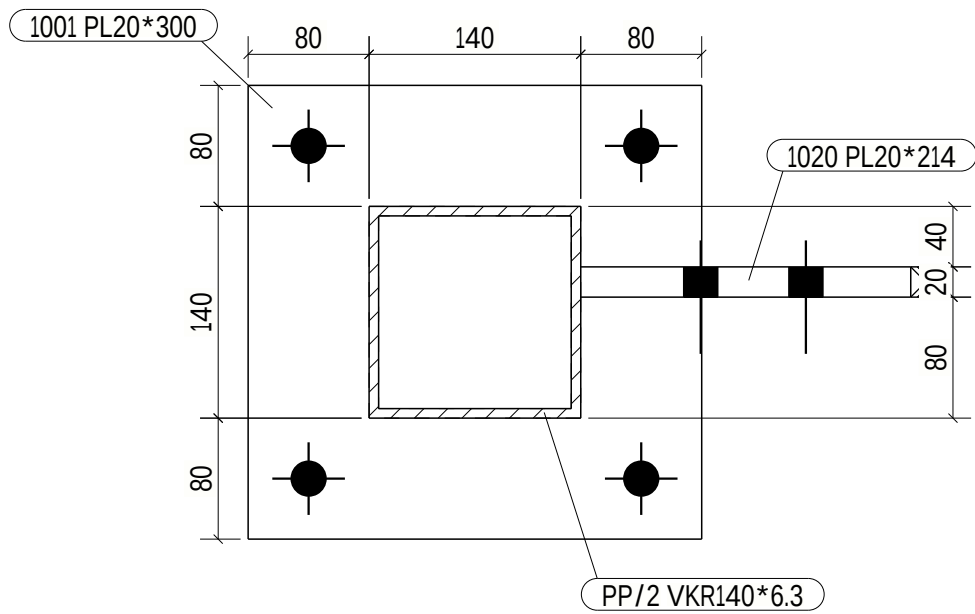
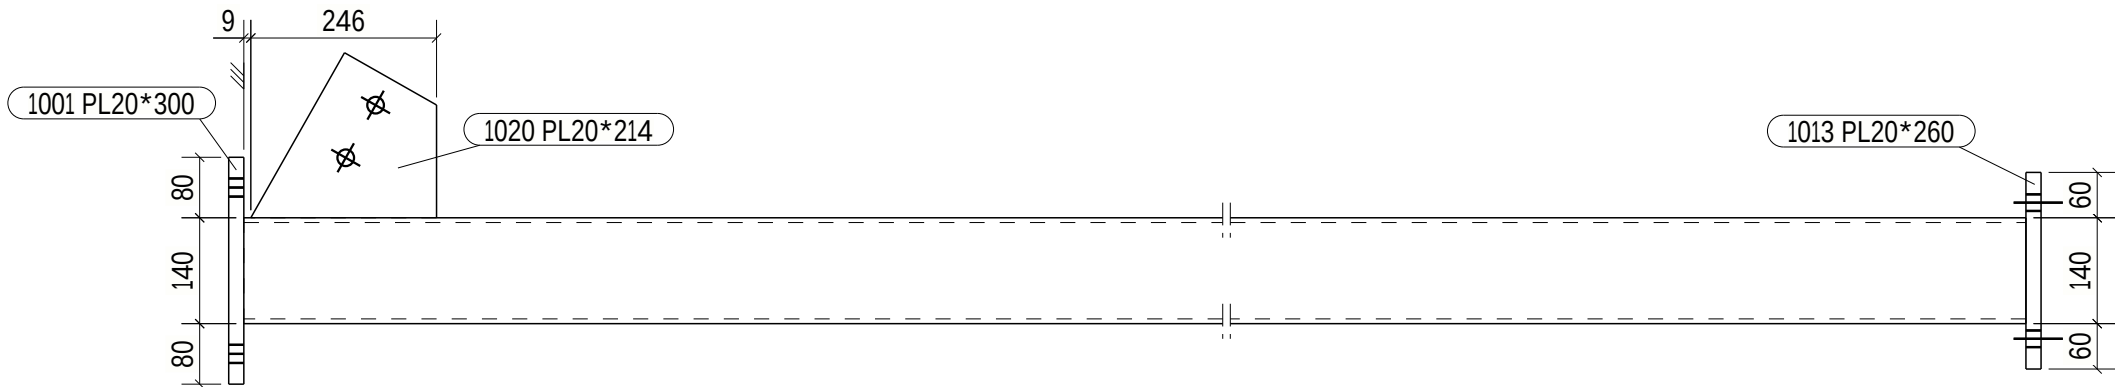


| PLACERING I STOMNÄT |             |
|---------------------|-------------|
| NUMMER              | SYSTEMLINJE |
| P/2                 | 4/A         |

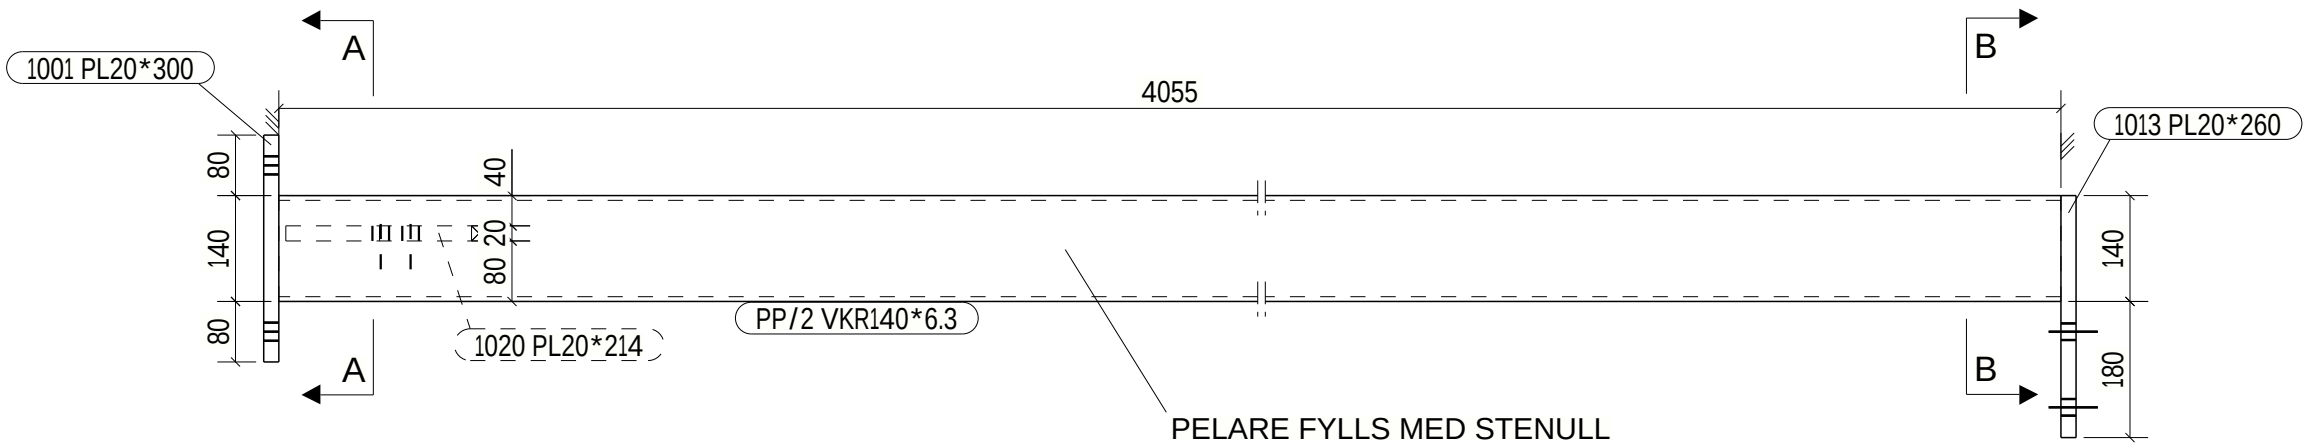

A - A  
1:5

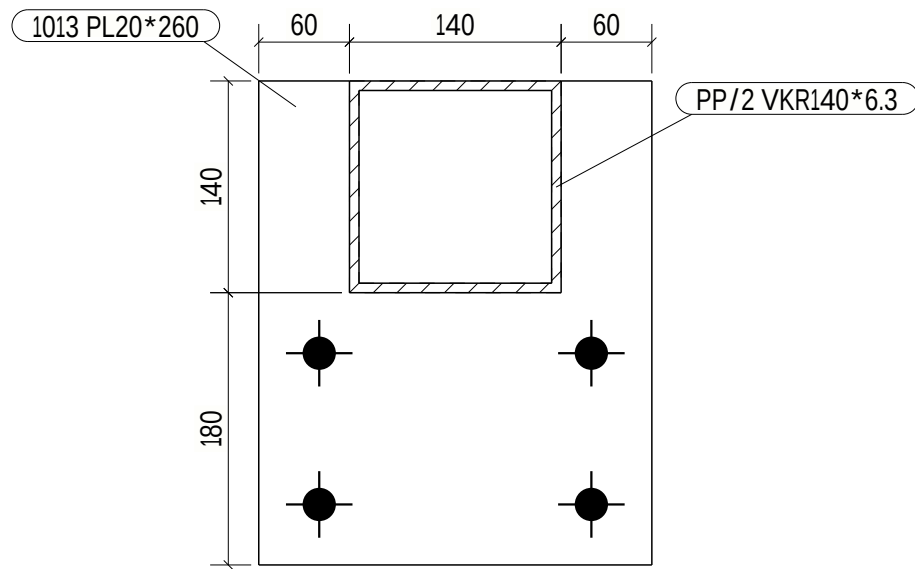

B - B  
1:5

ALLMÄNNA NOTERINGAR: ALLA SVETSAR ÄR KÄLSVETS a5 OM EJ ANNAT ANGES

| MATERIALLISTA FÖR ETT GODS MÄRKT: P/2 1 st. TILLVERKAS |            |          |      |       |         |         |
|--------------------------------------------------------|------------|----------|------|-------|---------|---------|
| STYCKLIT.                                              | PROFIL     | MATERIAL | ANT. | LÄNGD | AREA/st | VIKT/st |
| PP/2                                                   | VKR140*6.3 | S355J2H  | 1    | 4055  | 2.2     | 106.0   |
| 1001                                                   | PL20*300   | S355J2   | 1    | 300   | 0.2     | 14.1    |
| 1013                                                   | PL20*260   | S355J2   | 1    | 320   | 0.2     | 13.1    |
| 1020                                                   | PL20*214   | S355J2   | 1    | 251   | 0.1     | 5.6     |
| TOTALT                                                 |            |          |      |       | 2.7     | 138.8   |

|                                                                                                  |  |               |                                |  |                   |                      |     |          |
|--------------------------------------------------------------------------------------------------|--|---------------|--------------------------------|--|-------------------|----------------------|-----|----------|
| Norconsult  |  | ANSVARIG PART | CENTRALE KÖ ROBERTSFORS KOMMUN |  | PROJEKT           | FÖRFRÅGNINGSUNDERLAG |     | STATUS   |
| BJÖRN LIDSTRÖM                                                                                   |  | KONTAKTPERSON | TILLVERKNINGSRITNINGAR STÅL    |  | RIITNINGSKATEGORI | BYGGHANDLING         |     | HANDLING |
| BJÖRN LIDSTRÖM                                                                                   |  | GODKÄND AV    |                                |  |                   | ÄNDRING              | A3  | FORMAT   |
| ARVID WENNERBERG                                                                                 |  | SKAPAD AV     | PARTS                          |  | INNEHÅLL          | DATUM                | 1:5 | SKALA    |
|                                                                                                  |  |               |                                |  |                   | 2024-12-20           |     | BET      |
|                                                                                                  |  |               |                                |  |                   | NUMMER               | P/2 |          |