

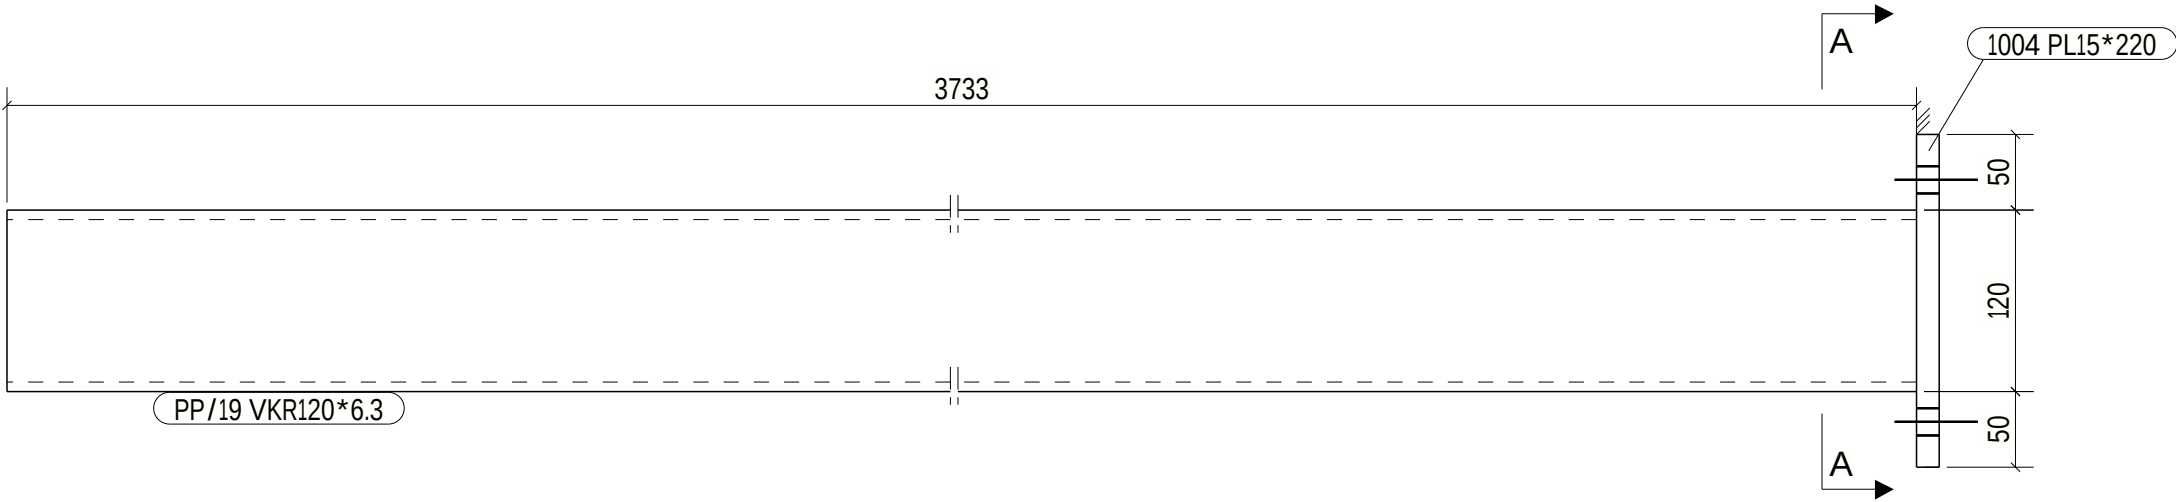


PLACERING I STOMNÄT	
NUMMER	SYSTEMLINJE
P/20	7/B-C

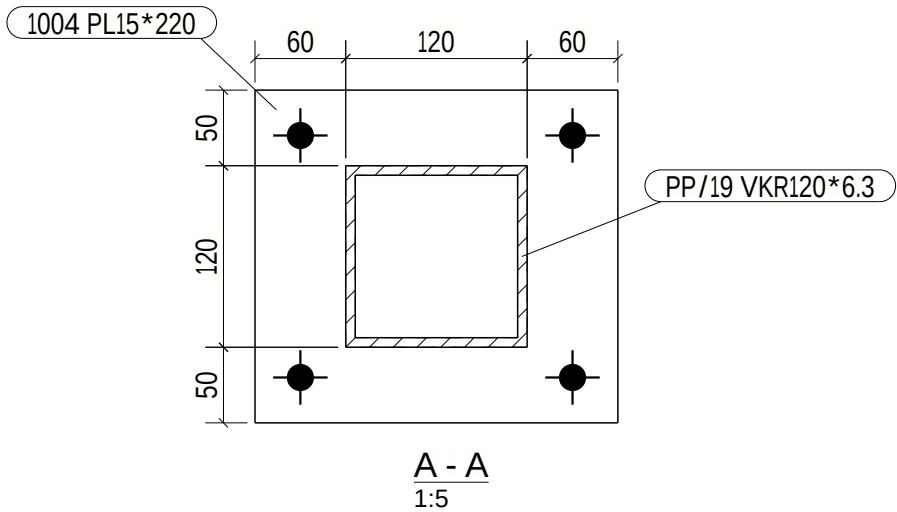

UTVÄNDIGT STÅL VARMFÖRZINKAS ENLIGT
ALLMÄNNA FÖRESKRIFTER K-01-0-001 -- 003

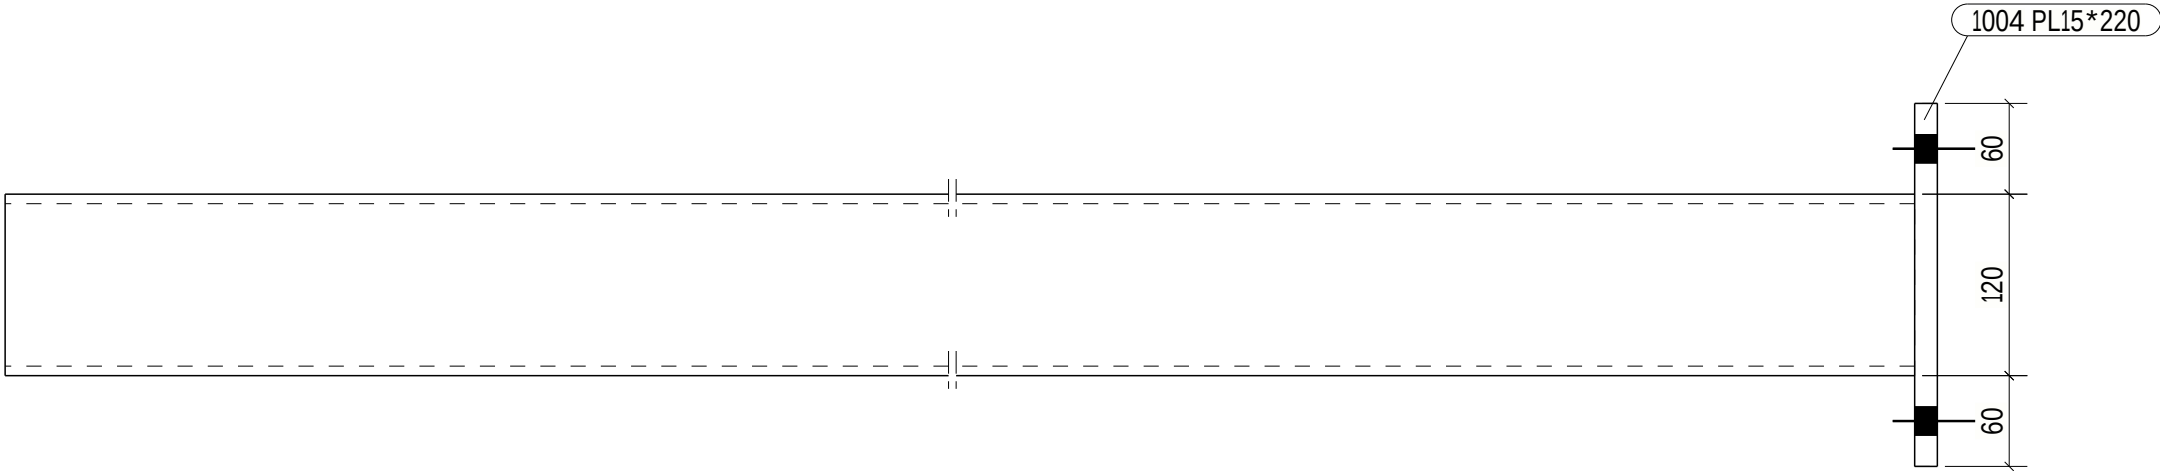

ALLMÄNNA NOTERINGAR: ALLA SVETSAR ÄR KÄLSVETS a5 OM EJ ANNAT ANGES

MATERIALLISTA FÖR ETT GODS MÄRKT: P/20 1 st. TILLVERKAS						
STYCKLIT.	PROFIL	MATERIAL	ANT.	LÄNGD	AREA/st	VIKT/st
PP/19	VKR120*6.3	S355J2H	1	3733	1.7	82.6
1004	PL15*220	S355J2	1	240	0.1	6.2
TOTALT					1.8	88.9

Norconsult	ANSVARIG PART	PROJEKT	FÖRFRÅGNINGSUNDERLAG		STATUS
	KONTAKTPERSON	CENTRALKÖK ROBERTSFORS KOMMUN	BYGGHANDLING		HANDLING
	GODKÄND AV	TILLVERKNINGSRITNINGAR STÅL	ÄNDRING	FORMAT	A3
	SKAPAD AV	INNEHÅLL	2024-12-20	DATUM	1:5
PARTS			NUMMER	BET	
			P/20		