



PLACERING I STOMNÄT	
NUMMER	SYSTEMLINJE
P/21	7/C-D

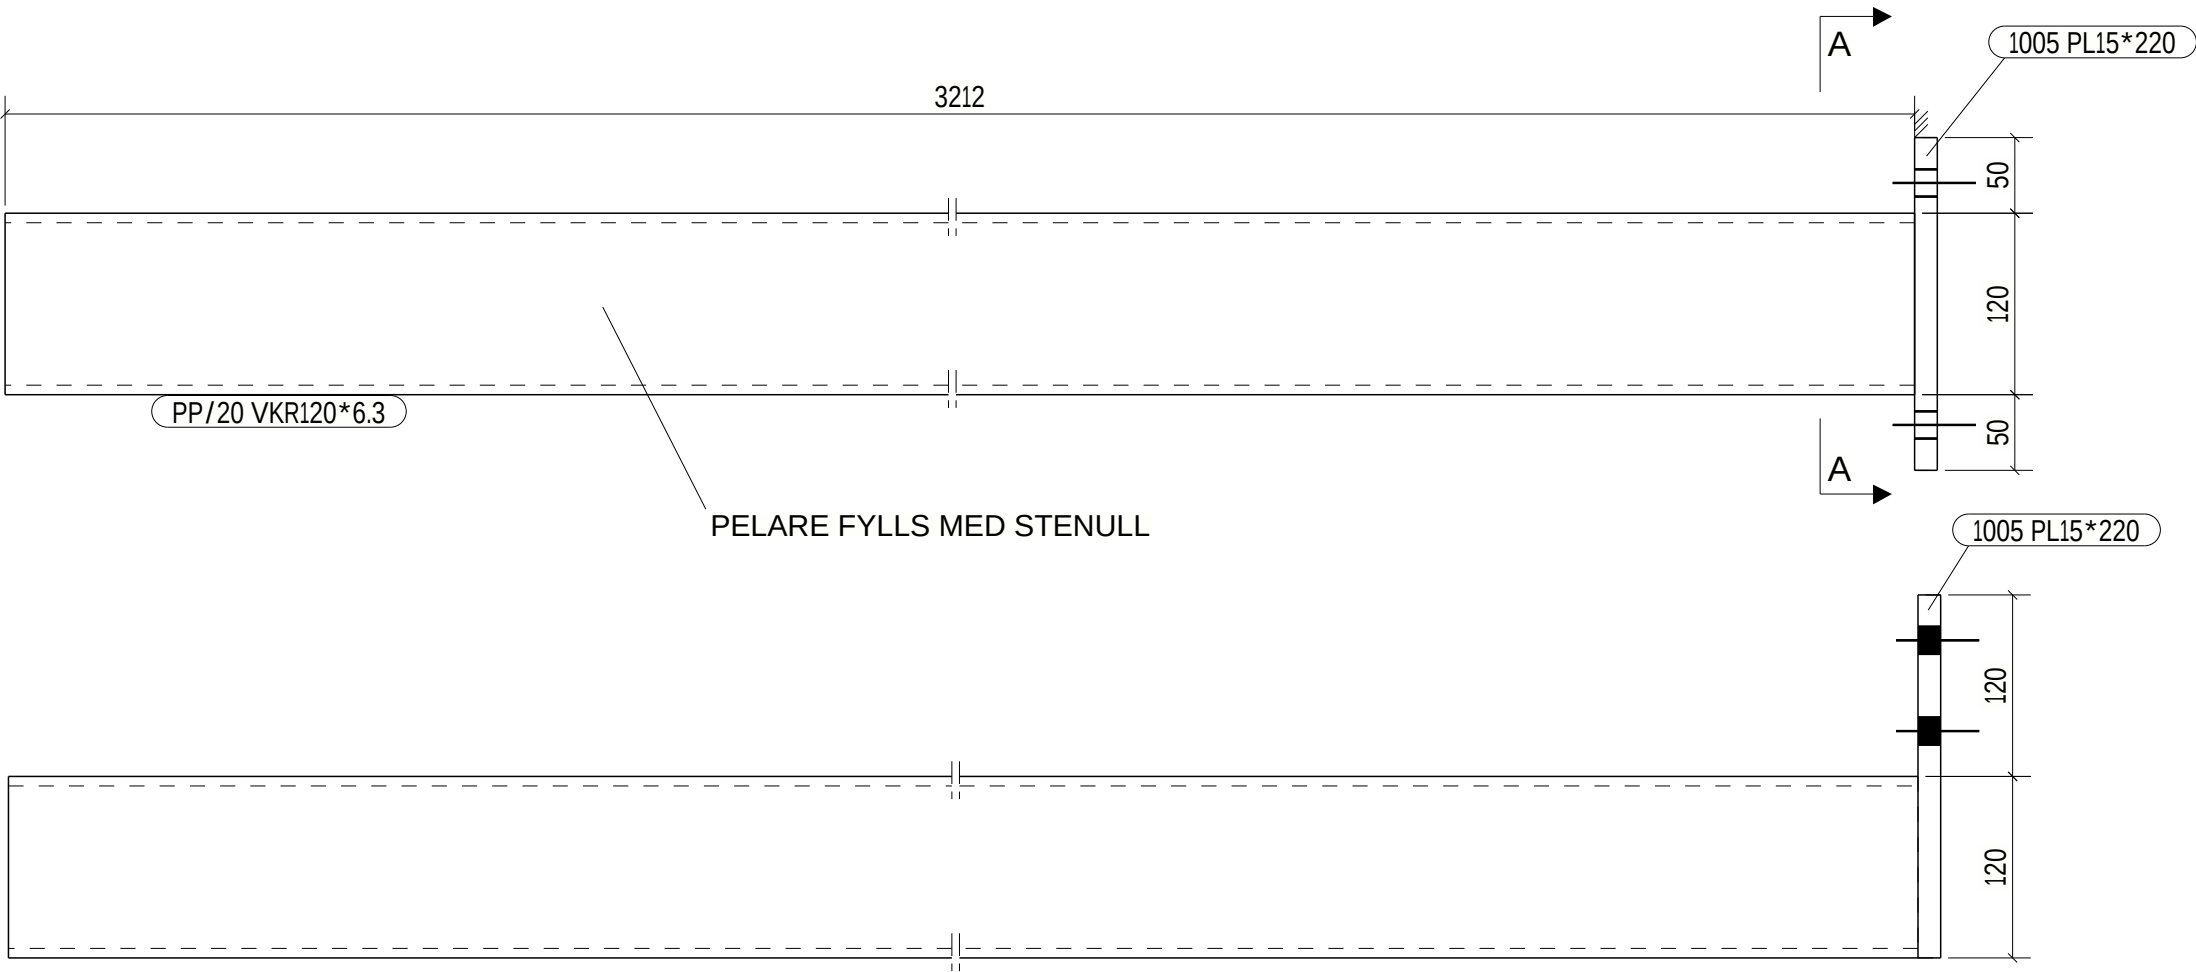

PELARE FYLLS MED STENULL

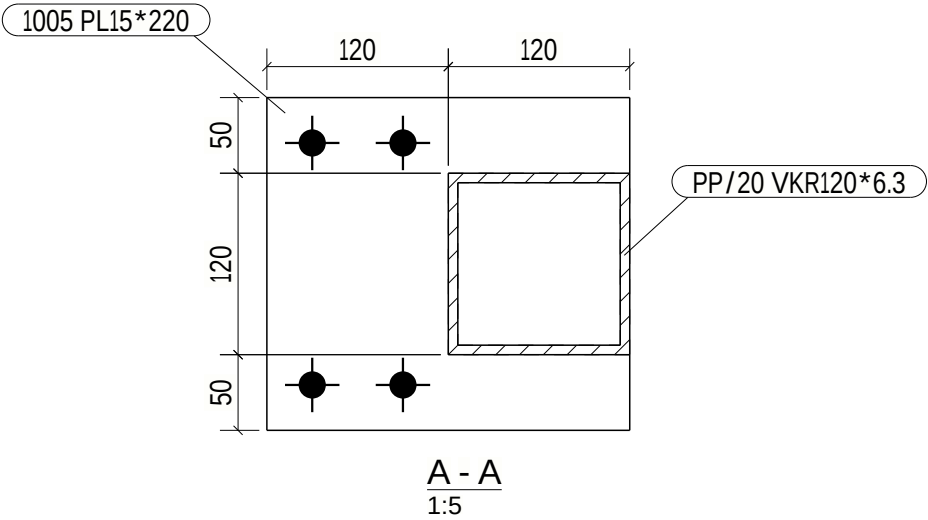

ALLMÄNNA NOTERINGAR: ALLA SVETSAR ÄR KÄLSVETS a5 OM EJ ANNAT ANGES

MATERIALLISTA FÖR ETT GODS MÄRKT: P/21 1 st. TILLVERKAS						
STYCKLIT.	PROFIL	MATERIAL	ANT.	LÄNGD	AREA/st	VIKT/st
PP/20	VKR120*6.3	S355J2H	1	3212	1.5	71.1
1005	PL15*220	S355J2	1	240	0.1	6.2
TOTALT					1.6	77.3

Norconsult	ANSVARIG PART	PROJEKT	FÖRFRÅGNINGSUNDERLAG		STATUS
	KONTAKTPERSON	CENTRALKÖK ROBERTSFORS KOMMUN	BYGGHANDLING		HANDLING
	GODKÄND AV	TILLVERKNINGSRITNINGAR STÅL	ÄNDRING	FORMAT	A3
	SKAPAD AV	INNEHÅLL	DATUM	SKALA	1:5
PARTS		NUMMER	2024-12-20	BET	P/21