

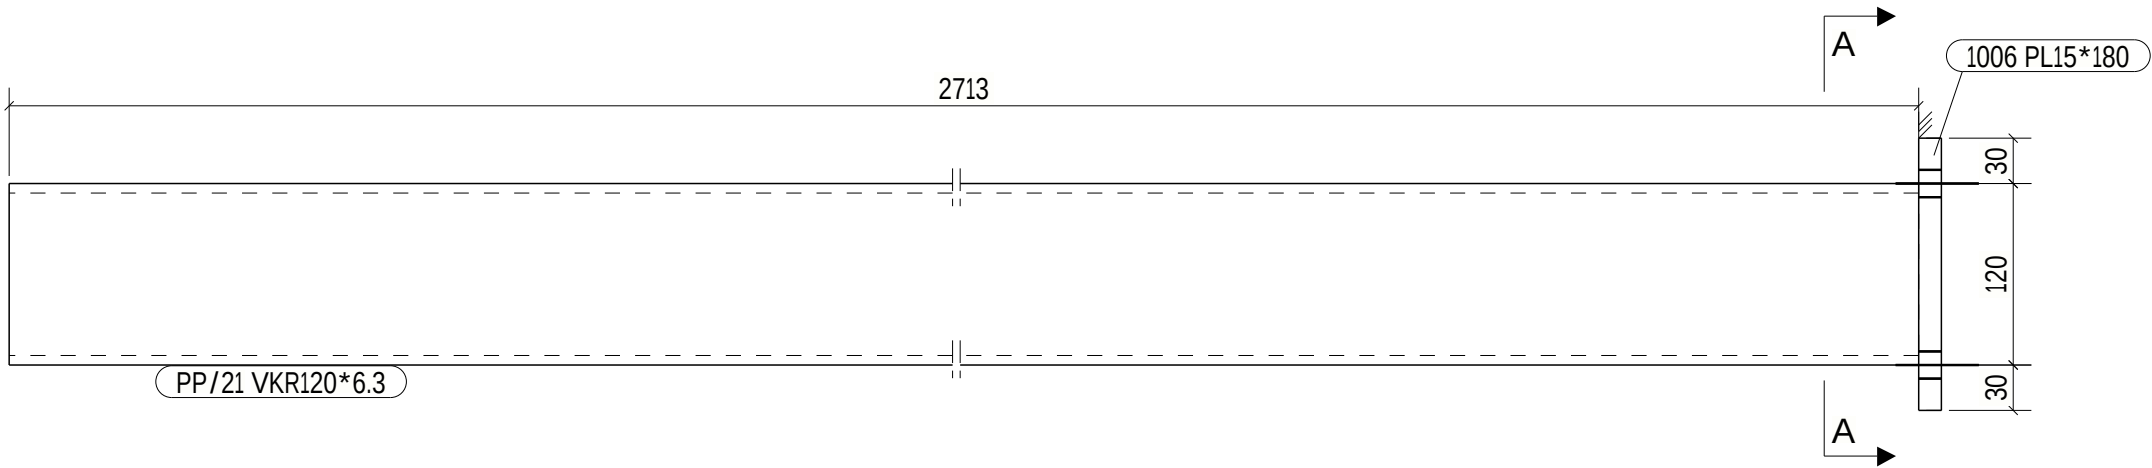


PLACERING I STOMNÄT	
NUMMER	SYSTEMLINJE
P/22	7/D-E

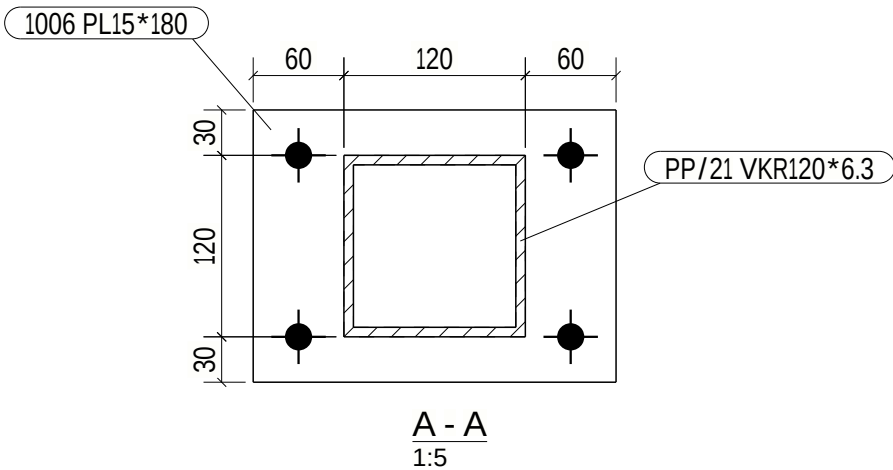

UTVÄNDIGT STÅL VARMFÖRZINKAS ENLIGT
ALLMÄNNA FÖRESKRIFTER K-01-0-001 -- 003

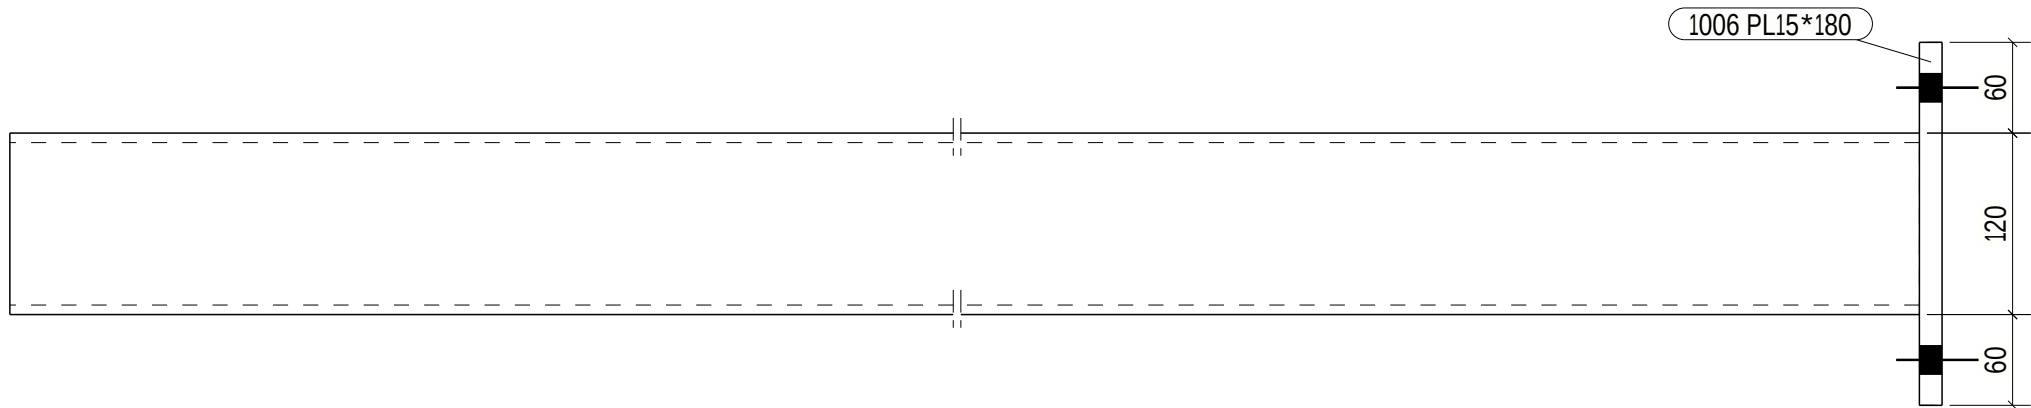

ALLMÄNNA NOTERINGAR: ALLA SVETSAR ÄR KÄLSVETS a5 OM EJ ANNAT ANGES

MATERIALLISTA FÖR ETT GODS MÄRKT: P/22						1 st. TILLVERKAS
STYCKLIT.	PROFIL	MATERIAL	ANT.	LÄNGD	AREA/st	VIKT/st
PP/21	VKR120*6.3	S355J2H	1	2713	1.2	60.1
1006	PL15*180	S355J2	1	240	0.1	5.1
TOTALT					1.3	65.1

Norconsult	ANSVARIG PART	PROJEKT	FÖRFRÅGNINGSUNDERLAG		STATUS
	KONTAKTPERSON	CENTRALEKÖK ROBERTSFORS KOMMUN	BYGGHANDLING		HANDLING
	GODKÄND AV	TILLVERKNINGSRITNINGAR STÅL	ÄNDRING		FORMAT
	SKAPAD AV	INNEHÅLL	2024-12-20		SKALA
PARTS		NUMMER	P/22		BET