
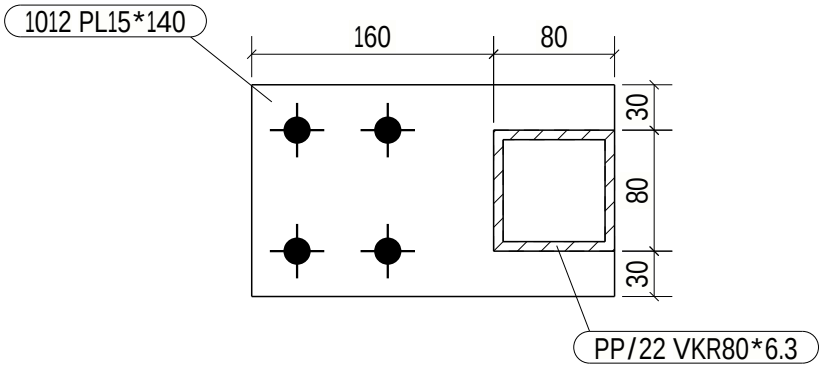
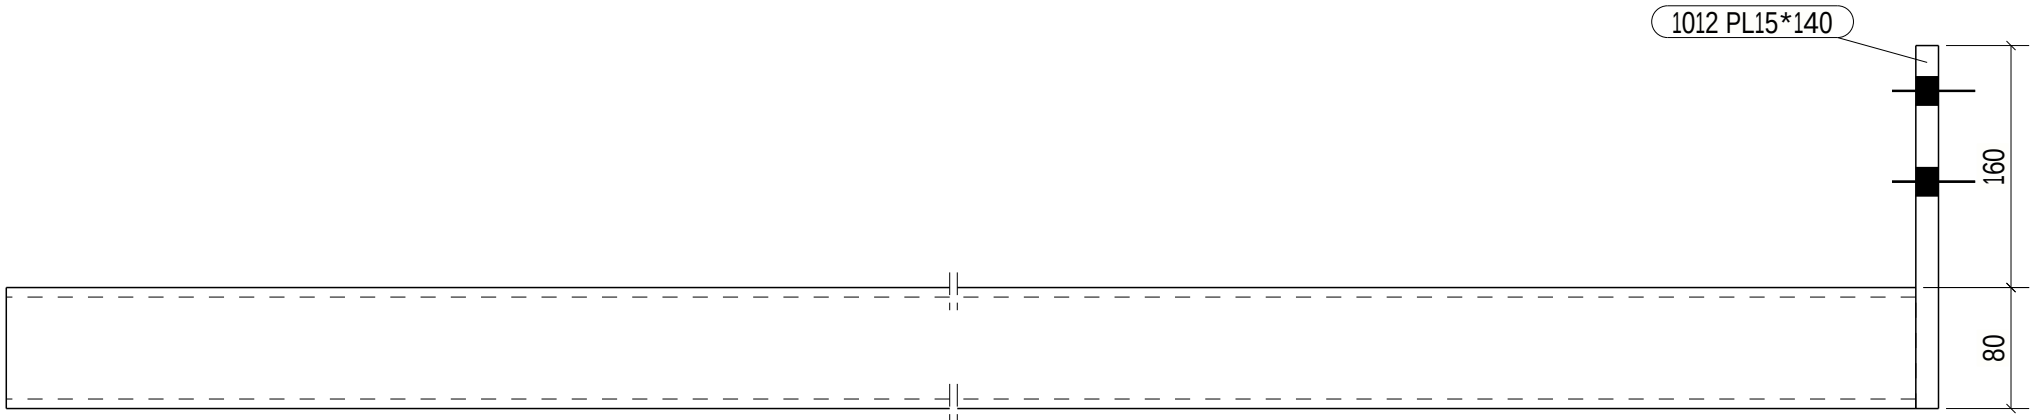


PLACERING I STOMNÄT	
NUMMER	SYSTEMLINJE
P/26	1/C-D
P/26	<1/C-D

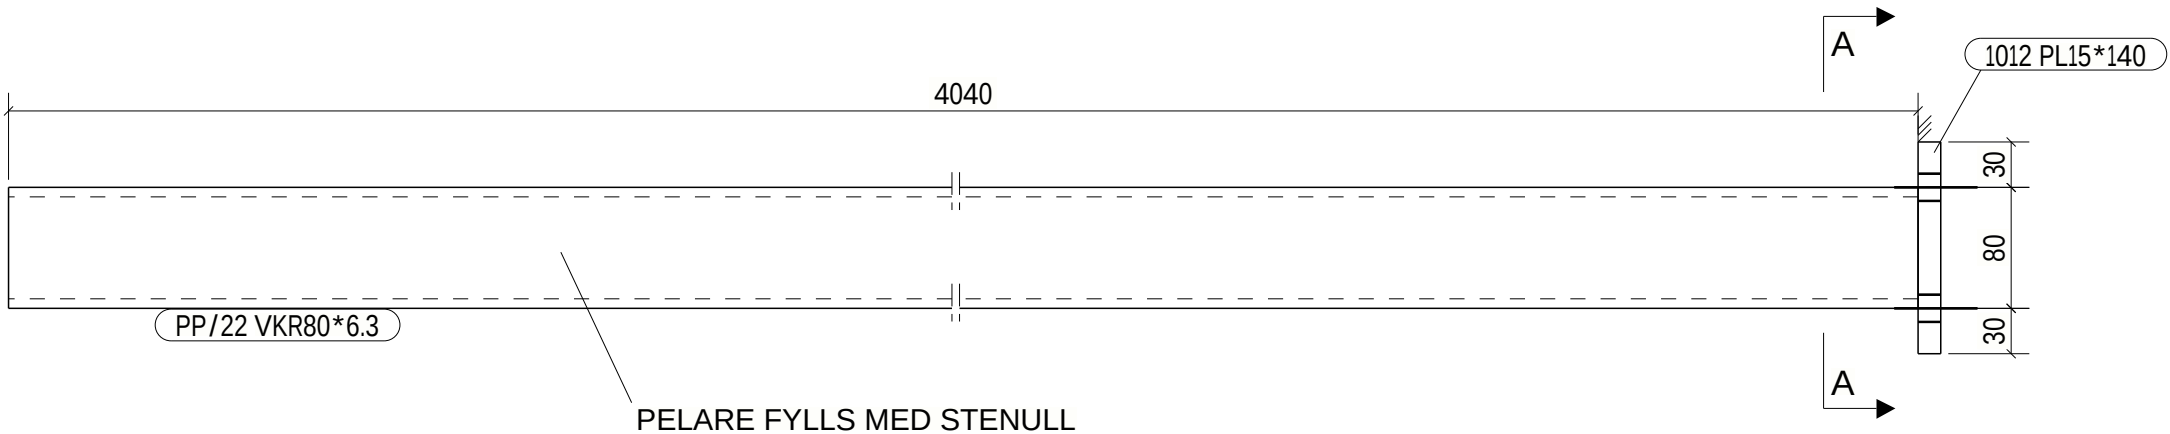

A - A
1:5

ALLMÄNNA NOTERINGAR: ALLA SVETSAR ÄR KÄLSVETS a5 OM EJ ANNAT ANGES

MATERIALLISTA FÖR ETT GODS MÄRKT: P/26 2 st. TILLVERKAS						
STYCKLIT.	PROFIL	MATERIAL	ANT.	LÄNGD	AREA/st	VIKT/st
PP/22	VKR80*6.3	S355J2H	1	4040	1.2	57.4
1012	PL15*140	S355J2	1	240	0.1	4.0
TOTALT					1.3	61.4

Norconsult	ANSVARIG PART	PROJEKT	FÖRFRÅGNINGSUNDERLAG		STATUS
	KONTAKTPERSON	CENTRALEKÖK ROBERTSFORS KOMMUN	BYGGHANDLING		HANDLING
	GODKÄND AV	TILLVERKNINGSRITNINGAR STÅL	ÄNDRING		FORMAT
	SKAPAD AV	INNEHÅLL	2024-12-20		SKALA
PARTS			NUMMER	1:5	BET
			P/26		