
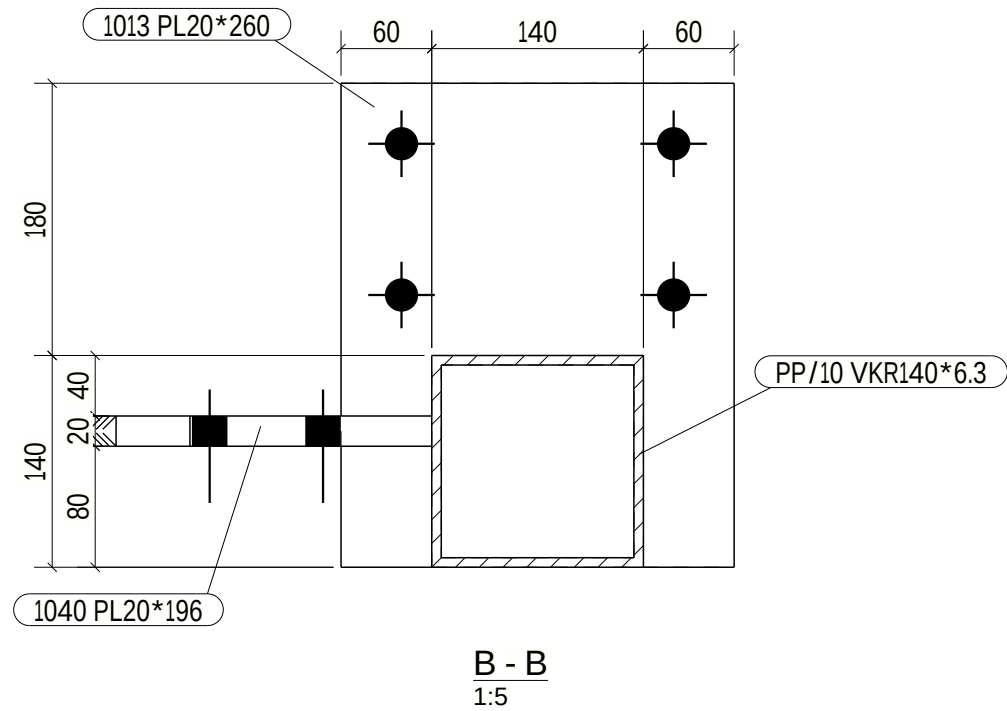
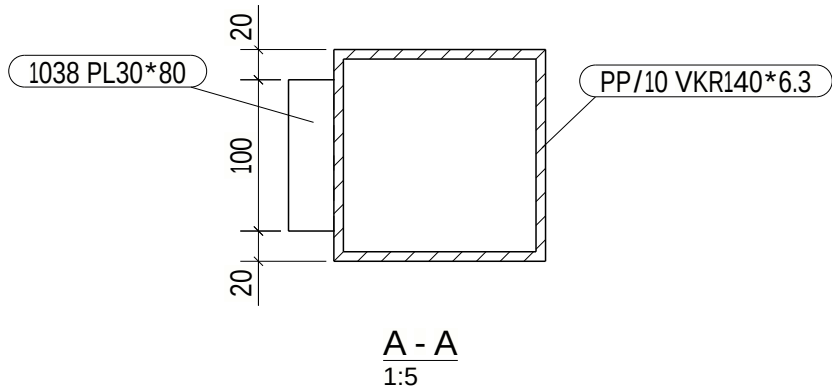


PLACERING I STOMNÄT	
NUMMER	SYSTEMLINJE
P/27	5/D

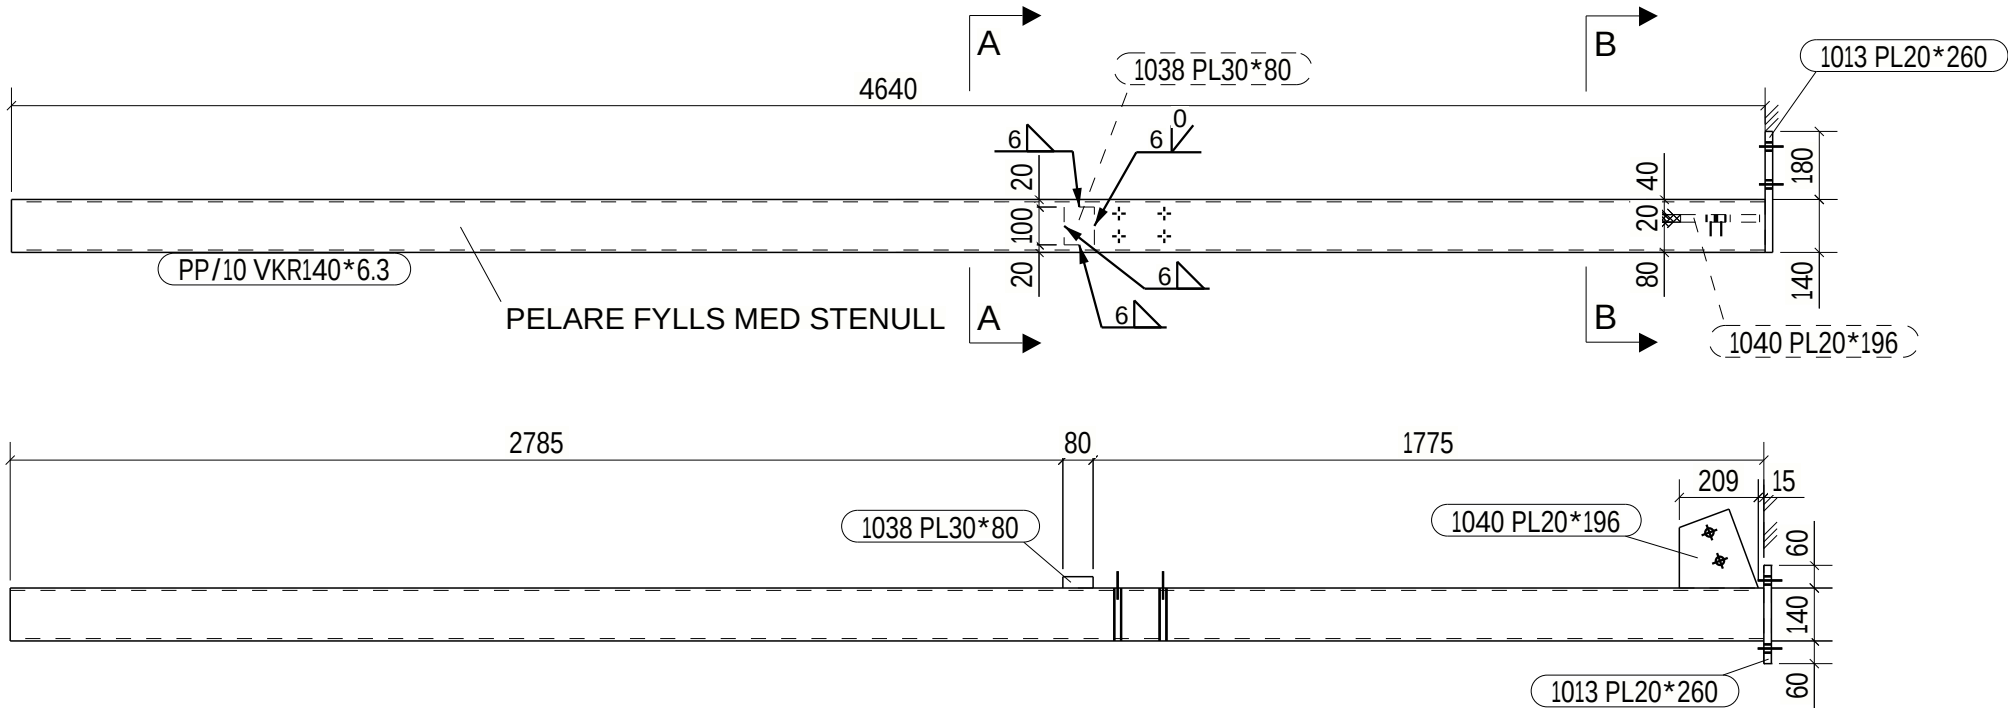

ALLMÄNNA NOTERINGAR: ALLA SVETSAR ÄR KÄLSVETS a5 OM EJ ANNAT ANGES

MATERIALLISTA FÖR ETT GODS MÄRKT: P/27 1 st. TILLVERKAS						
STYCKLIT.	PROFIL	MATERIAL	ANT.	LÄNGD	AREA/st	VIKT/st
PP/10	VKR140*6.3	S355J2H	1	4640	2.5	121.3
1013	PL20*260	S355J2	1	320	0.2	13.1
1040	PL20*196	S355J2	1	223	0.1	5.1
1038	PL30*80	S355J2	1	100	0.0	1.9
TOTALT					2.8	141.3

Norconsult	ANSVARIG PART	PROJEKT	FÖRFRÅGNINGSUNDERLAG		STATUS
	KONTAKTPERSON	CENTRALEKÖB ROBERTSFORS KOMMUN	BYGGHANDLING		HANDLING
	GODKÄND AV	TILLVERKNINGSRITNINGAR STÅL	ÄNDRING		FORMAT
	SKAPAD AV	INNEHÅLL	2024-12-20		SKALA
PARTS			NUMMER	1:20	BET
			P/27		