


PLACERING I STOMNÄT	
NUMMER	SYSTEMLINJE
P/28	5/B-C

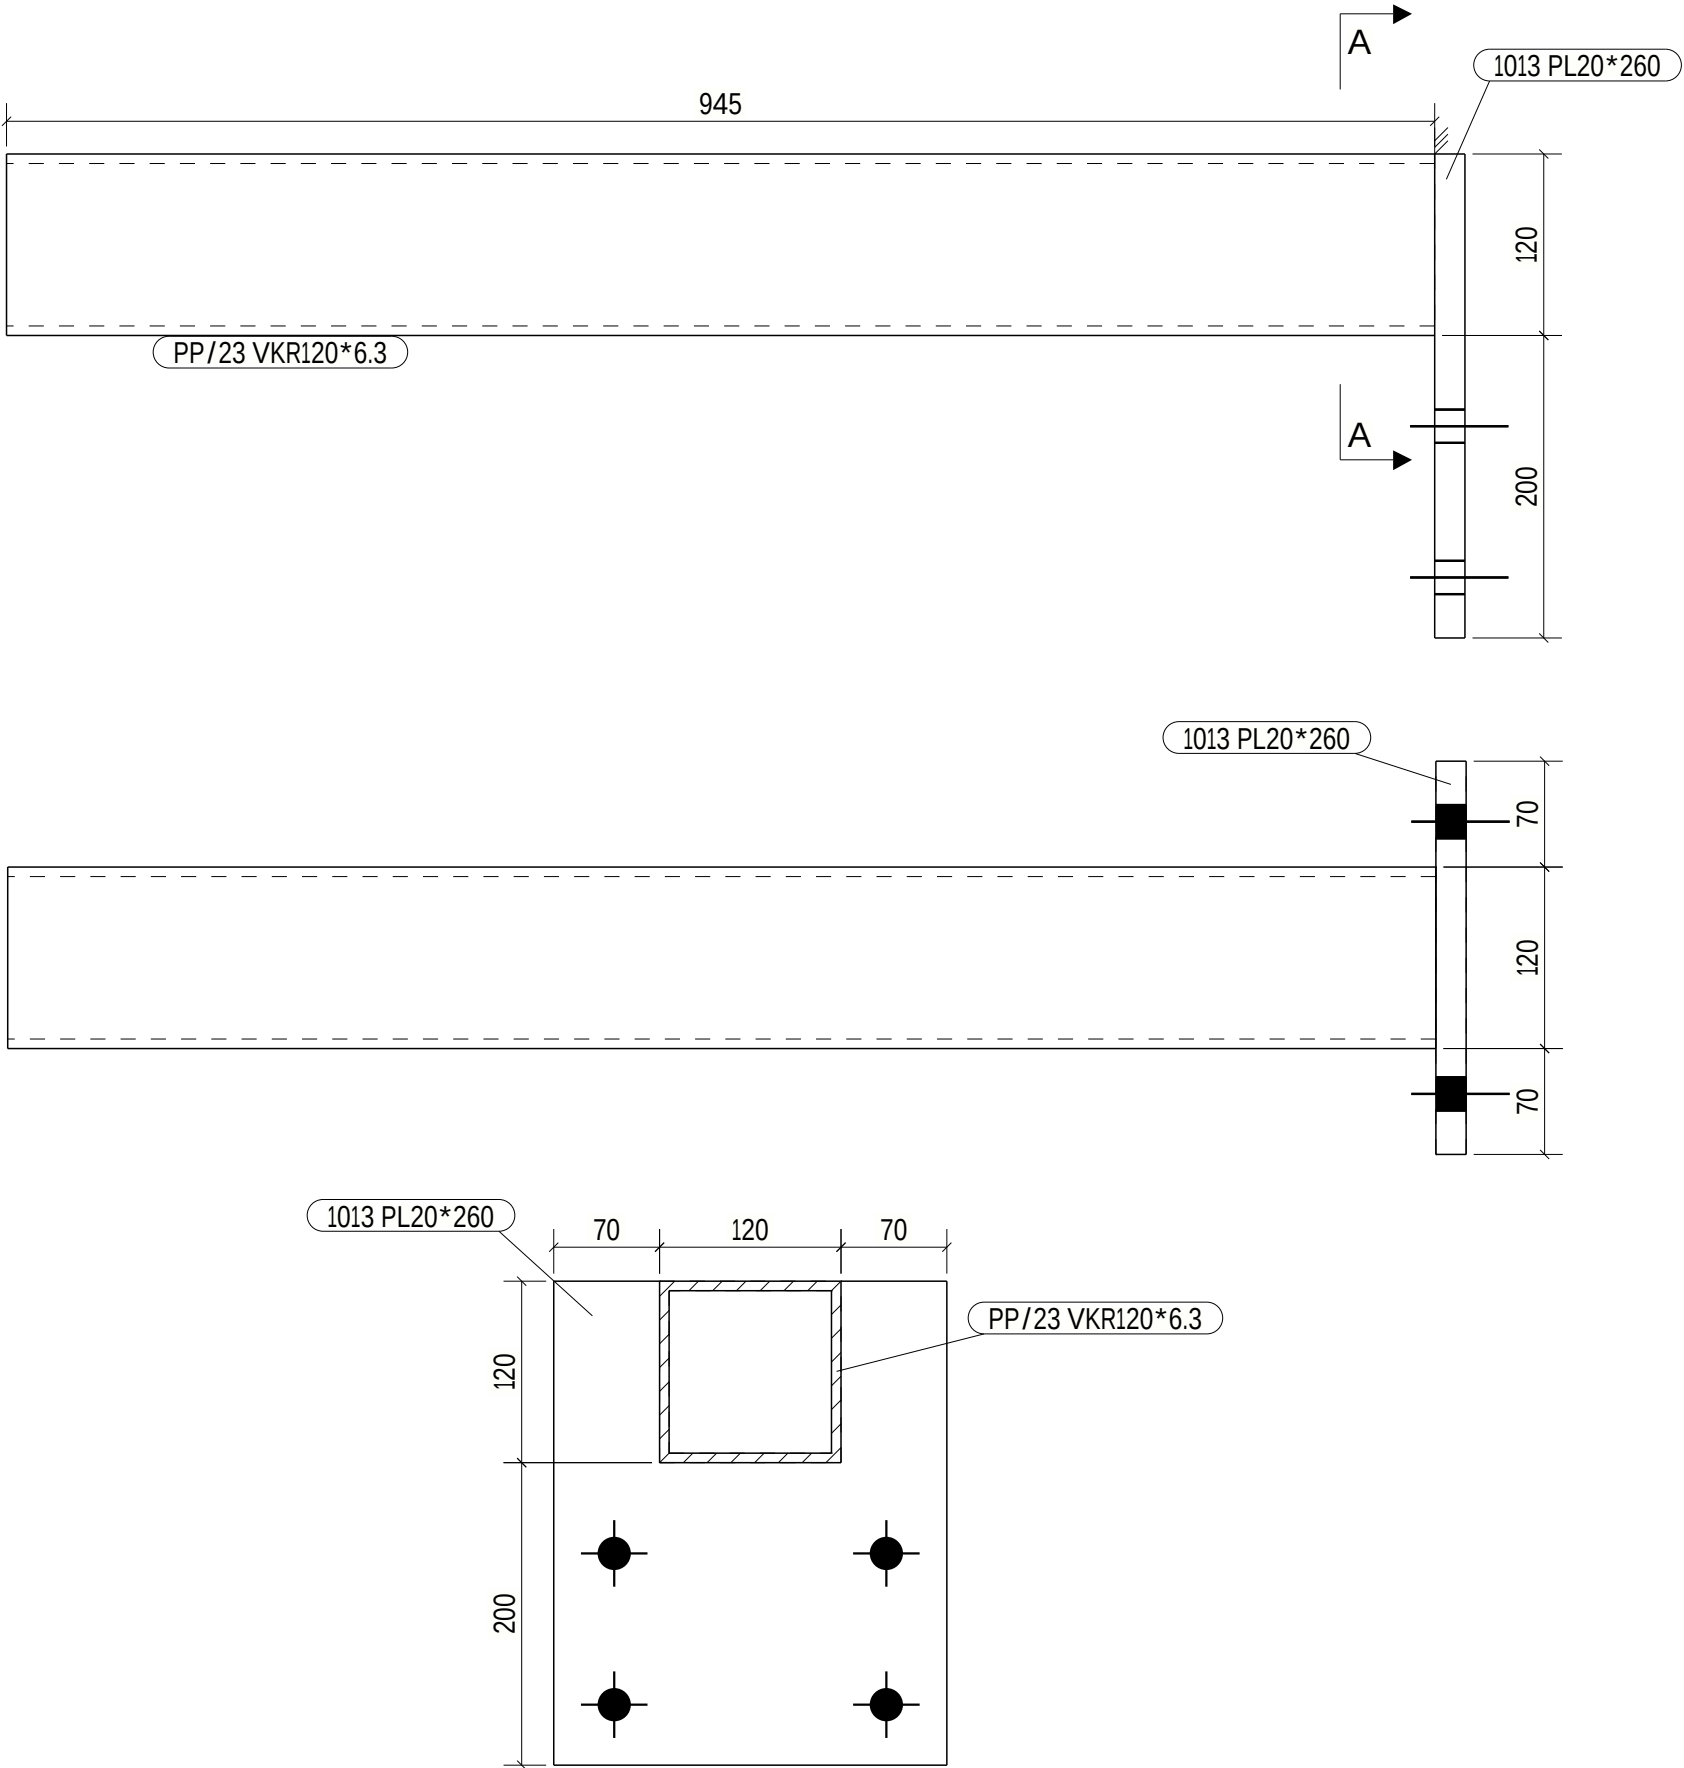

ALLMÄNNA NOTERINGAR: ALLA SVETSAR ÄR KÄLSVETS a5 OM EJ ANNAT ANGES						
MATERIALLISTA FÖR ETT GODS MÄRKT: P/28				1 st. TILLVERKAS		
STYCKLIT.	PROFIL	MATERIAL	ANT.	LÄNGD	AREA/st	VIKT/st
PP/23	VKR120*6.3	S355J2H	1	945	0.4	20.9
1013	PL20*260	S355J2	1	320	0.2	13.1
TOTALT					0.6	34.0

Norconsult	ANSVARIG PART	PROJEKT	FÖRFRÅGNINGSUNDERLAG		STATUS
	KONTAKTPERSON	CENTRALKÖK ROBERTSFORS KOMMUN	BYGGHANDLING		HANDLING
	GODKÄND AV	TILLVERKNINGSRITNINGAR STÅL	ÄNDRING	FORMAT	A3
	SKAPAD AV	INNEHÅLL	2024-12-20	DATUM	1:5
PARTS			NUMMER	BET	
			P/28		