
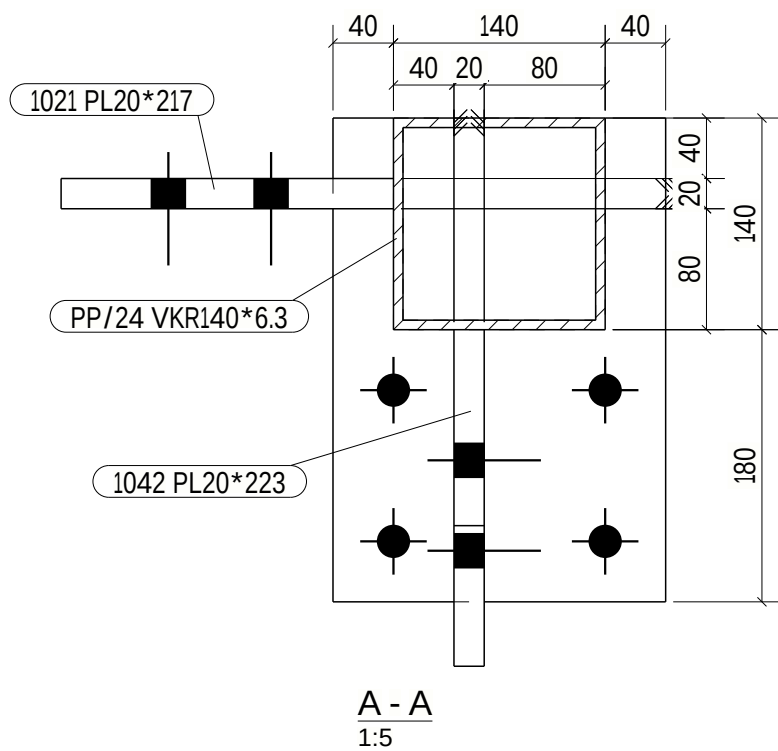


PLACERING I STOMNÄT	
NUMMER	SYSTEMLINJE
P/29	4/A

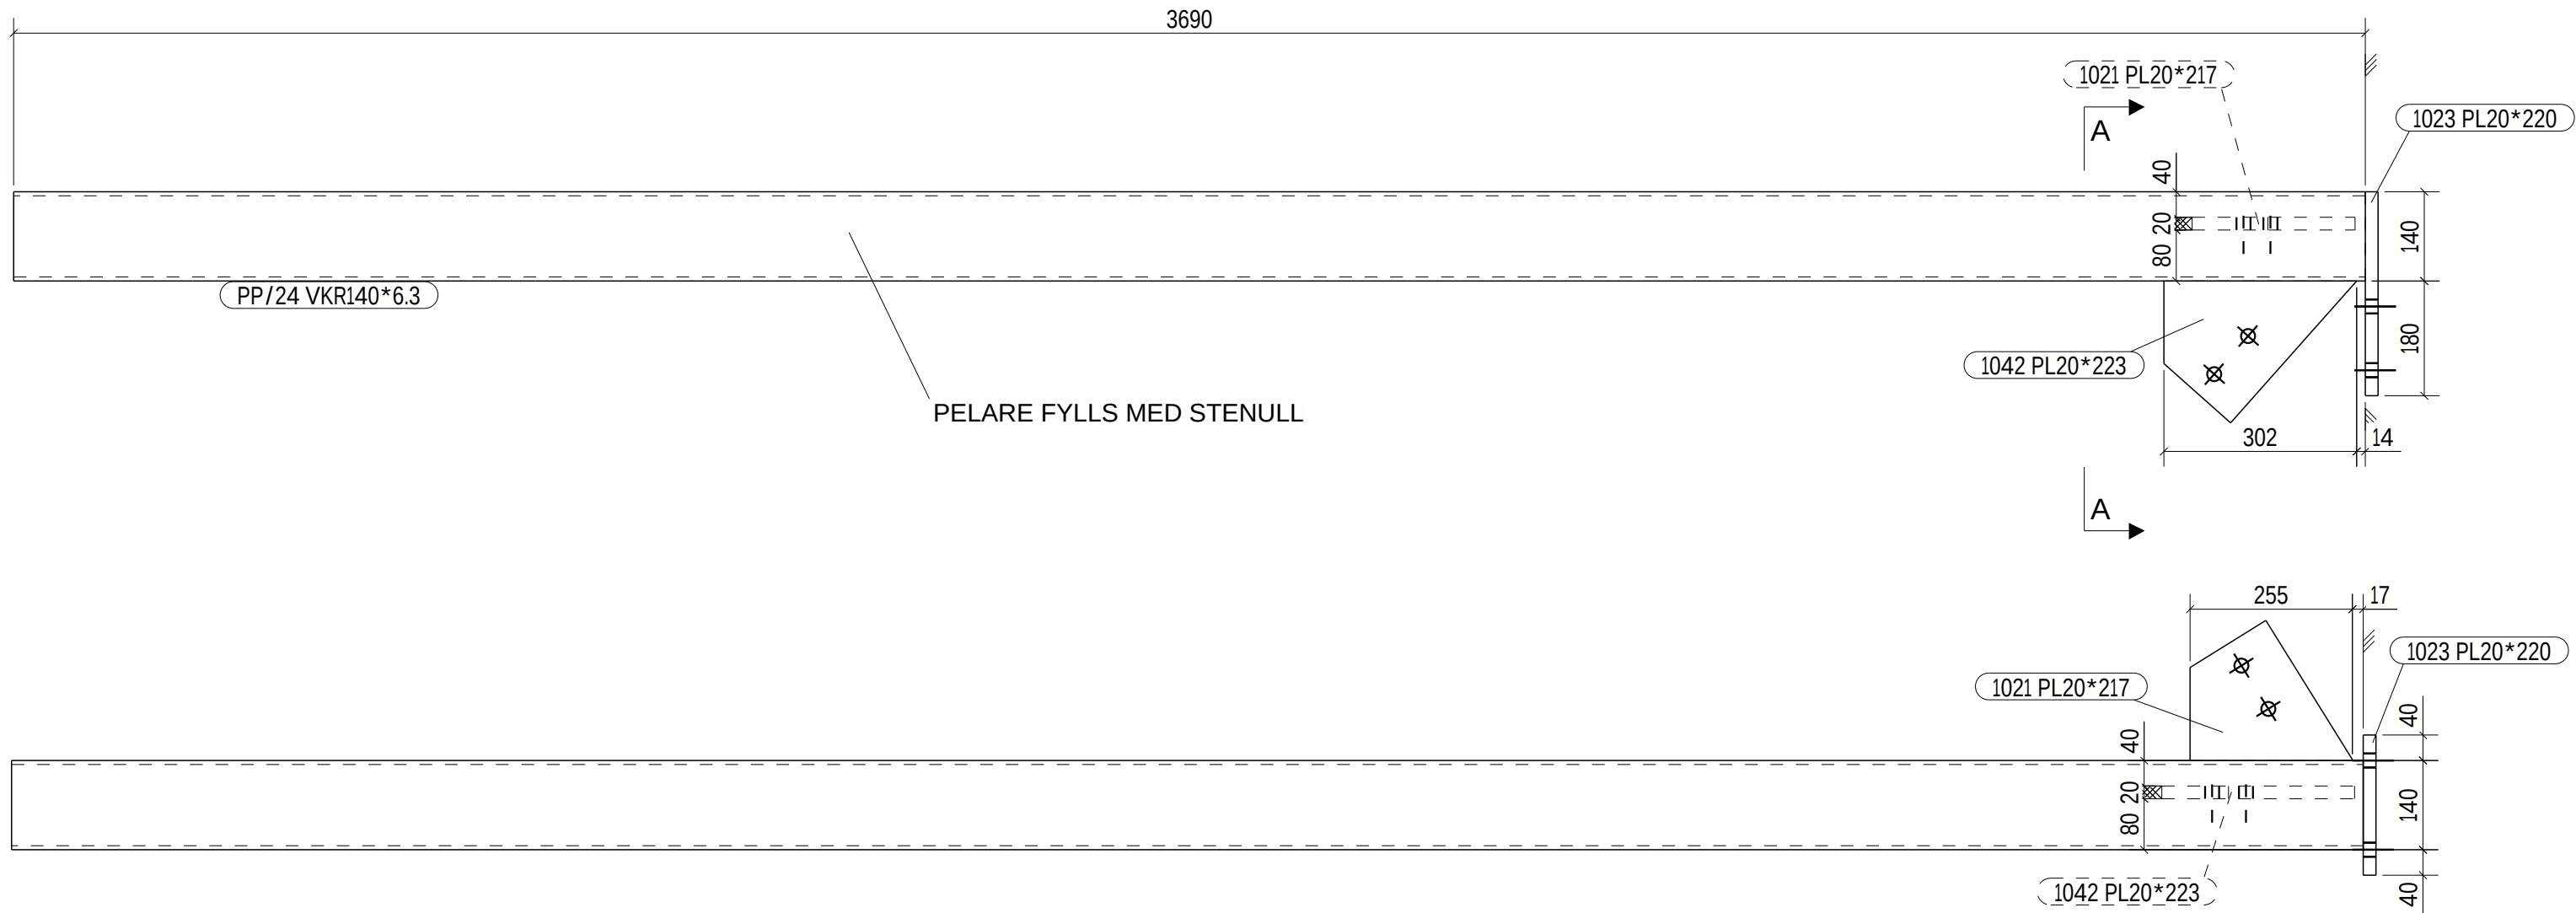

ALLMÄNNA NOTERINGAR:						
ALLA HÅL ÄR 22mm OM EJ ANNAT ANGES						
ALLA SVETSAR ÄR 6.5mm OM EJ ANNAT ANGES						
MATERIALLISTA FÖR ETT GODS MÄRKT: P/29 1 st. TILLVERKAS						
STYCKLIT.	PROFIL	MATERIAL	ANT.	LÄNGD	AREA/st	VIKT/st
PP/24	VKR140*6.3	S355J2H	1	3690	2.0	96.5
1023	PL20*220	S355J2	1	320	0.2	11.1
1042	PL20*223	S355J2	1	302	0.1	6.3
1021	PL20*217	S355J2	1	259	0.1	5.8
TOTALT					2.3	119.6

Norconsult	ANSVARS PART	PROJEKT	FÖRFRÅGNINGSUNDERLAG		STATUS
	KONTAKTPERSON	CENTRALEKÖB ROBERTSFORS KOMMUN	BYGGHANDLING		HANDLING
	GODKÄND AV	TILLVERKNINGSRITNINGAR STÅL	ÄNDRING		FORMAT
	SKAPAD AV	ARVID WENNBERG	2024-12-20		SKALA
PARTS			P/29		BET