
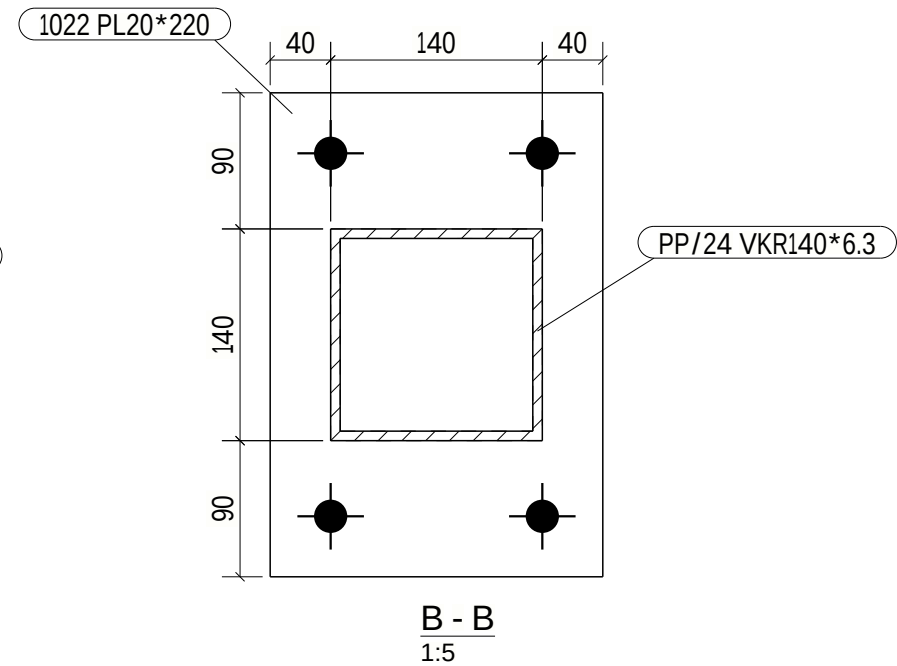
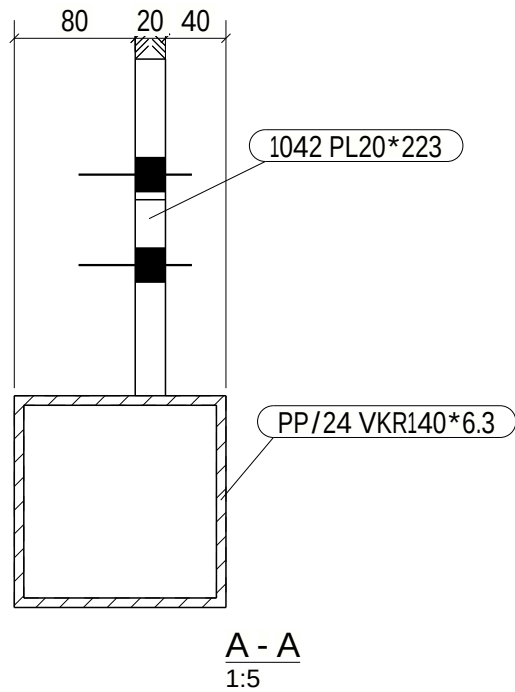
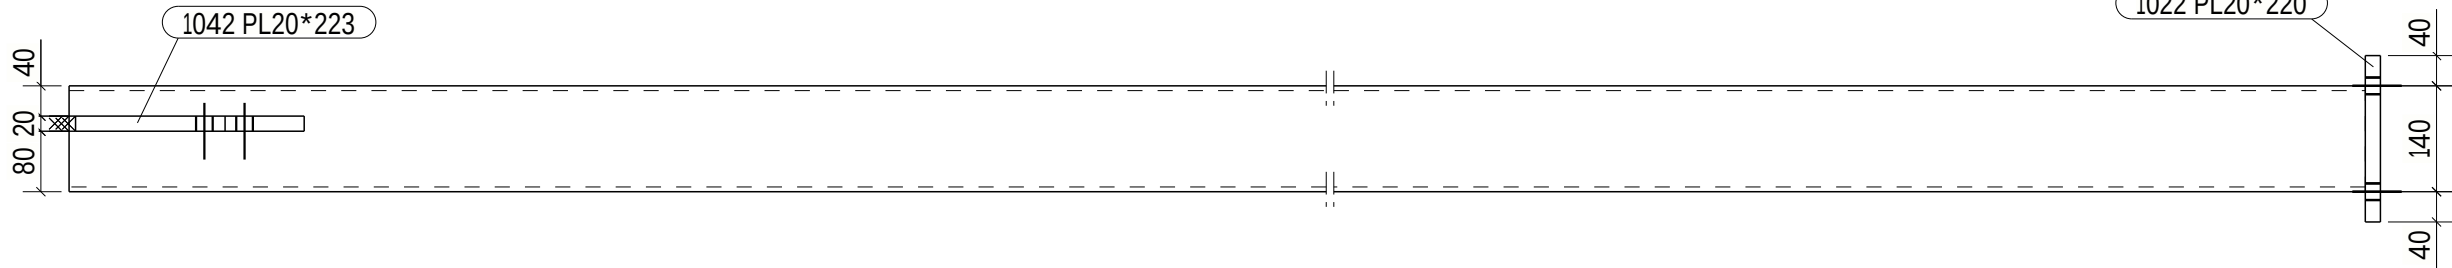


PLACERING I STOMNÄT	
NUMMER	SYSTEMLINJE
P/30	4/A-B

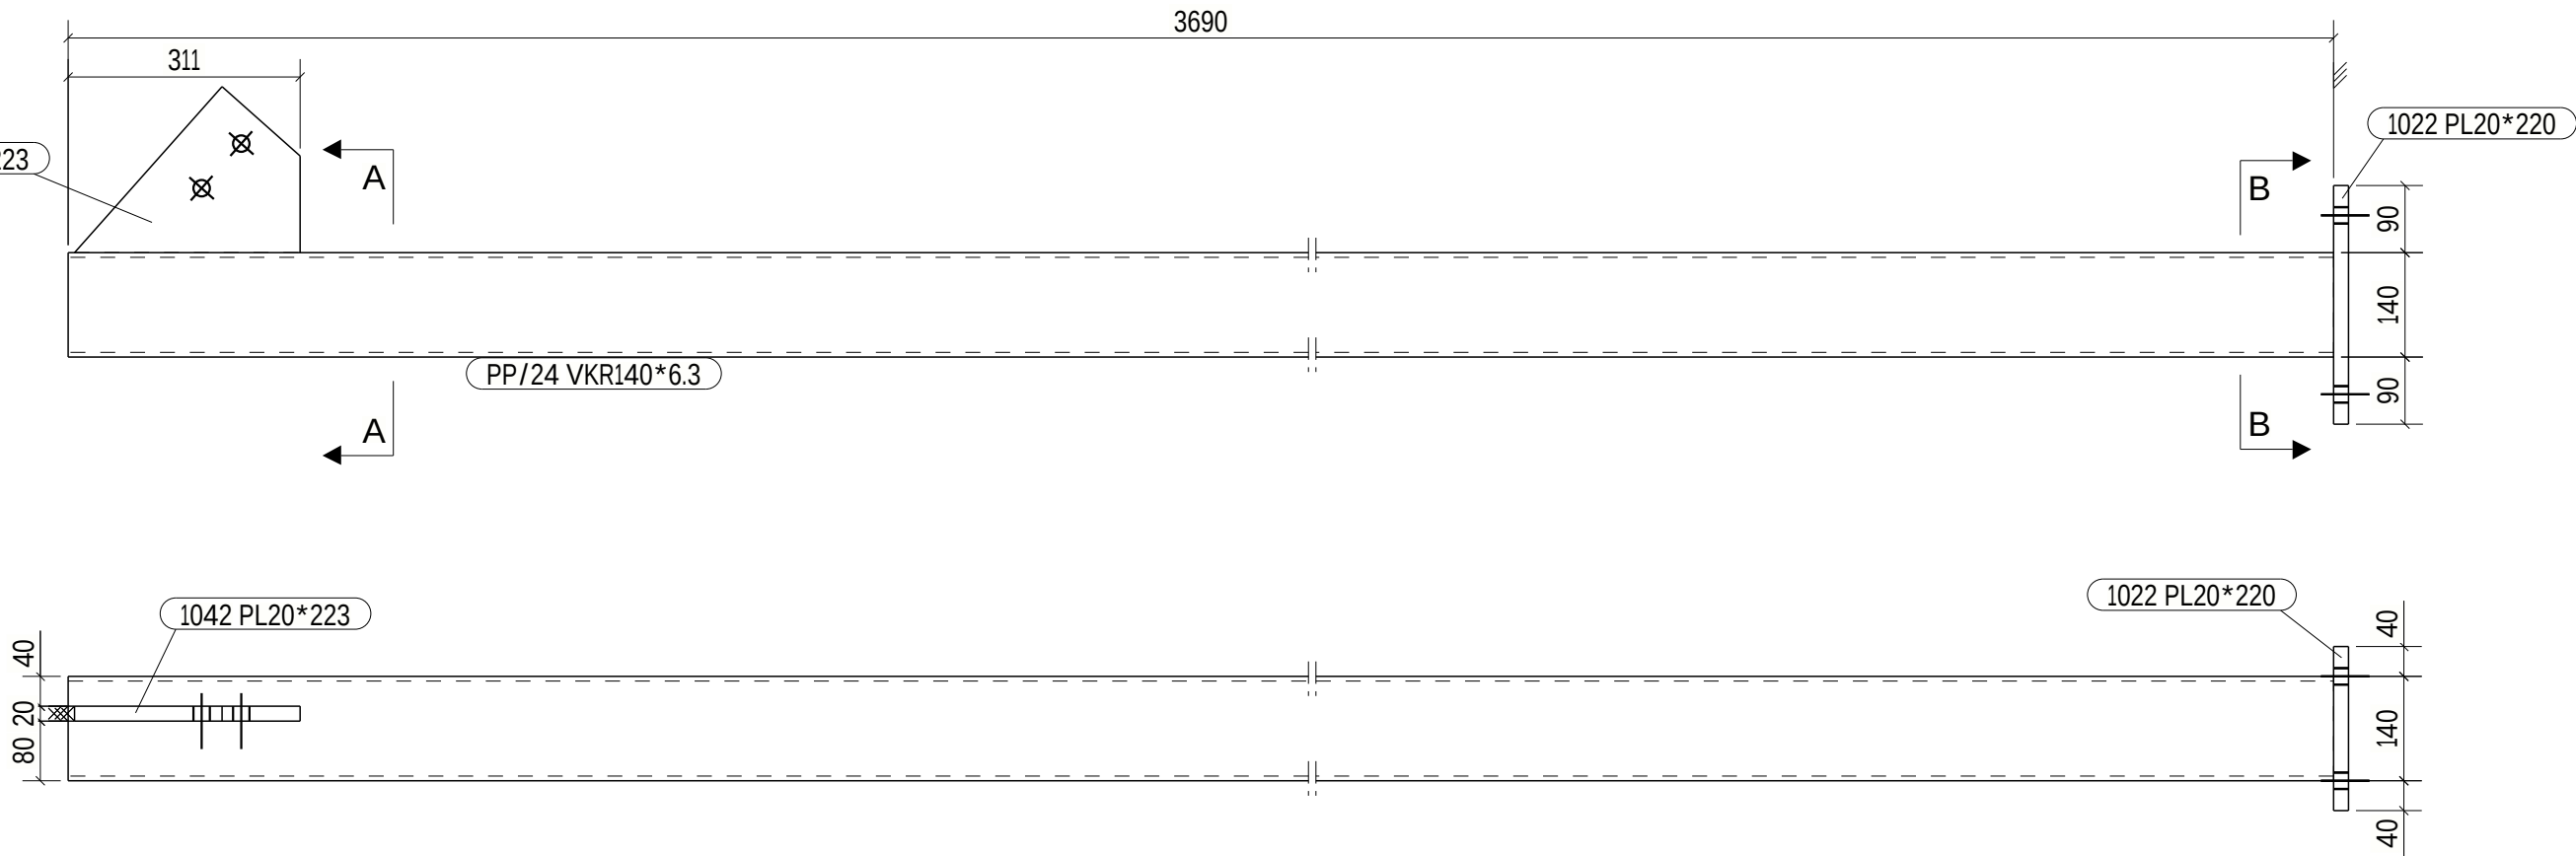

ALLMÄNNA NOTERINGAR: ALLA SVETSAR ÄR KÄLSVETS a5 OM EJ ANNAT ANGES

MATERIALLISTA FÖR ETT GODS MÄRKT: P/30						1 st. TILLVERKAS
STYCKLIT.	PROFIL	MATERIAL	ANT.	LÄNGD	AREA/st	VIKT/st
PP/24	VKR140*6.3	S355J2H	1	3690	2.0	96.5
1022	PL20*220	S355J2	1	320	0.2	11.1
1042	PL20*223	S355J2	1	302	0.1	6.3
TOTALT					2.3	113.9

Norconsult 	ANSVARIG PART	PROJEKT	FÖRFRÅGNINGSUNDERLAG		STATUS
	KONTAKTPERSON	CENTRALEKÖB ROBERTSFORS KOMMUN	BYGGHANDLING		HANDLING
	GODKÄND AV	TILLVERKNINGSRITNINGAR STÅL	ÄNDRING		FORMAT
	SKAPAD AV	INNEHÅLL	2024-12-20		SKALA
PARTS		NUMMER	P/30		BET