
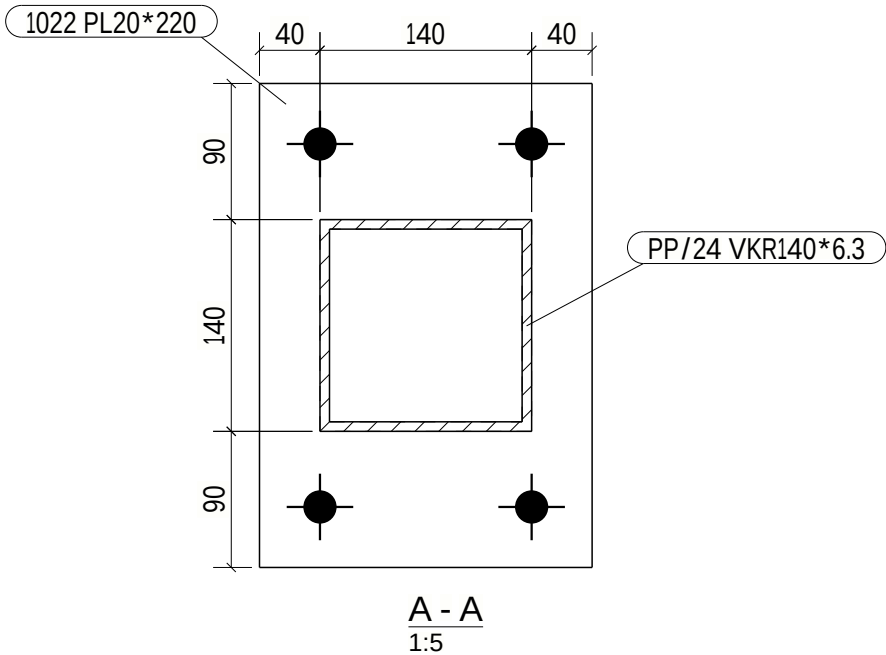


PLACERING I STOMNÄT	
NUMMER	SYSTEMLINJE
P/31	4/A-B
P/31	4/B

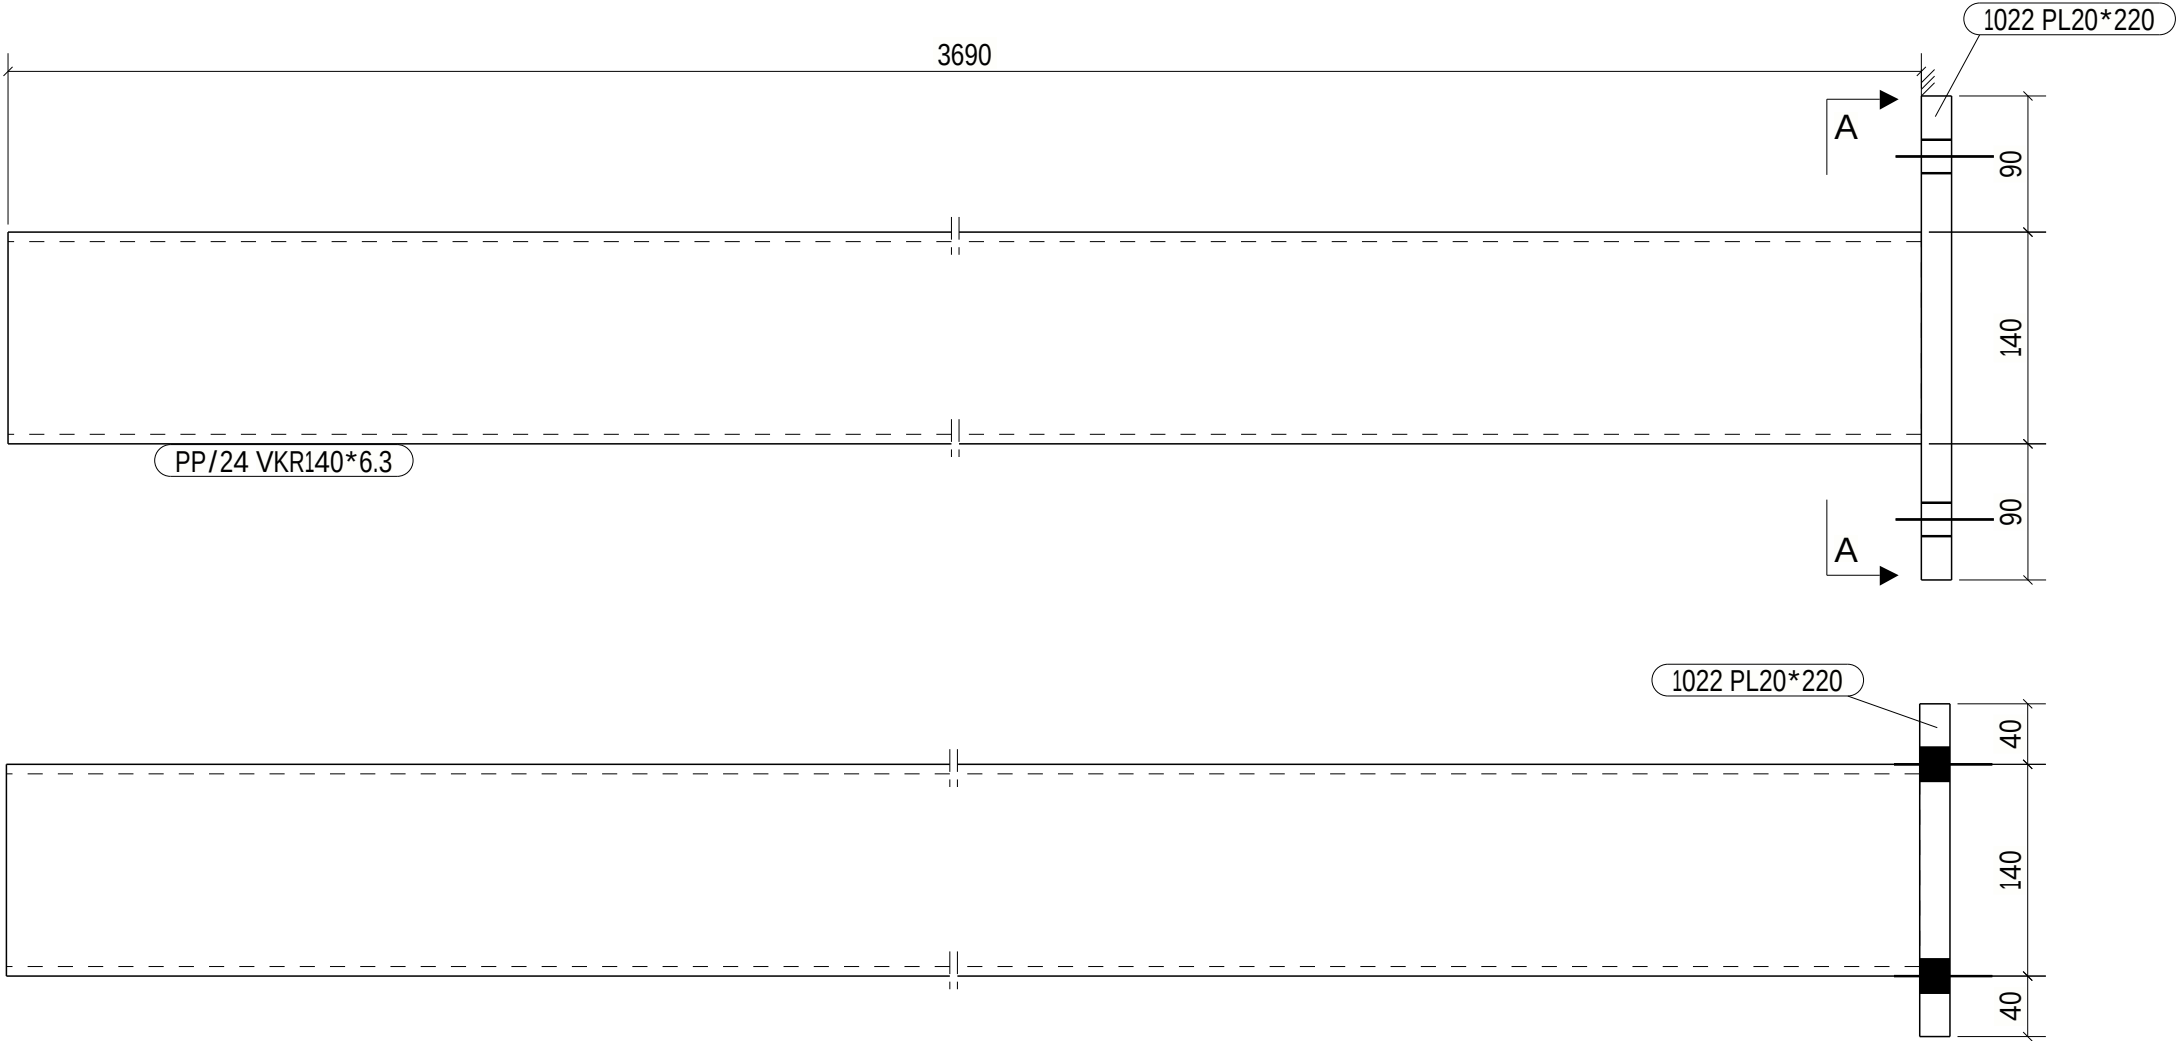

ALLMÄNNA NOTERINGAR: ALLA SVETSAR ÄR KÄLSVETS a5 OM EJ ANNAT ANGES

MATERIALLISTA FÖR ETT GODS MÄRKT: P/31 2 st. TILLVERKAS						
STYCKLIT.	PROFIL	MATERIAL	ANT.	LÄNGD	AREA/st	VIKT/st
PP/24	VKR140*6.3	S355J2H	1	3690	2.0	96.5
1022	PL20*220	S355J2	1	320	0.2	11.1
TOTALT					2.2	107.5

Norconsult	ANSVARIG PART	PROJEKT		STATUS	
	KONTAKTPERSON	CENTRALKÖK ROBERTSFORS KOMMUN		FÖRFRÅGNINGSUNDERLAG	
	GODKÄND AV	TILLVERKNINGSRITNINGAR STÅL		BYGGHANDLING	
	SKAPAD AV	INNEHÅLL		HANDLING	
BJÖRN LIDSTRÖM		2024-12-20		ÄNDRING	FORMAT
BJÖRN LIDSTRÖM		1:5		DATUM	SKALA
ARVID WENNERBERG		P/31		NUMMER	BET
PARTS					