
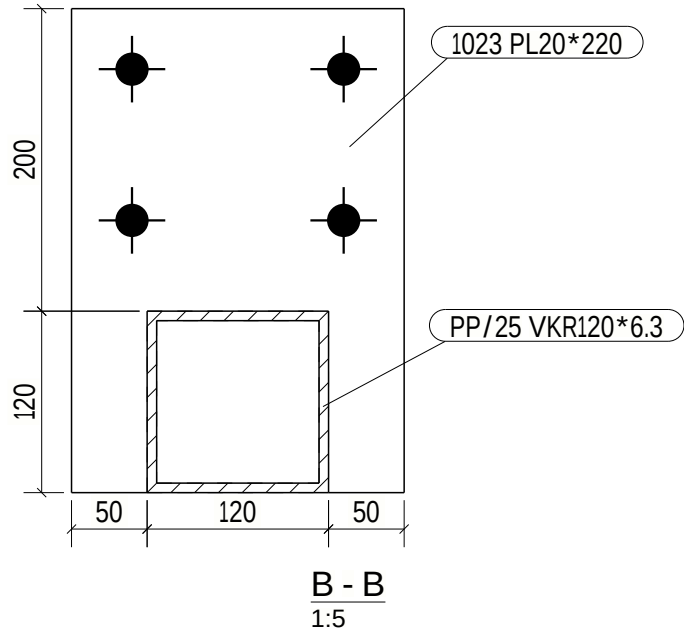
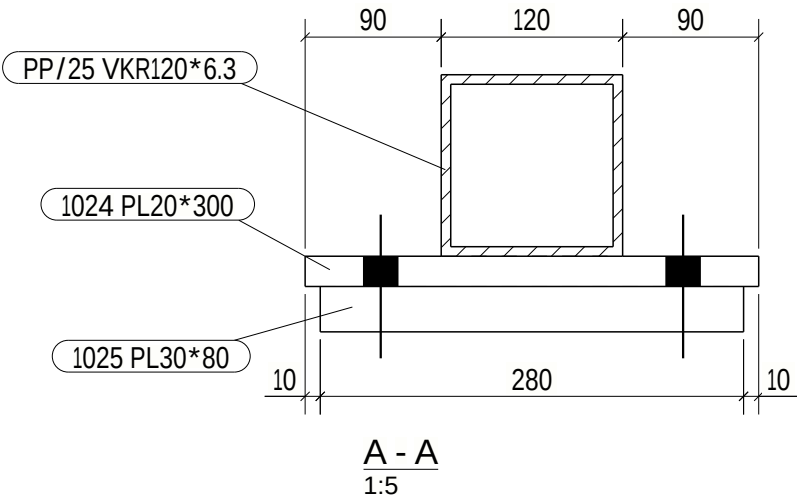


| PLACERING I STOMNÄT |             |
|---------------------|-------------|
| NUMMER              | SYSTEMLINJE |
| P/32                | 4/B-C       |

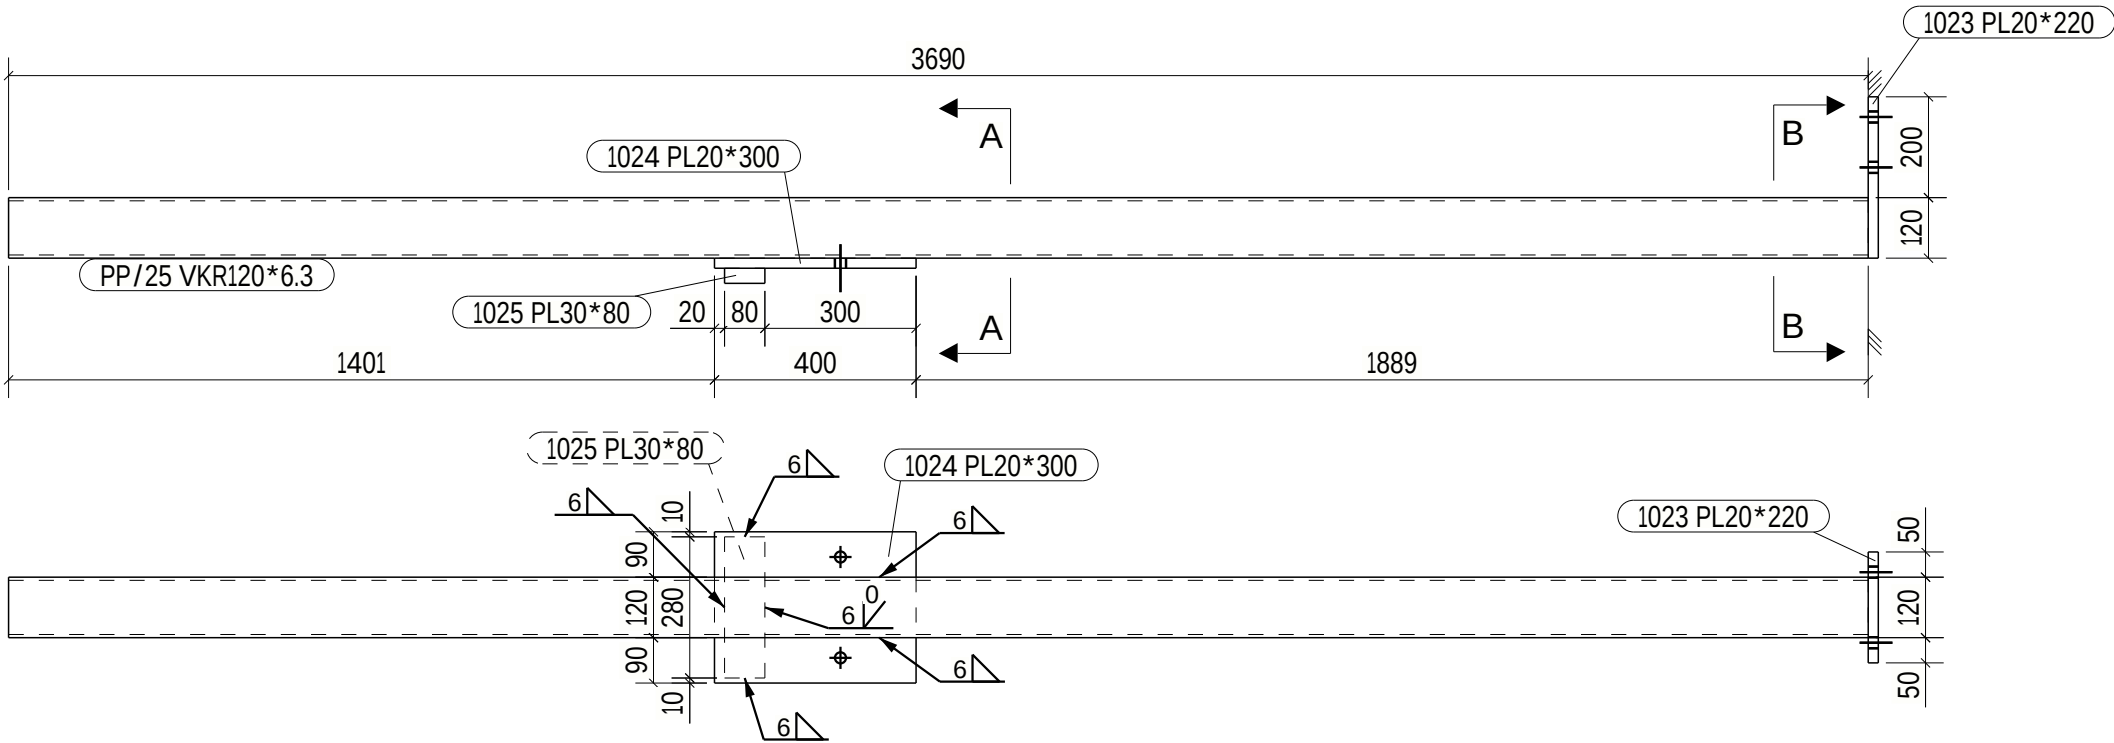

ALLMÄNNA NOTERINGAR: ALLA SVETSAR ÄR KÄLSVETS a5 OM EJ ANNAT ANGES

| MATERIALLISTA FÖR ETT GODS MÄRKT: P/32 1 st. TILLVERKAS |            |          |      |       |         |         |
|---------------------------------------------------------|------------|----------|------|-------|---------|---------|
| STYCKLIT.                                               | PROFIL     | MATERIAL | ANT. | LÄNGD | AREA/st | VIKT/st |
| PP/25                                                   | VKR120*6.3 | S355J2H  | 1    | 3690  | 1.7     | 81.7    |
| 1024                                                    | PL20*300   | S355J2   | 1    | 400   | 0.3     | 18.8    |
| 1023                                                    | PL20*220   | S355J2   | 1    | 320   | 0.2     | 11.1    |
| 1025                                                    | PL30*80    | S355J2   | 1    | 280   | 0.1     | 5.3     |
| TOTALT                                                  |            |          |      |       | 2.2     | 116.9   |

|            |               |                               |                      |      |          |
|------------|---------------|-------------------------------|----------------------|------|----------|
| Norconsult | ANSVARIG PART | PROJEKT                       | FÖRFRÅGNINGSUNDERLAG |      | STATUS   |
|            | KONTAKTPERSON | CENTRALEKÖ ROBERTSFORS KOMMUN | BYGGHANDLING         |      | HANDLING |
|            | GODKÄND AV    | TILLVERKNINGSRITNINGAR STÅL   | ÄNDRING              |      | FORMAT   |
|            | SKAPAD AV     | INNEHÅLL                      | 2024-12-20           |      | SKALA    |
| PARTS      |               |                               | NUMMER               | P/32 | BET      |