


Norconsult		ANSVARIG PART	CENTRALKÖK ROBERTSFORS KOMMUN		PROJEKT	FÖRFRÅGNINGSUNDERLAG		STATUS
BJÖRN LIDSTRÖM		KONTAKTPERSON	TILLVERKNINGSRITNINGAR STÅL		RITNINGSKATEGORI	BYGGHANDLING		HANDLING
BJÖRN LIDSTRÖM		GODKÄND AV	PARTS		INNEHÅLL	ÄNDRING	A3	FORMAT
ARVID WENNERBERG		SKAPAD AV			DATUM	2024-12-20	SKALA	1:15
						NUMMER	P/33	BET

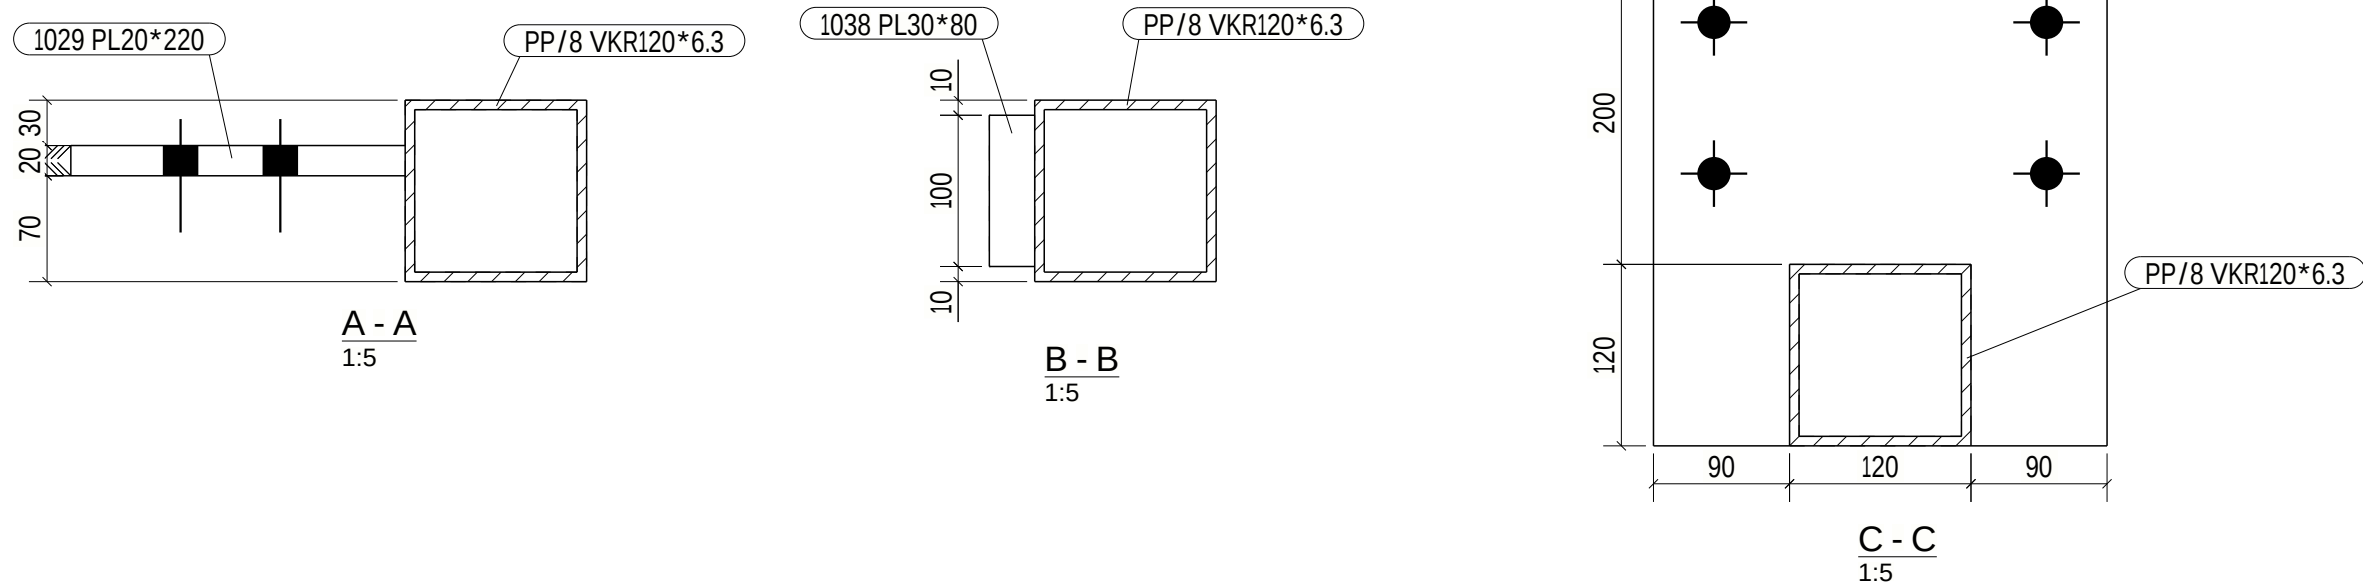

MATERIALLISTA FÖR ETT GODS MÄRKT: P/33 1 st. TILLVERKAS

STYCKLIT.	PROFIL	MATERIAL	ANT.	LÄNGD	AREA/st	VIKT/st
PP/8	VKR120*6.3	S355J2H	1	5186	2.4	114.8
1041	PL20*300	S355J2	1	320	0.2	15.1
1029	PL20*220	S355J2	1	268	0.1	5.9
1038	PL30*80	S355J2	1	100	0.0	1.9
TOTALT					2.7	137.7