
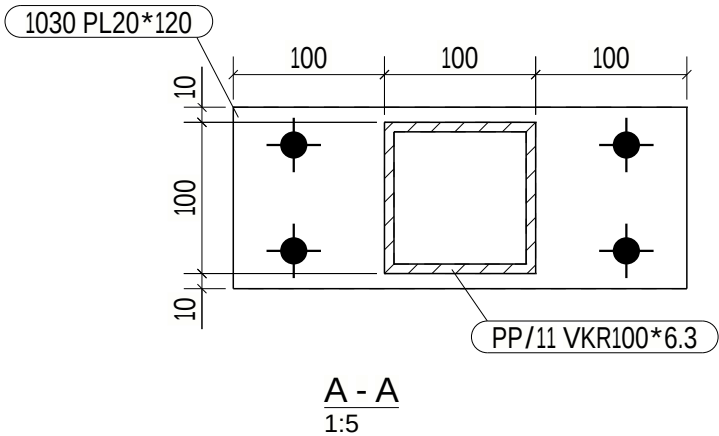


PLACERING I STOMNÄT	
NUMMER	SYSTEMLINJE
P/34	4-5/D

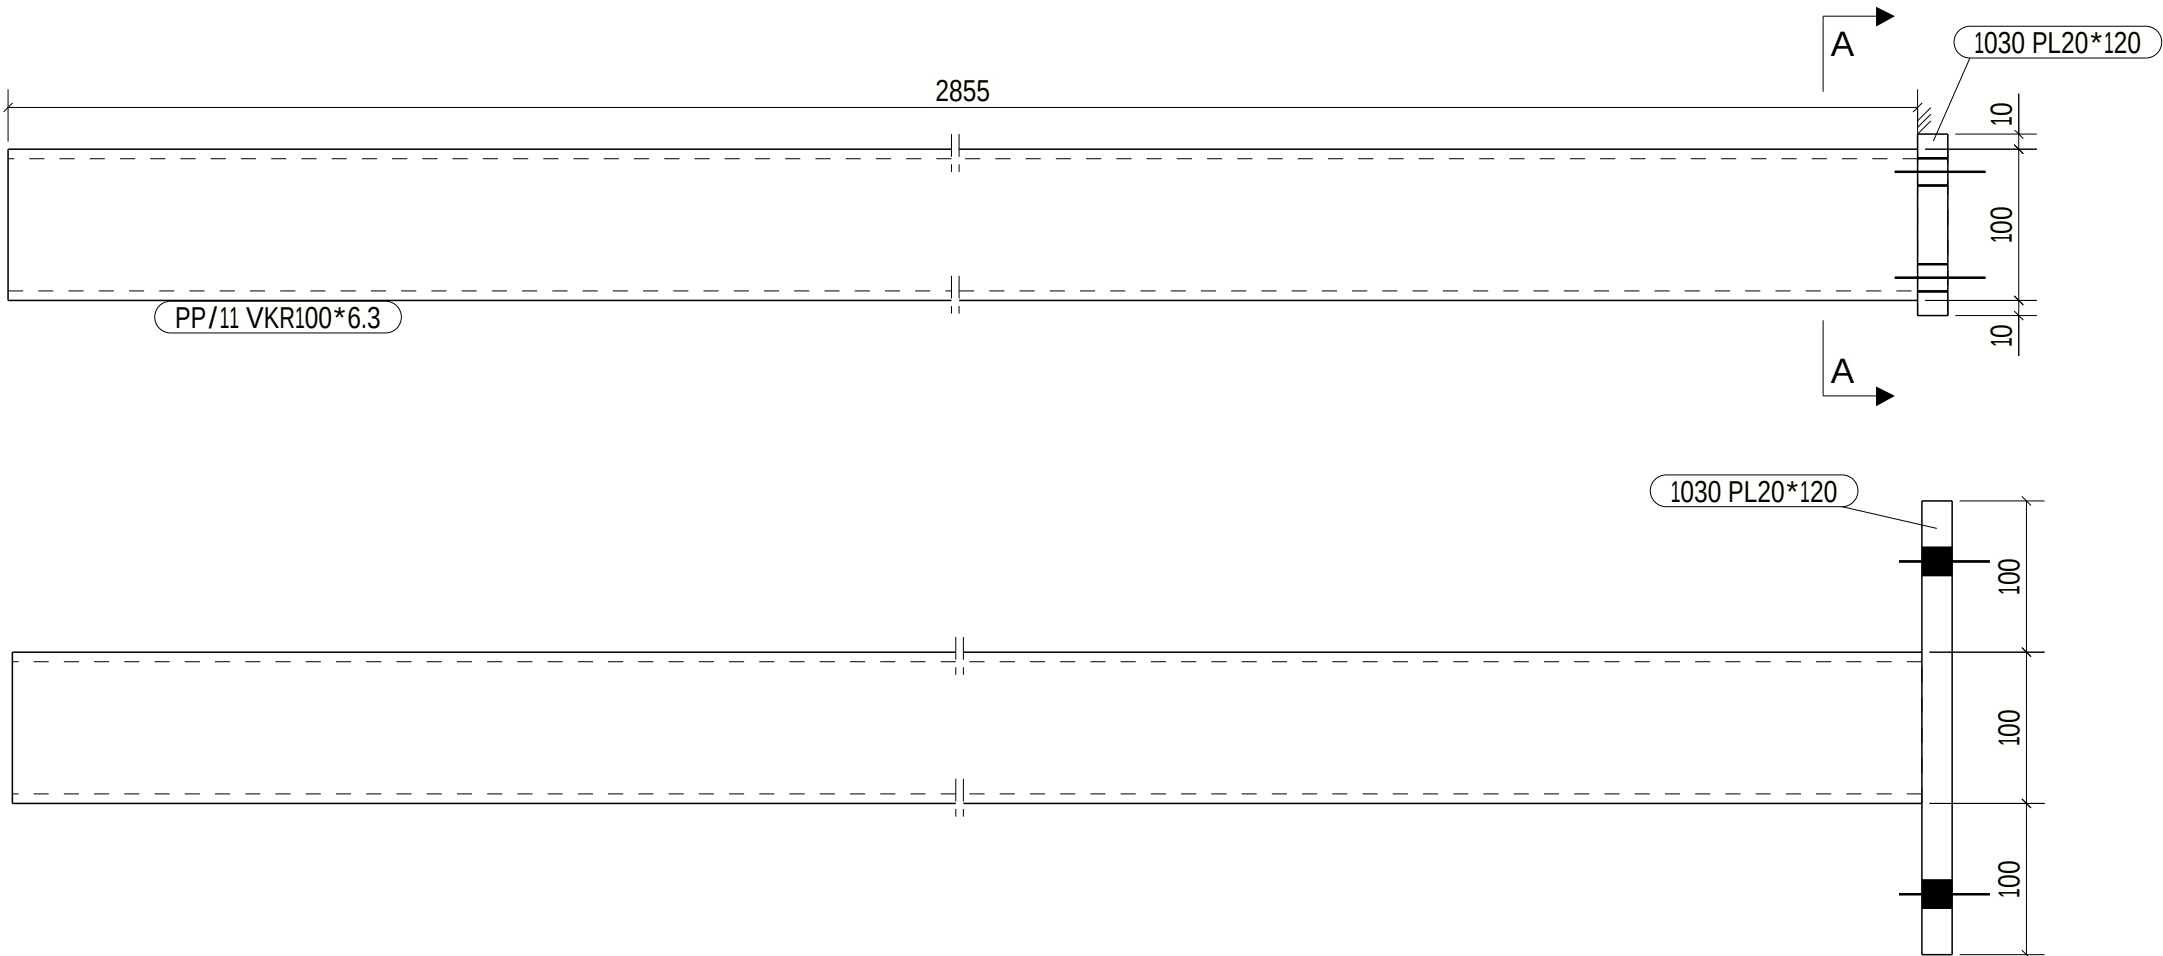

ALLMÄNNA NOTERINGAR: ALLA SVETSAR ÄR KÄLSVETS a5 OM EJ ANNAT ANGES						
MATERIALLISTA FÖR ETT GODS MÄRKT: P/34 1 st. TILLVERKAS						
STYCKLIT.	PROFIL	MATERIAL	ANT.	LÄNGD	AREA/st	VIKT/st
PP/11	VKR100*6.3	S355J2H	1	2855	1.1	52.0
1030	PL20*120	S355J2	1	300	0.1	5.7
TOTALT					1.2	57.6

Norconsult	ANSVARIG PART	PROJEKT	FÖRFRÅGNINGSUNDERLAG		STATUS
	KONTAKTPERSON	CENTRALKÖK ROBERTSFORS KOMMUN	BYGGHANDLING		HANDLING
	GODKÄND AV	TILLVERKNINGSRITNINGAR STÅL	ÄNDRING	FORMAT	A3
	SKAPAD AV	INNEHÅLL	2024-12-20	DATUM	1:5
PARTS			NUMMER	BET	
			P/34		