


PLACERING I STOMNÄT	
NUMMER	SYSTEMLINJE
P/35	3-4/<A
P/35	3-4/A
P/35	4-5/<A
P/35	4-5/A

UTVÄNDIGT STÅL VARMFÖRZINKAS ENLIGT
ALLMÄNNA FÖRESKRIFTER K-01-0-001 -- 003

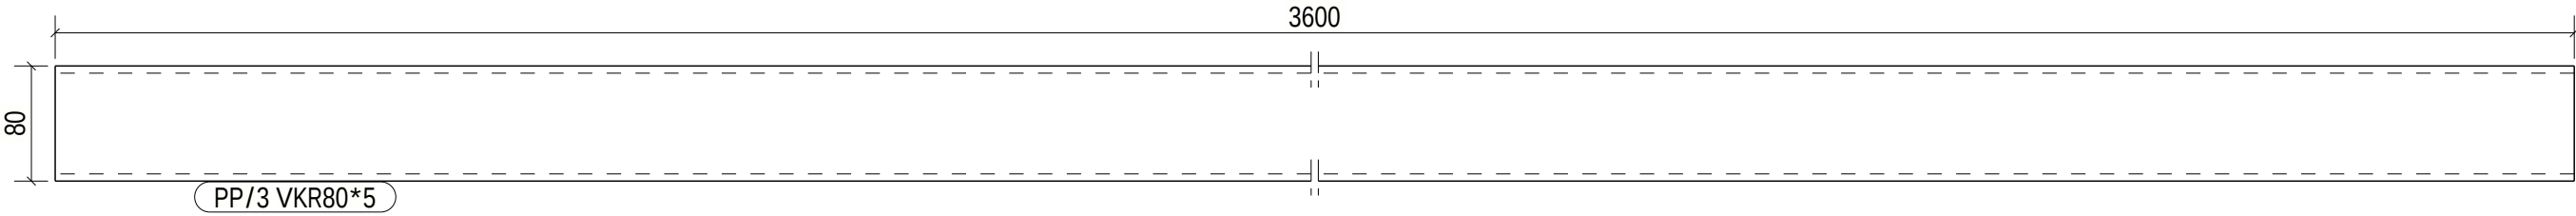

ALLMÄNNA NOTERINGAR: ALLA SVETSAR ÄR KÄLSVETS a5 OM EJ ANNAT ANGES						
MATERIALLISTA FÖR ETT GODS MÄRKT: P/35			4 st. TILLVERKAS			
STYCKLIT.	PROFIL	MATERIAL	ANT.	LÄNGD	AREA/st	VIKT/st
PP/3	VKR80*5	S355J2H	1	3600	1.1	41.5
TOTALT					1.1	41.5

Norconsult ANSVARIG PART	PROJEKT		STATUS	
	CENTRALKÖK ROBERTSFORS KOMMUN		FÖRFRÅGNINGSUNDERLAG	
	TILLVERKNINGSRITNINGAR STÅL		BYGGHANDLING	
	PARTS		A3	
BJÖRN LIDSTRÖM		RITNINGSKATEGORI		ÄNDRING
BJÖRN LIDSTRÖM		INNEHÅLL		DATUM
ARVID WENNERBERG		NUMMER		SKALA
				BET