
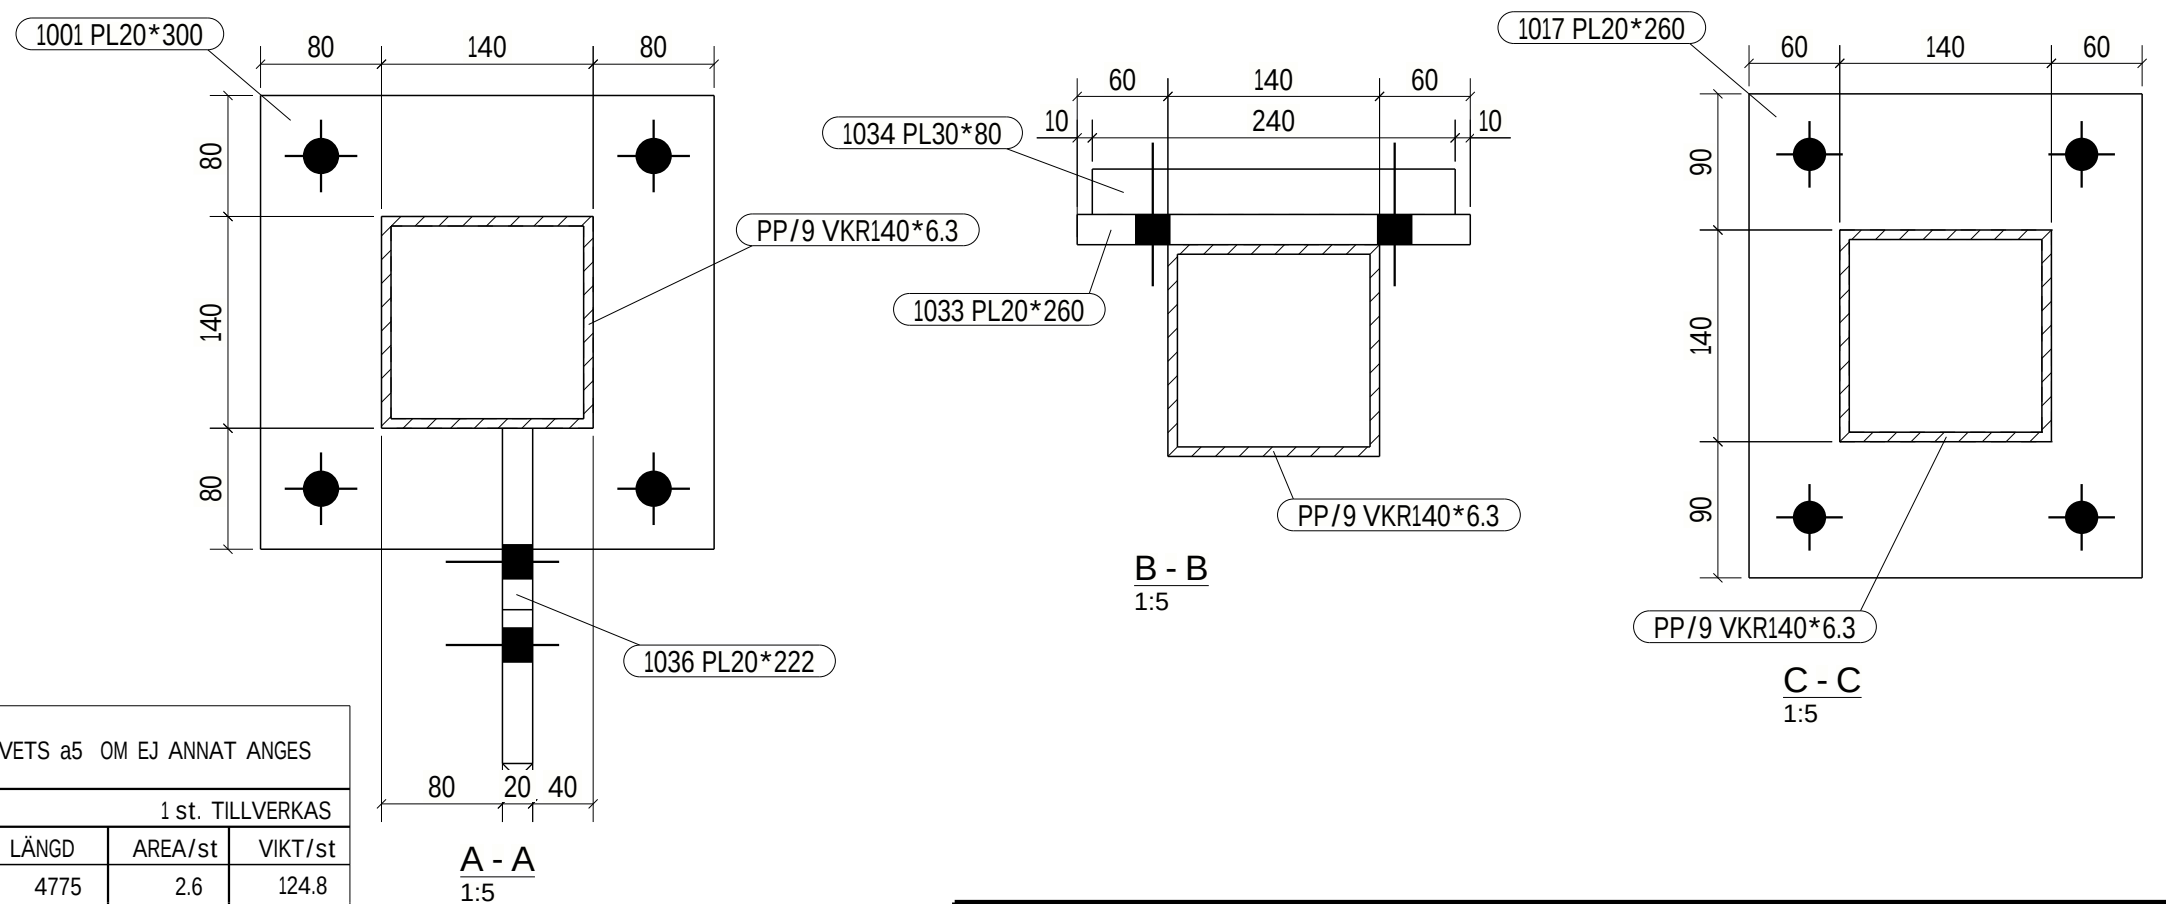


PLACERING I STOMNÄT	
NUMMER	SYSTEMLINJE
P/6	5/B-C

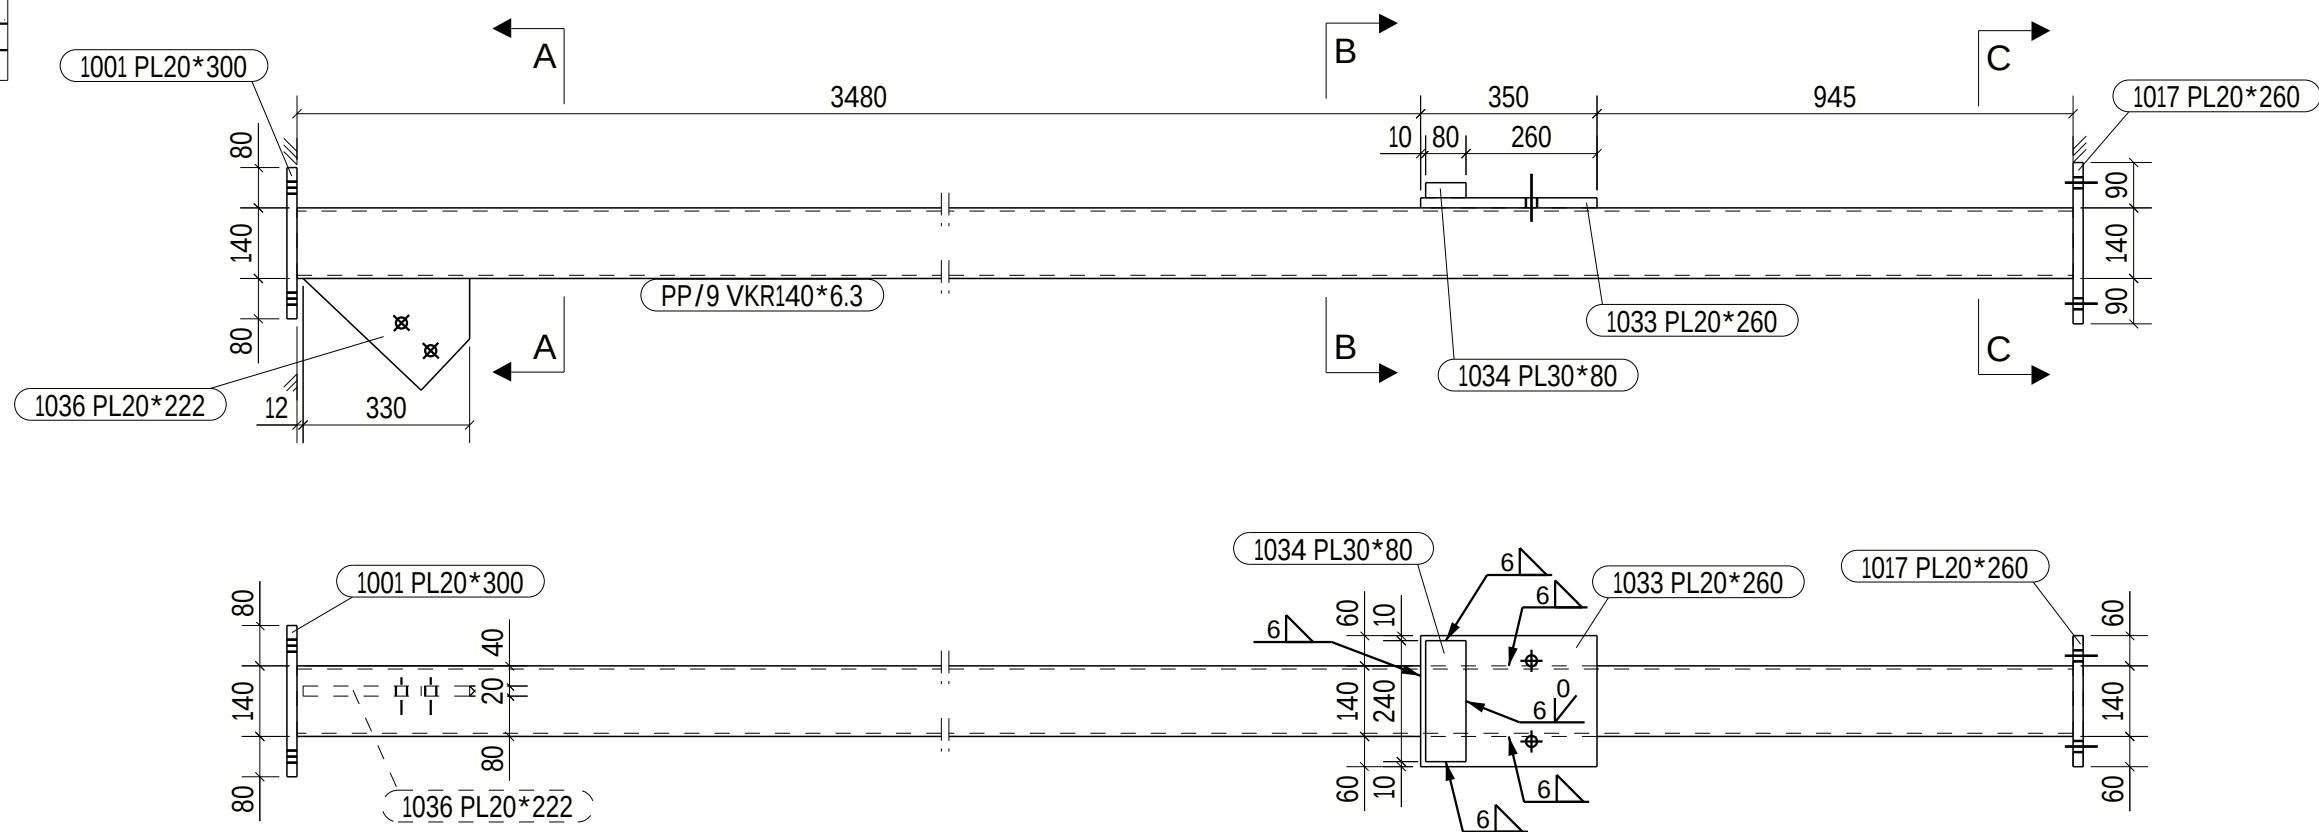

ALLMÄNNA NOTERINGAR: ALLA SVETSAR ÄR KÄLSVETS a5 OM EJ ANNAT ANGES

MATERIALLISTA FÖR ETT GODS MÄRKT: P/6					1 st. TILLVERKAS	
STYCKLIT.	PROFIL	MATERIAL	ANT.	LÄNGD	AREA/st	VIKT/st
PP/9	VKR140*6.3	S355J2H	1	4775	2.6	124.8
1033	PL20*260	S355J2	1	350	0.2	14.3
1001	PL20*300	S355J2	1	300	0.2	14.1
1017	PL20*260	S355J2	1	320	0.2	13.1
1036	PL20*222	S355J2	1	330	0.1	6.7
1034	PL30*80	S355J2	1	240	0.1	4.5
TOTALT					3.3	177.5

Norconsult		ANSVARIG PART	PROJECT	FÖRFRÅGNINGSUNDERLAG		STATUS
BJÖRN LIDSTRÖM		KONTAKTPERSON	CENTRALKÖK ROBERTSFORS KOMMUN	BYGGHANDLING		HANDLING
BJÖRN LIDSTRÖM		GODKÄND AV	TILLVERKNINGSRITNINGAR STÅL	ÄNDRING		FORMAT
ARVID WENNBERG		SKAPAD AV		DATUM		SKALA
			PARTS	2024-12-20		1:15
				P/6		BET