
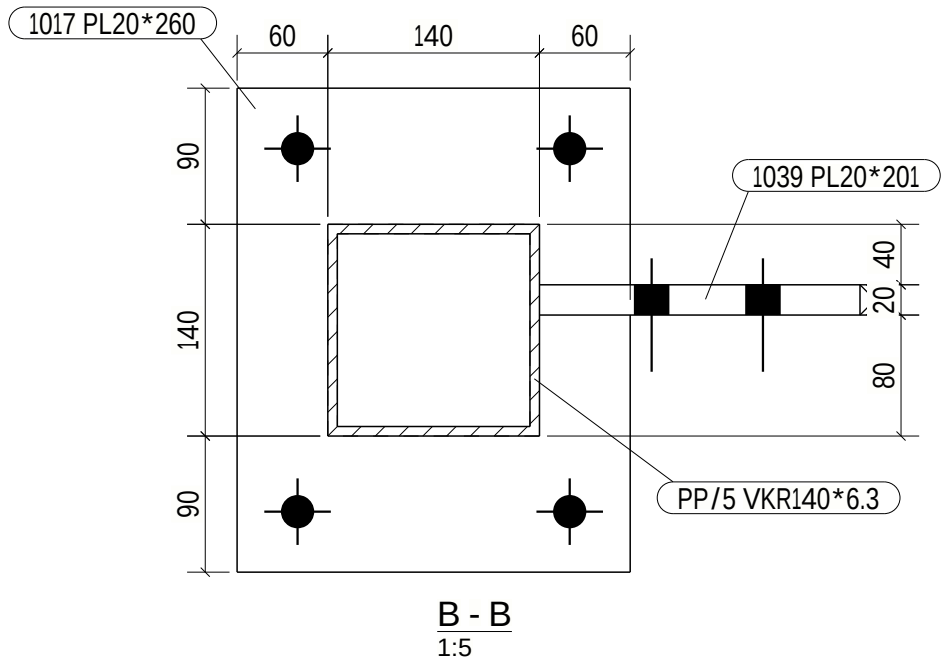
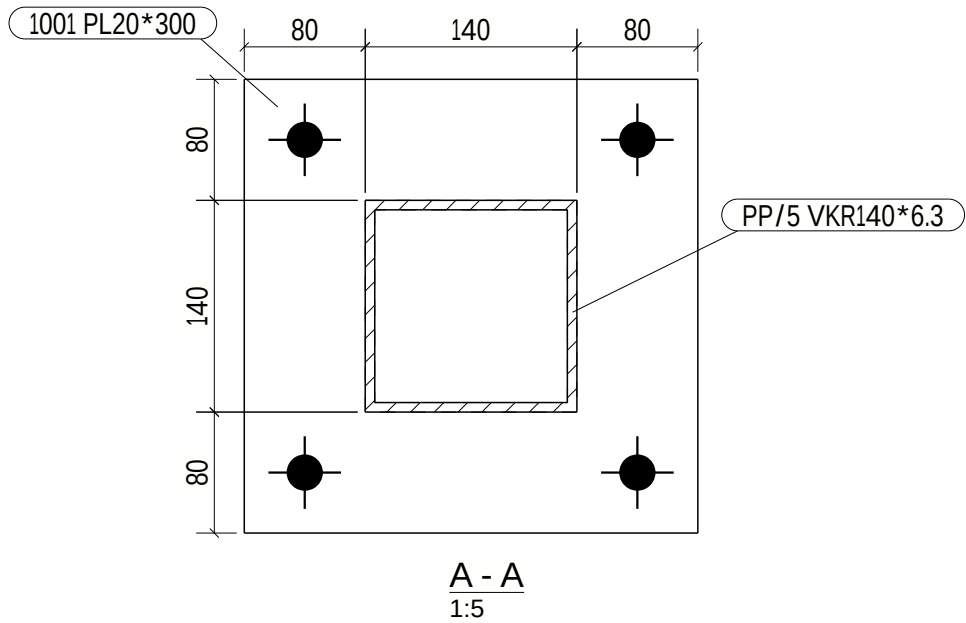


PLACERING I STOMNÄT	
NUMMER	SYSTEMLINJE
P/9	4/B

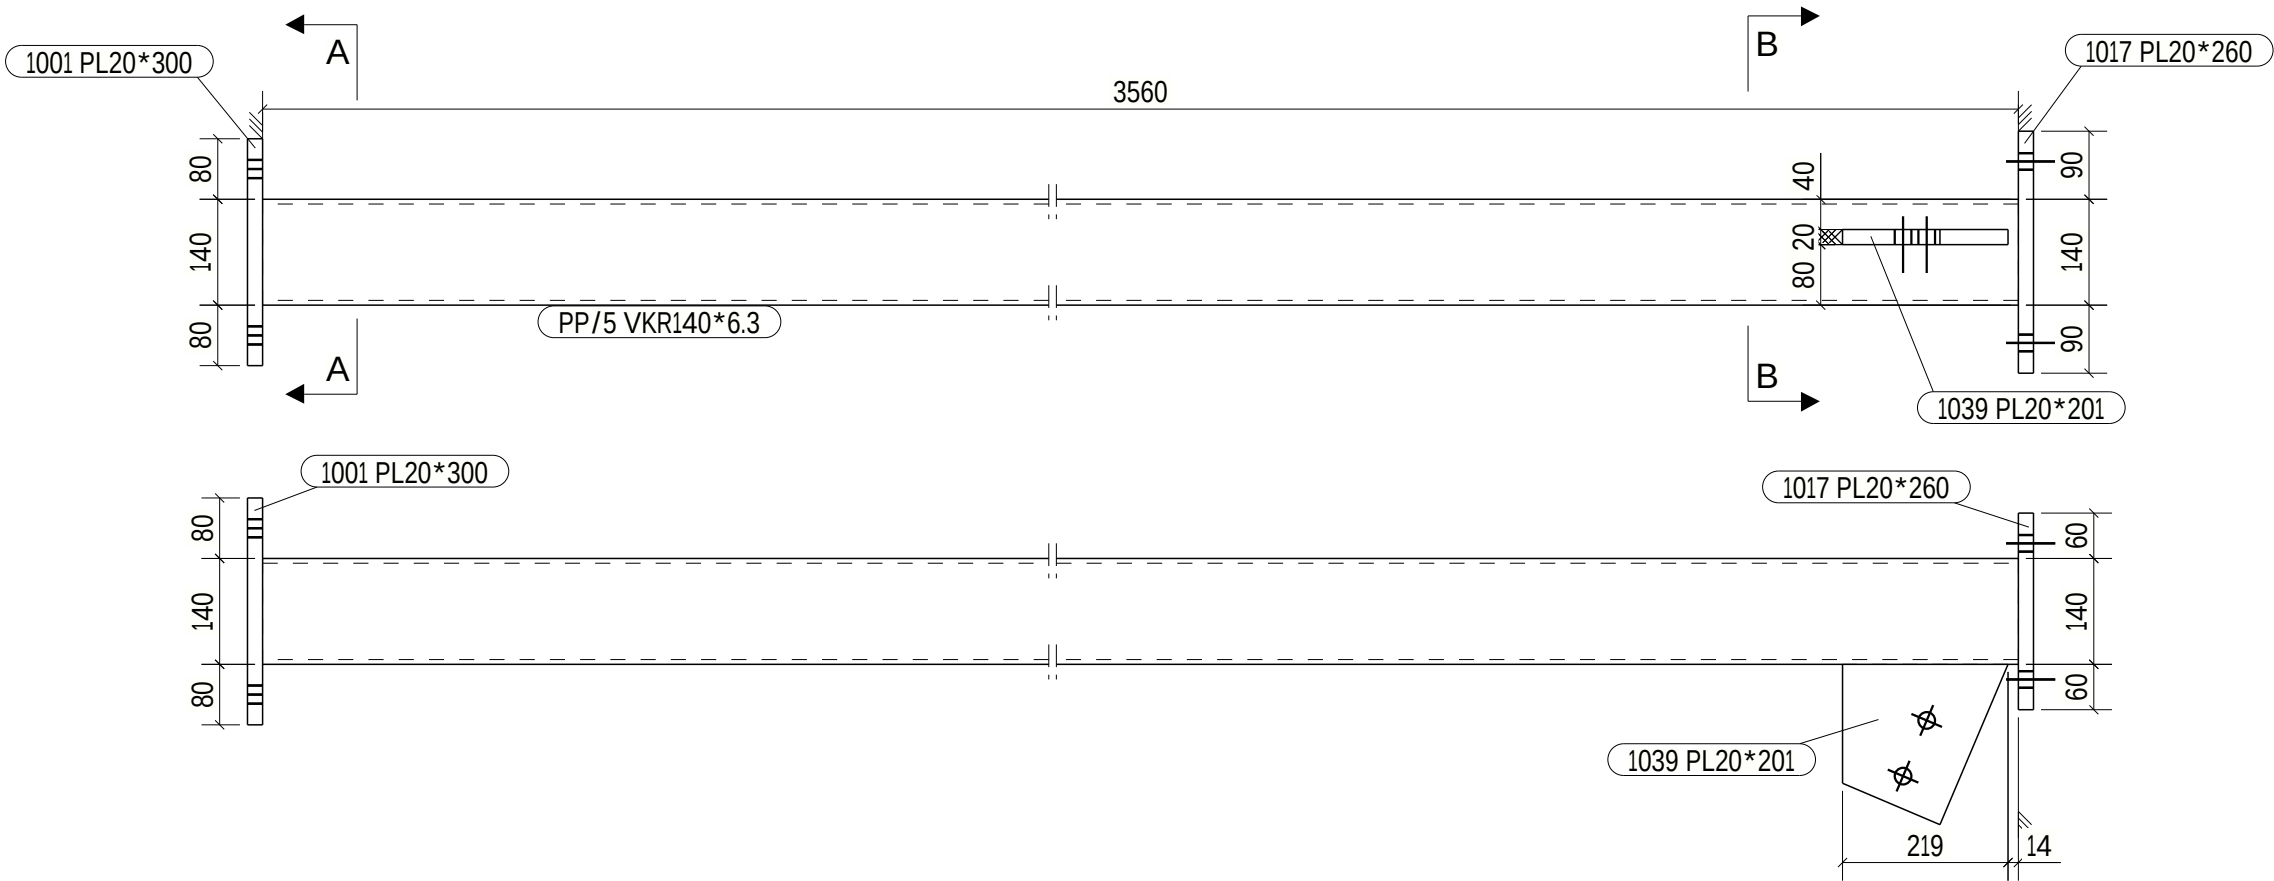

ALLMÄNNA NOTERINGAR: ALLA SVETSAR ÄR KÄLSVETS a5 OM EJ ANNAT ANGES

MATERIALLISTA FÖR ETT GODS MÄRKT: P/9 1 st. TILLVERKAS						
STYCKLIT.	PROFIL	MATERIAL	ANT.	LÄNGD	AREA/st	VIKT/st
PP/5	VKR140*6.3	S355J2H	1	3560	1.9	93.1
1001	PL20*300	S355J2	1	300	0.2	14.1
1017	PL20*260	S355J2	1	320	0.2	13.1
1039	PL20*201	S355J2	1	230	0.1	5.2
TOTALT					2.4	125.5

Norconsult 	ANSVARIG PART	PROJEKT	FÖRFRÅGNINGSUNDERLAG		STATUS
	KONTAKTPERSON	CENTRALEKÖ ROBERTSFORS KOMMUN	BYGGHANDLING		HANDLING
	GODKÄND AV	TILLVERKNINGSRITNINGAR STÅL	ÄNDRING		FORMAT
	SKAPAD AV	INNEHÅLL	2024-12-20		DATUM
PARTS			P/9		NUMMER
			A3		SKALA
			1:5		BET