
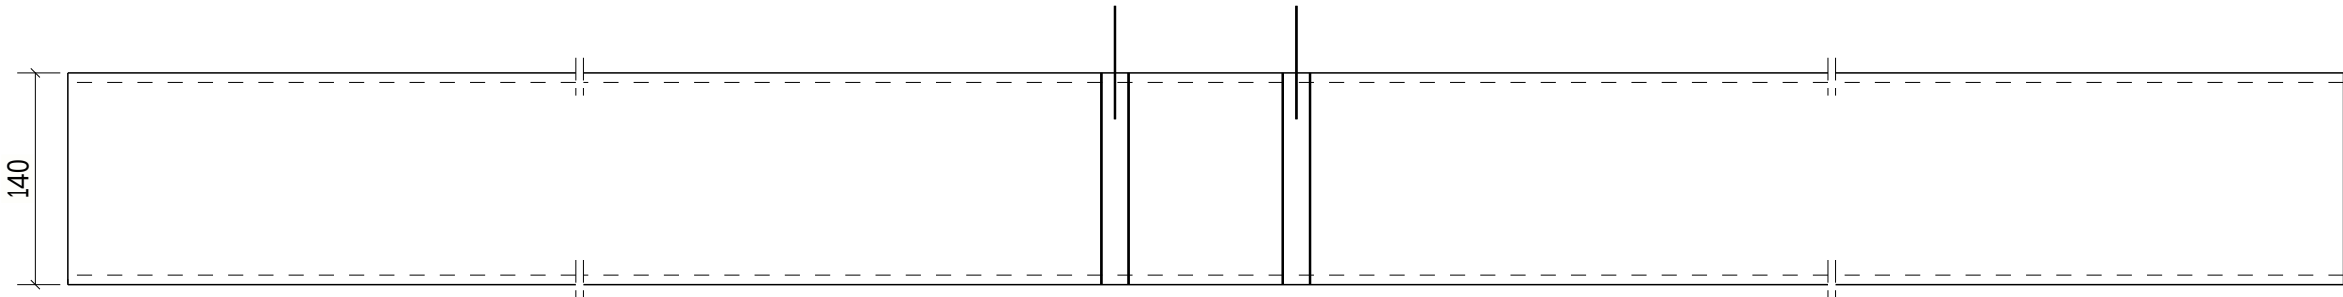


ANTAL	MONTAGEDEL
1	P/27

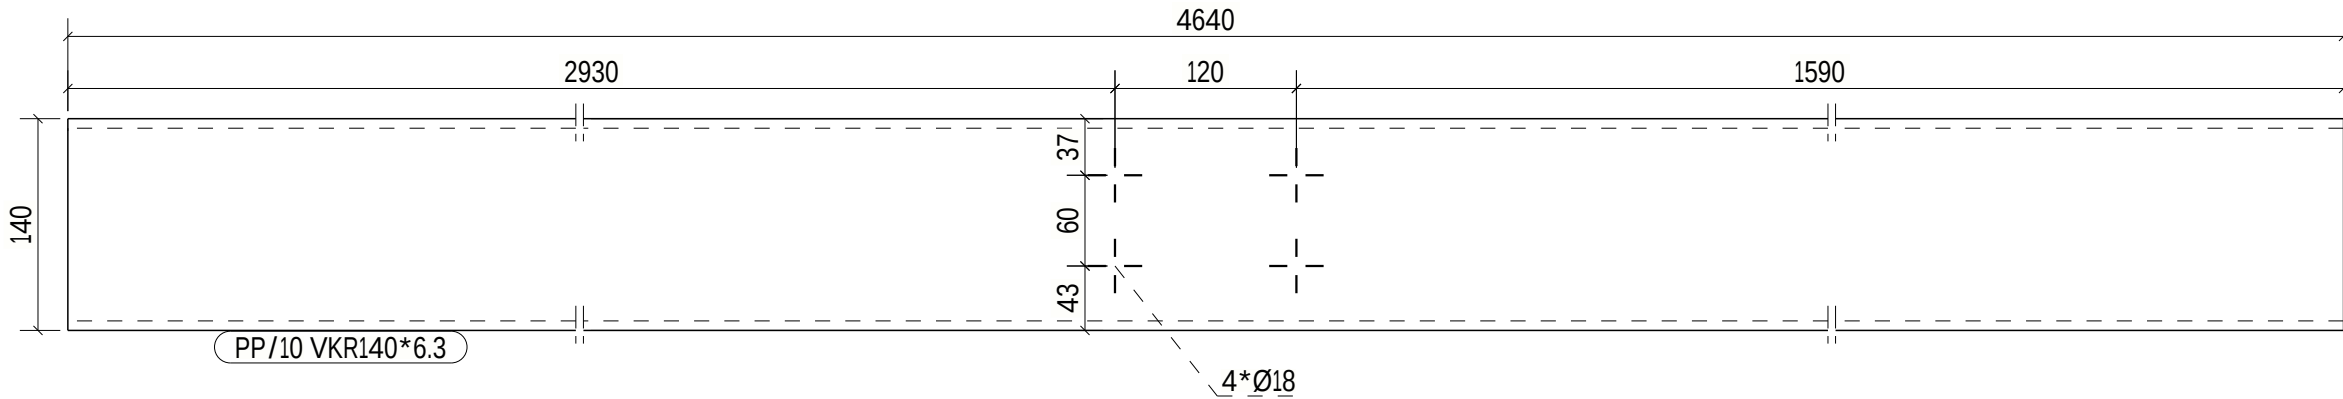

PP/10	VKR140*6.3	S355J2H	1	4639.6	2.51	121.3
MÄRKE	PROFIL	MATERIAL	ANTAL	LÄNGD	AREA	VIKT
MATERIALLISTA				TOTALT	2.51	121.3

Norconsult		CENTRALEKÖ ROBERTSFORS KOMMUN		FÖRFRÅGNINGSUNDERLAG	
BJÖRN LIDSTRÖM		TILLVERKNINGSRITNINGAR STÅL		BYGGHANDLING	
ARVID WENNERBERG		PARTS		2024-12-20	
				1:5	
				PP/10	