


ANTAL	MONTAGEDEL
1	P/34

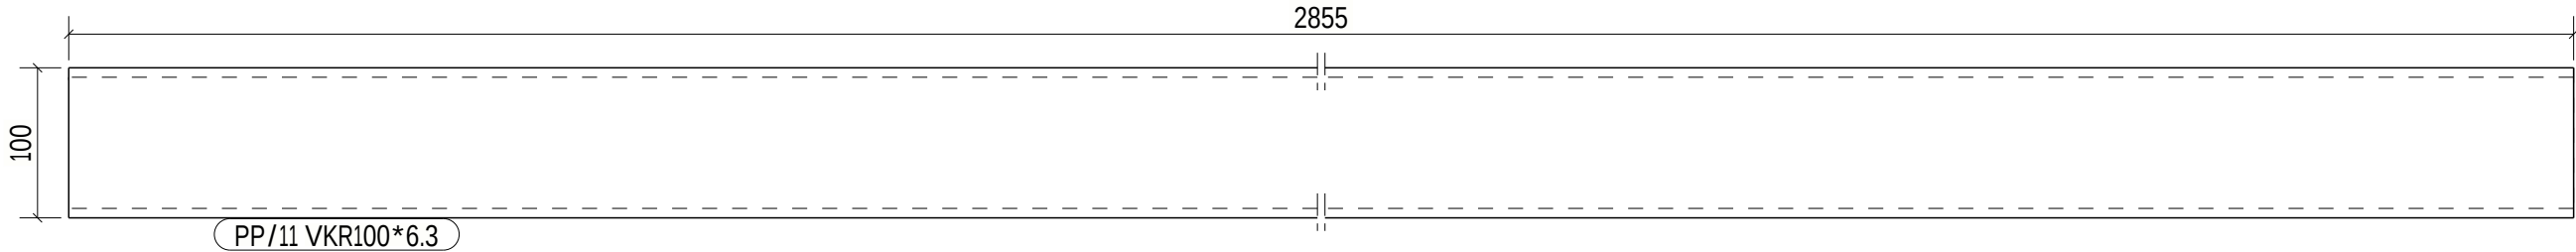

PP/11	VKR100*6.3	S355J2H	1	2855.0	1.08	52.0
MÄRKE	PROFIL	MATERIAL	ANTAL	LÄNGD	AREA	VIKT
MATERIALLISTA				TOTALT	1.08	52.0

Norconsult ANSVARIG PART BJÖRN LIDSTRÖM BJÖRN LIDSTRÖM ARVID WENNERBERG	CENTRALKÖK ROBERTSFORS KOMMUN	FÖRFRÅGNINGSUNDERLAG	
		BYGGHANDLING	
	TILLVERKNINGSRITNINGAR STÅL	2024-12-20	A3
	PARTS	PP/11	