


ANTAL	MONTAGEDEL
1	P/19

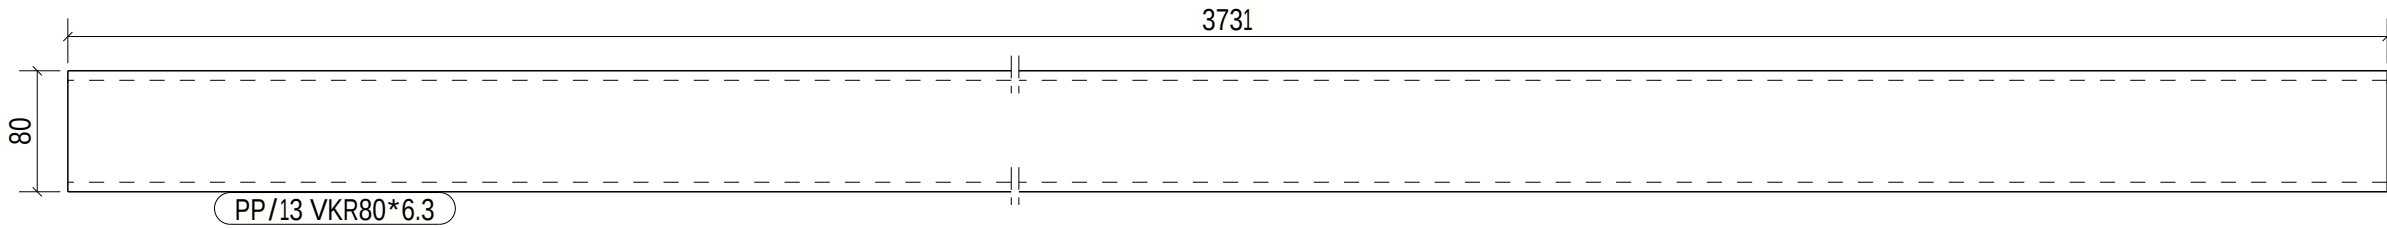

PP/13	VKR80*6.3	S355J2H	1	3731.0	1.12	53.0
MÄRKE	PROFIL	MATERIAL	ANTAL	LÄNGD	AREA	VIKT
MATERIALLISTA				TOTALT	1.12	53.0

Norconsult ANSVARIG PART BJÖRN LIDSTRÖM BJÖRN LIDSTRÖM ARVID WENNERBERG	CENTRAALKÖK ROBERTSFORS KOMMUN	FÖRFRÅGNINGSUNDERLAG	
		BYGGHANDLING	
	TILLVERKNINGSRITNINGAR STÅL	2024-12-20	A3
	PARTS	PP/13	