


ANTAL	MONTAGEDEL
1	P/25

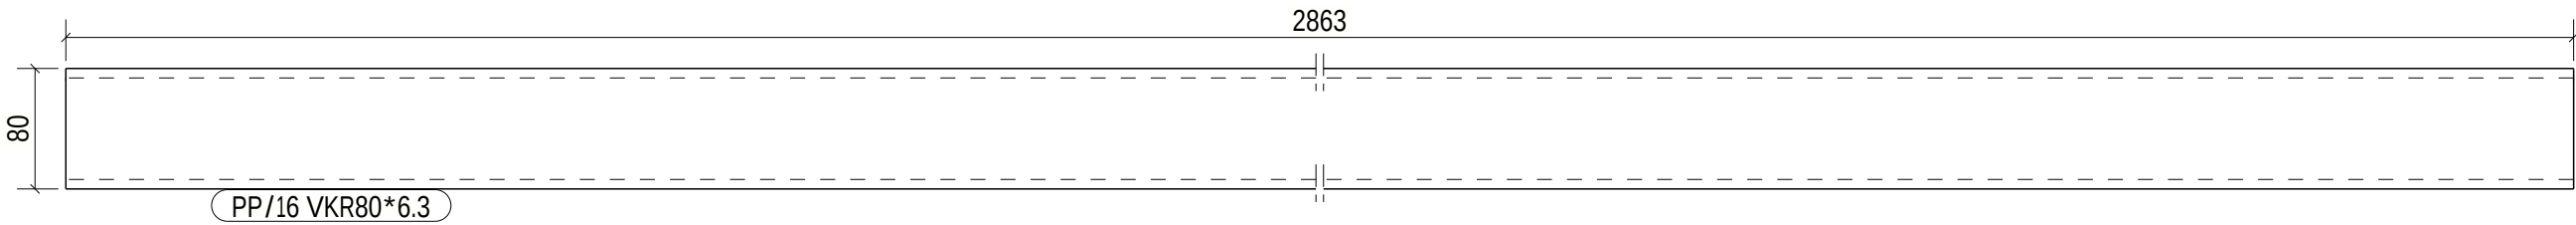

PP/16	VKR80*6.3	S355J2H	1	2862.7	0.86	40.7
MÄRKE	PROFIL	MATERIAL	ANTAL	LÄNGD	AREA	VIKT
MATERIALLISTA				TOTALT	0.86	40.7

Norconsult ANSVARIG PART BJÖRN LIDSTRÖM BJÖRN LIDSTRÖM ARVID WENNERBERG	CENTRAALKÖK ROBERTSFORS KOMMUN	FÖRFRÅGNINGSUNDERLAG	
		BYGGHANDLING	
	TILLVERKNINGSRITNINGAR STÅL	2024-12-20	A3
	PARTS	PP/16	