


ANTAL	MONTAGEDEL
1	P/17
2	P/26

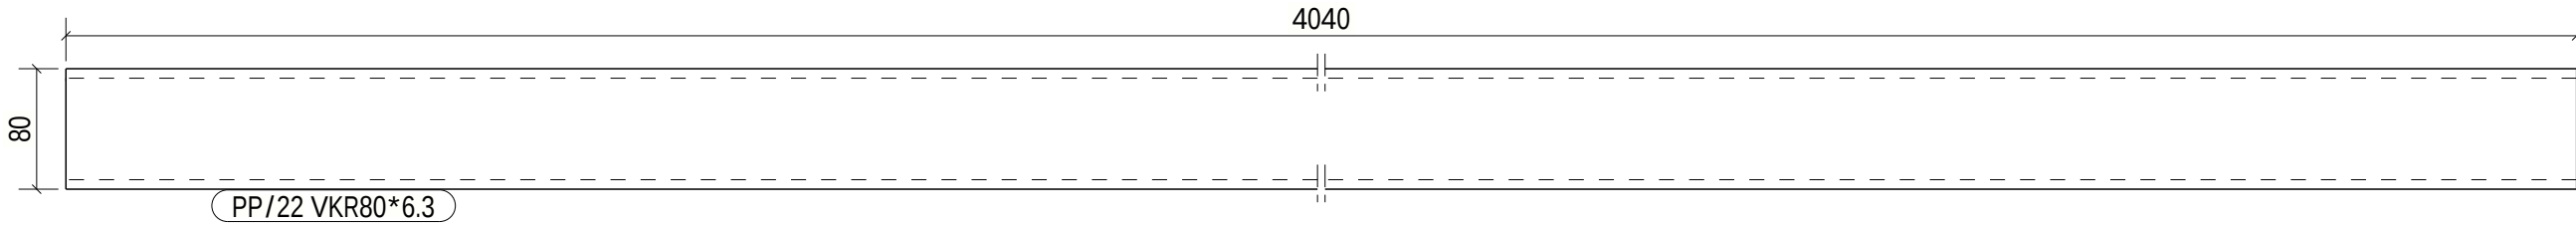

PP/22	VKR80*6.3	S355J2H	3	4040.0	1.21	57.4
MÄRKE	PROFIL	MATERIAL	ANTAL	LÄNGD	AREA	VIKT
MATERIALLISTA				TOTALT	3.64	172.2

Norconsult ANSVARIG PART BJÖRN LIDSTRÖM BJÖRN LIDSTRÖM ARVID WENNERBERG	CENTRALKÖK ROBERTSFORS KOMMUN	FÖRFRÅGNINGSUNDERLAG	
		BYGGHANDLING	
	TILLVERKNINGSRITNINGAR STÅL	2024-12-20	A3
	PARTS	PP/22	