


| ANTAL | MONTAGEDEL |
|-------|------------|
| 1     | P/29       |
| 1     | P/30       |
| 2     | P/31       |

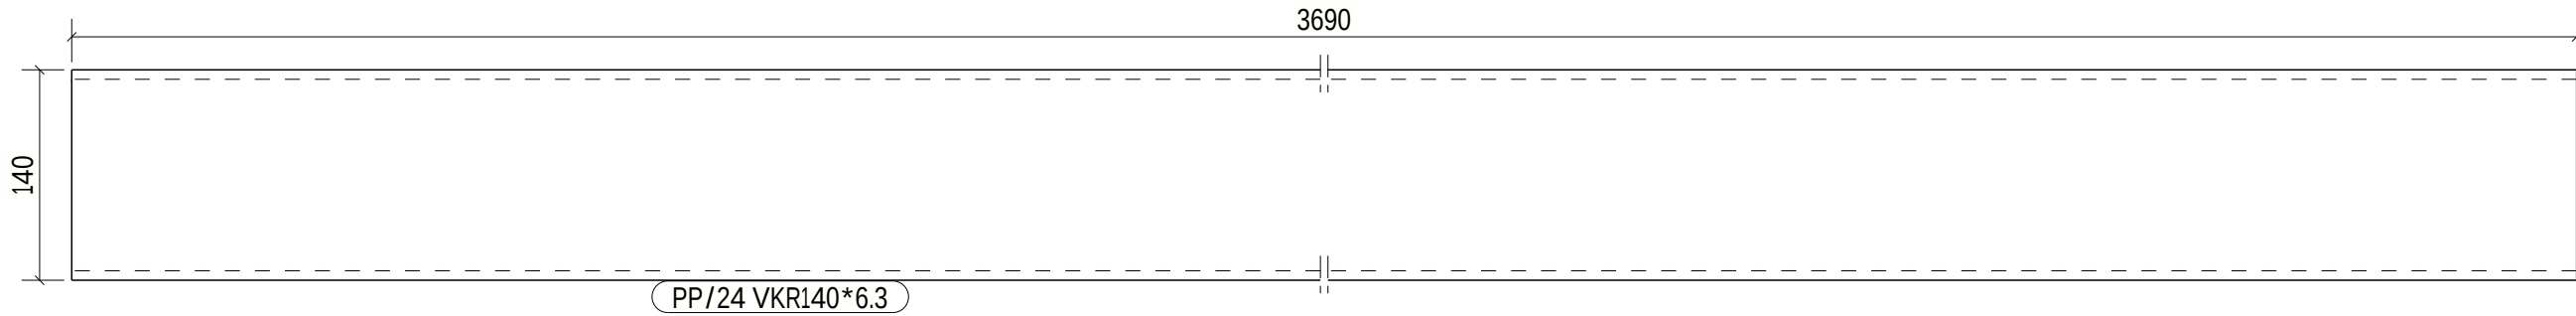

|               |            |          |       |        |      |       |
|---------------|------------|----------|-------|--------|------|-------|
| PP/24         | VKR140*6.3 | S355J2H  | 4     | 3690.0 | 1.99 | 96.5  |
| MÄRKE         | PROFIL     | MATERIAL | ANTAL | LÄNGD  | AREA | VIKT  |
| MATERIALLISTA |            |          |       | TOTALT | 7.97 | 385.8 |

|   |                                |                      |    |
|---|--------------------------------|----------------------|----|
| <div>Norconsult</div> <div>ANSVARIG PART</div> <div>BJÖRN LIDSTRÖM</div> <div>BJÖRN LIDSTRÖM</div> <div>ARVID WENNERBERG</div> | CENTRAALKÖK ROBERTSFORS KOMMUN | FÖRFRÅGNINGSUNDERLAG |    |
|   |                                | BYGGHANDLING         |    |
|   | TILLVERKNINGSRITNINGAR STÅL    | 2024-12-20           | A3 |
|   | PARTS                          | PP/24                |    |