


ANTAL	MONTAGEDEL
1	P/33

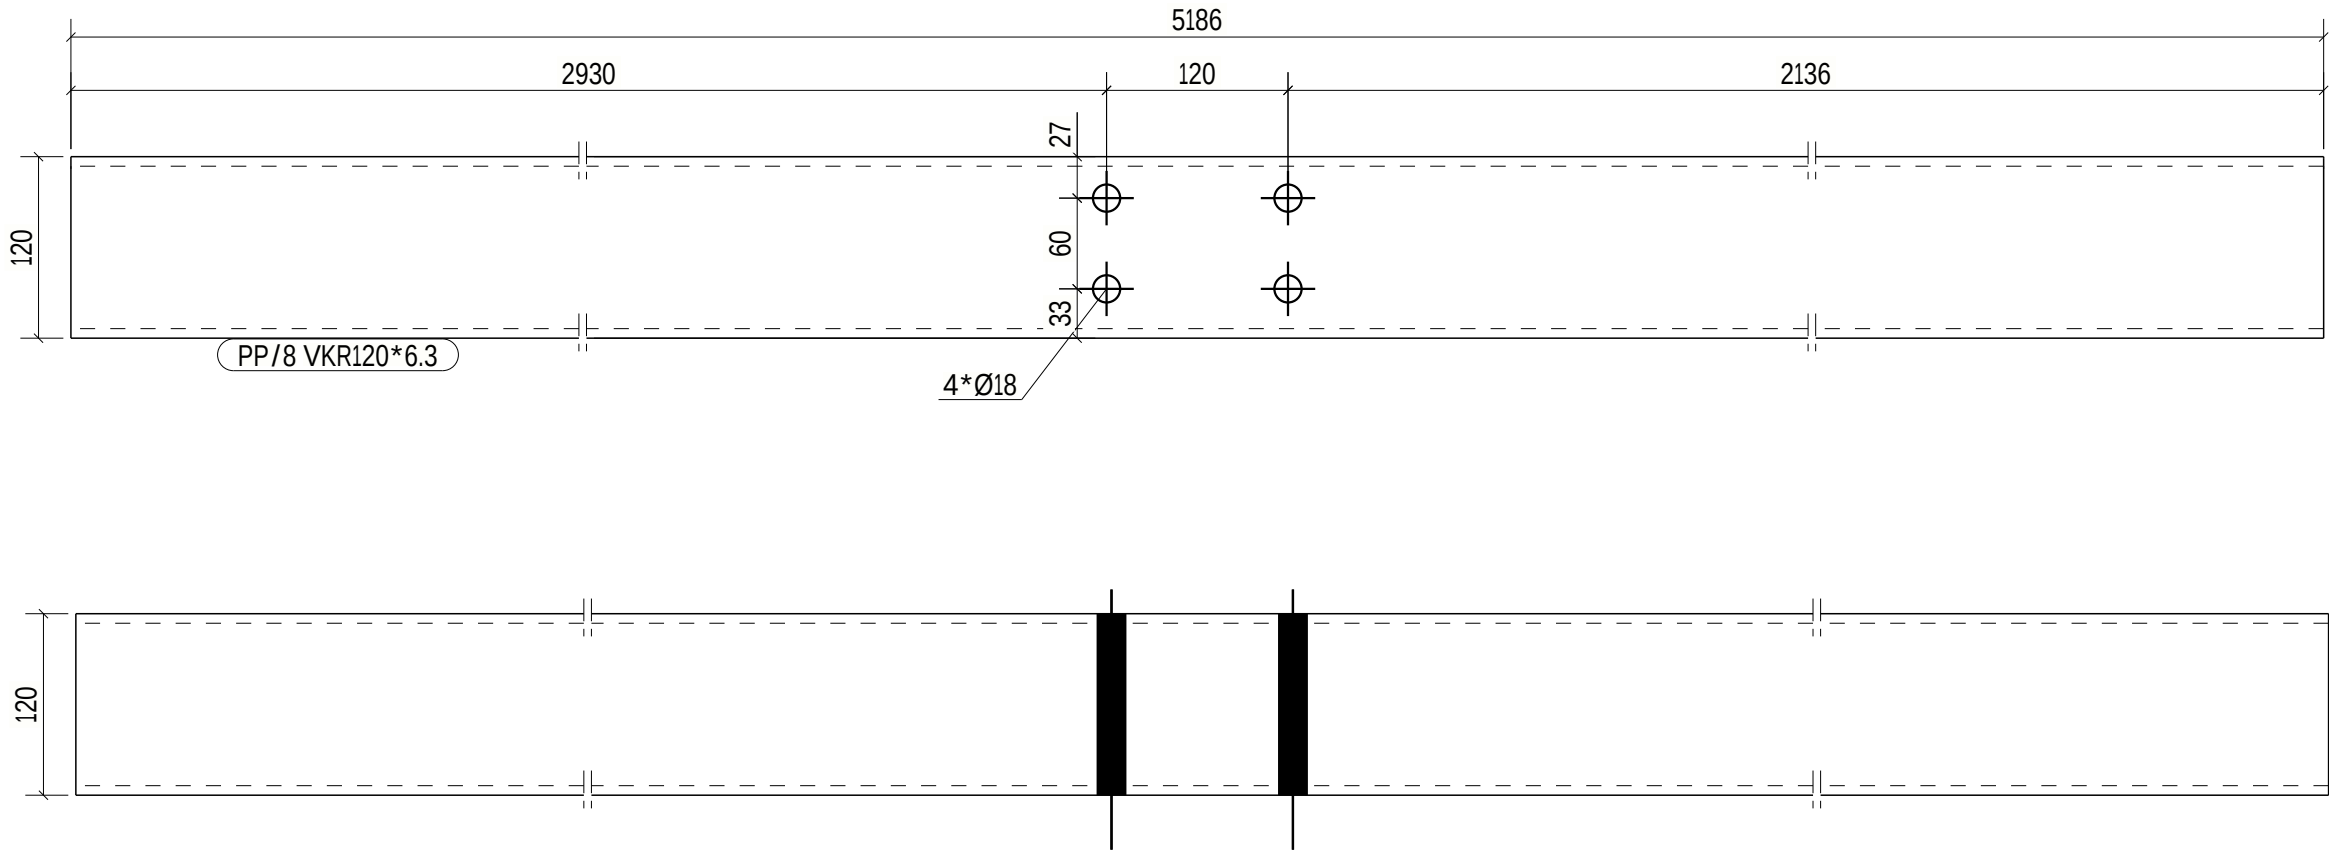

PP/8	VKR120*6.3	S355J2H	1	5185.7	2.39	114.8
MÄRKE	PROFIL	MATERIAL	ANTAL	LÄNGD	AREA	VIKT
MATERIALLISTA				TOTALT	2.39	114.8

Norconsult ANSVARIG PART BJÖRN LIDSTRÖM BJÖRN LIDSTRÖM ARVID WENNERBERG	CENTRALEKÖK ROBERTSFORS KOMMUN TILLVERKNINGSRITNINGAR STÅL PARTS	FÖRFRÅGNINGSUNDERLAG		STATUS	
		BYGGHANDLING		HANDLING	
		2024-12-20		ÄNDRING	FORMAT
		PP/8		NUMMER	BET