


ANTAL	MONTAGEDEL
1	P/6
1	P/7

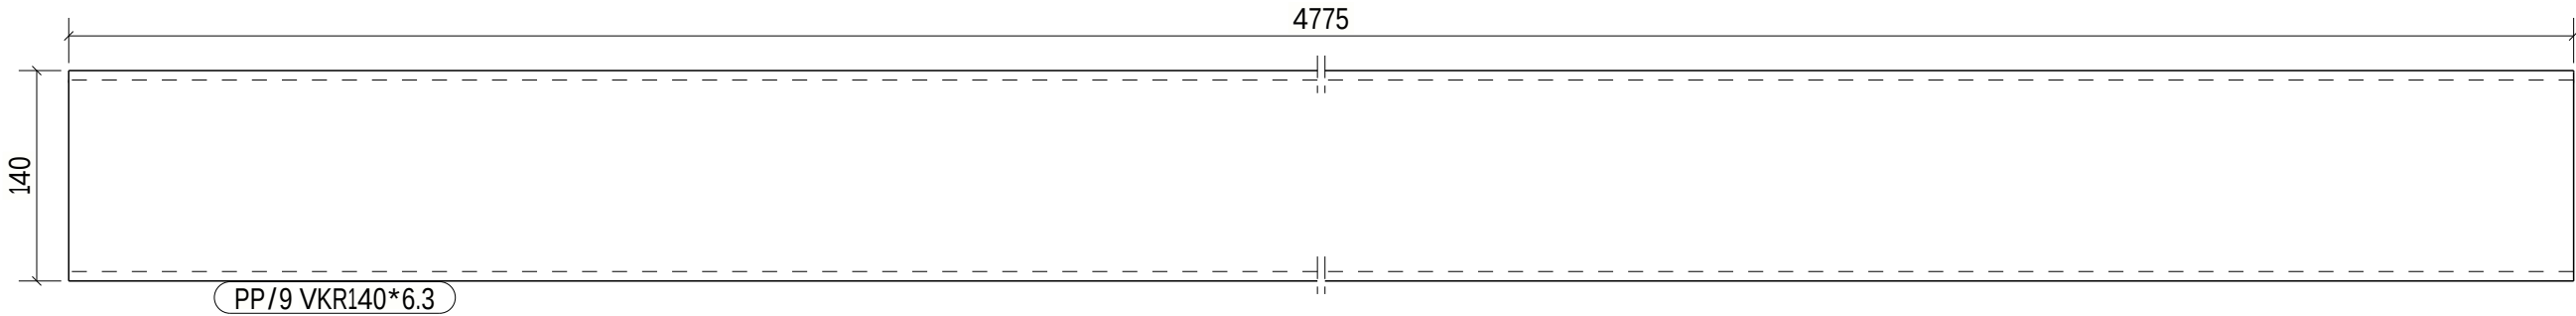

PP/9	VKR140*6.3	S355J2H	2	4774.6	2.58	124.8
MÄRKE	PROFIL	MATERIAL	ANTAL	LÄNGD	AREA	VIKT
MATERIALLISTA				TOTALT	5.16	249.6

Norconsult ANSVARIG PART BJÖRN LIDSTRÖM BJÖRN LIDSTRÖM ARVID WENNERBERG	CENTRAALKÖK ROBERTSFORS KOMMUN	FÖRFRÅGNINGSUNDERLAG	
		BYGGHANDLING	
	TILLVERKNINGSRITNINGAR STÅL	2024-12-20	A3
	PARTS	PP/9	