



PLACERING I STOMNÄT	
NUMMER	SYSTEMLINJE
B/17	4/A-C

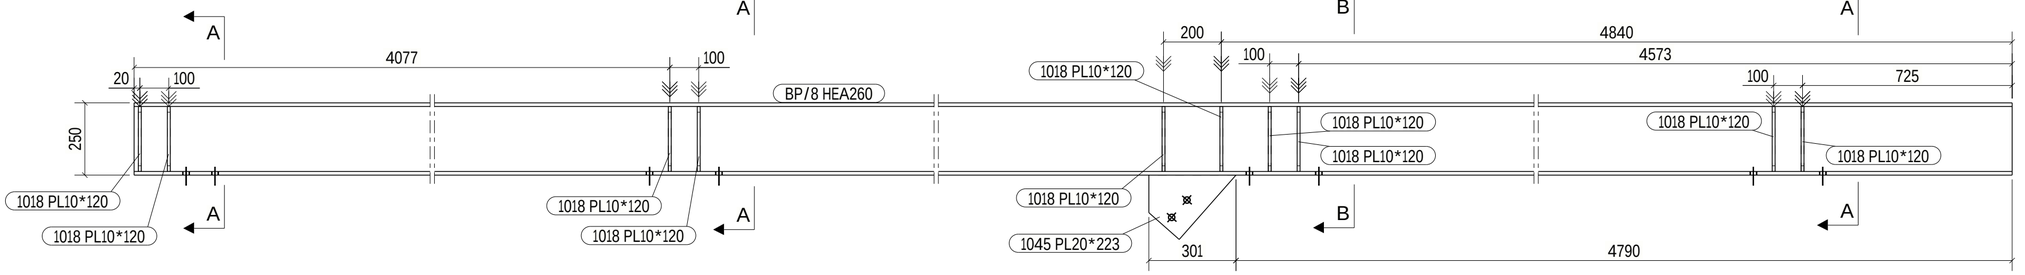

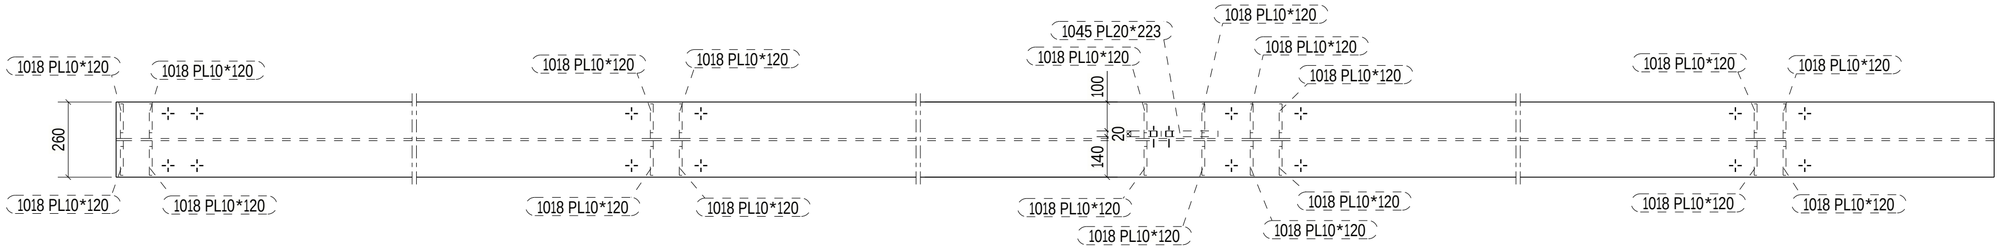

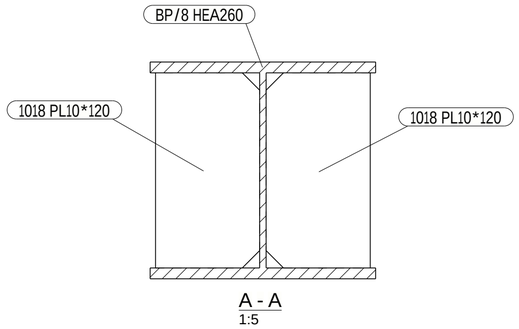

A - A
1:5

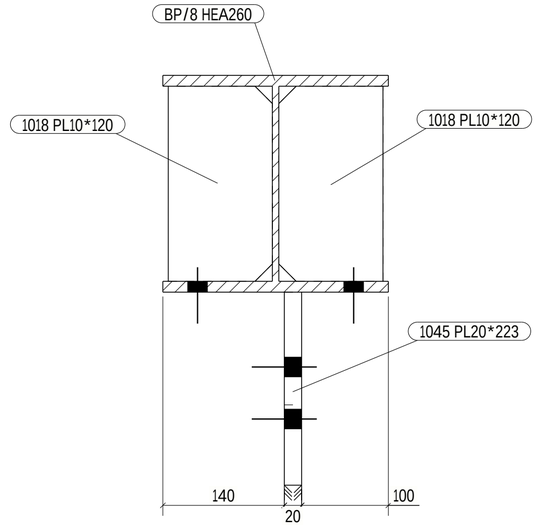

B - B
1:5

ALLMÄNNA NOTERINGAR:

ALLA HÅL ÄR 22 mm OM EJ ANNAT ANGES
ALLA SVETSAR ÄR 6.5 mm OM EJ ANNAT ANGES

MATERIALLISTA FÖR ETT GODS MÄRKT: B/17 — 1 st. TILLVERKAS

STYCKLIT.	PROFIL	MATERIAL	ANT.	LÄNGD	AREA/st	VIKT/st
BP/8	HEA260	S355J2	1	12000	17.8	817.8
1045	PL20*223	S355J2	1	301	0.1	6.3
1018	PL10*120	S355J2	20	225	0.1	2.1
				TOTALT	19.1	865.9

ANSVARIG PART: Norconsult	PROJEKT: CENTRALKÖK ROBERTSFORS KOMMUN	STATUS: FÖRFRÅGNINGSUNDERLAG	
KONTAKTPERSON: BJÖRN LIDSTRÖM	RITNINGSKATEGORI: TILLVERKNINGSRITNINGAR STÅL	HANDLING: BYGGHANDLING	
GODKÄND AV: BJÖRN LIDSTRÖM	INNEHÅLL: PARTS	ÄNDRING:	FORMAT: A2
SKAPAD AV: ARVID WENNBERG		DATUM: 2024-12-20	SKALA: 1:15
		NUMMER: B/17	BET:

Tekla Structures