

| ANTAL | MONTAGEDEL |
|---|---|
| 1 | B/26 |

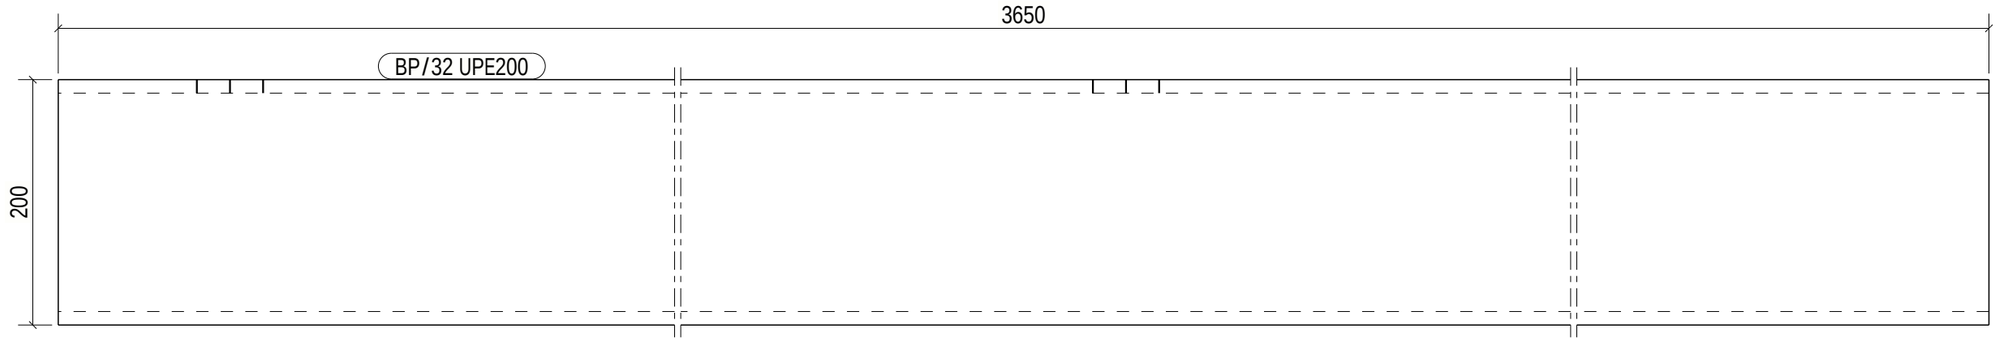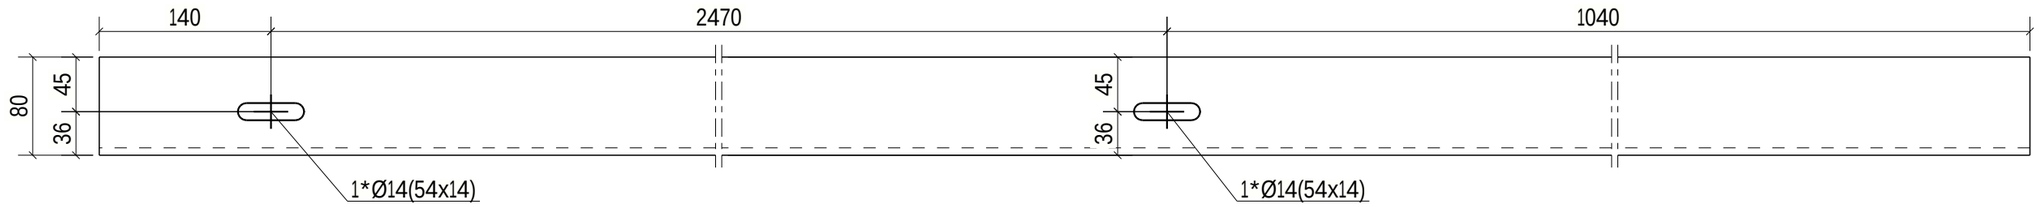


| BP/32 | UPE200 | S355J2 | 1 | 3650.0 | 2.54 | 83.1 |
|---|---|---|---|---|---|---|
| MÄRKE | PROFIL | MATERIAL | ANTAL | LÄNGD | AREA | VIKT |
| MATERIALLISTA | | | | TOTALT | 2.54 | 83.1 |

| | | |
|---|---|---|
| Norconsult<br>ANSVARIG PART | PROJEKT<br>CENTRALKÖK ROBERTSFORS KOMMUN | STATUS<br>FÖRFRÅGNINGSUNDERLAG |
| KONTAKTPERSON<br>BJÖRN LIDSTRÖM | | HANDLING<br>BYGGHANDLING |
| GODKÄND AV<br>BJÖRN LIDSTRÖM | RITNINGSKATEGORI<br>TILLVERKNINGSRITNINGAR STÅL | ÄNDRING / FORMAT<br>A3 |
| SKAPAD AV<br>ARVID WENNBERG | INNEHÅLL<br>PARTS | DATUM / SKALA<br>2024-12-20 / 1:5 |
| | | NUMMER / BET<br>BP/32 |

Tekla Structures