
ANTAL	MONTAGEDEL
1	P/2

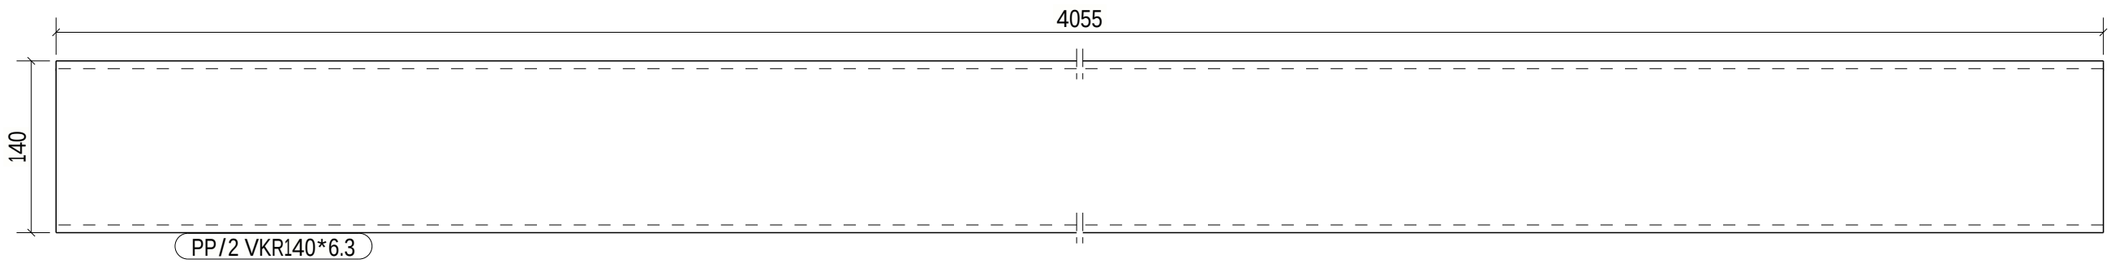

PP/2	VKR140*6.3	S355J2H	1	4055.0	2.19	106.0
MÄRKE	PROFIL	MATERIAL	ANTAL	LÄNGD	AREA	VIKT
MATERIALLISTA				TOTALT	2.19	106.0

ANSVARIG PART Norconsult	PROJEKT CENTRALKÖK ROBERTSFORS KOMMUN	STATUS FÖRFRÅGNINGSUNDERLAG
KONTAKTPERSON BJÖRN LIDSTRÖM		HANDLING BYGGHANDLING
GODKÄND AV BJÖRN LIDSTRÖM	RITNINGSKATEGORI TILLVERKNINGSRITNINGAR STÅL	ÄNDRING / FORMAT A3
SKAPAD AV ARVID WENNBERG	INNEHÅLL PARTS	DATUM / SKALA 2024-12-20 / 1:5
		NUMMER / BET PP/2

Tekla Structures