

FÖRKLARINGAR

MÅTT ANGES I MILLIMETER DÄR EJ ANNAT ANGES.
PLUSHÖJDER ANGES I METER, PLUSHÖJDER ENLIGT RH2000
OCH AVSER FÄRDIG YTA, DÄR EJ ANNAT ANGES.


- BRANDCELLSGRÄNS EI30
- DÖRRAR/FÖNSTER
EI5/E30/EI30/EI60 = BRANDKLASSAD DÖRR/FÖNSTER
-C = DÖRRSTÄNGARE
M = MAGNETHÅLLARE
-Sm/-Sa/S200 = BRANDTÄTHET DÖRRAR ENL DÖRRUPPSTÄLLNING

- UTRYMNINGSRIKTNING
- VÄGLEDANDE MARKERING FÖR TILLGÄNGLIG UTRYMNING NÖDBELYST
- HANDBRANDSLÄCKARE
- UTRYMNINGSPLAN
- +XX.XXX = HÖJD ÖVER FÄRDIGT GOLV, METER
- BEFINTLIG VÄGG
- BÄRANDE INNERVÄGG ENL. K
- KYL-/FRYSRUMSVÄGG
- NY VÄGG
- BEF. DÖRR
- NY DÖRR
- KYLUMSDÖRR

HÄNVISNINGAR

- PLAN - RIVNING A-40-1-001-R
- FASADER - RIVNING A-40-3-001-R
- FASADER - ÖVERSIKT A-40-3-001

RITNING KRÄVER FÄRGUTSKRIFT FÖR KORREKT UTSEENDE

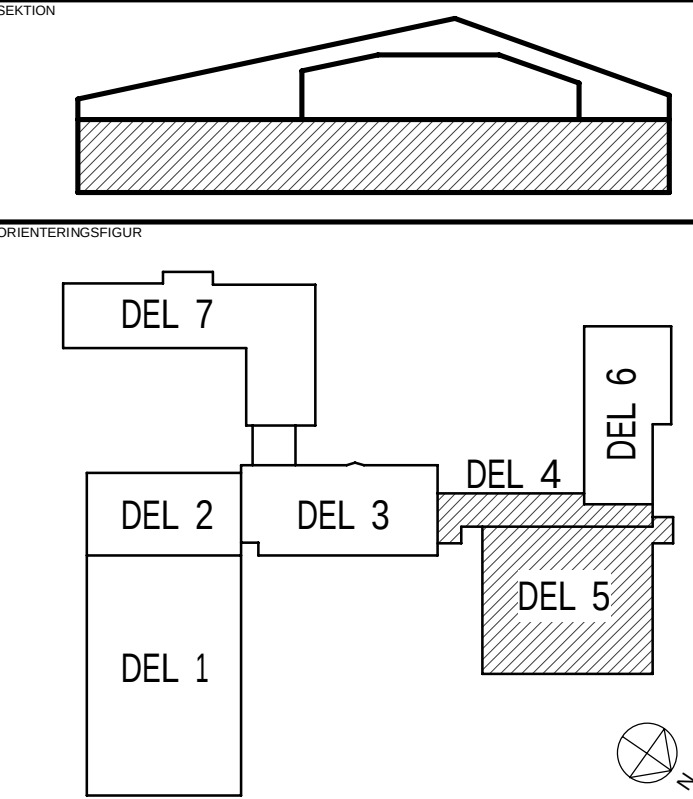

STATUS

FÖRFRÅGNINGSUNDERLAG

HANDLING

BYGGHANDLING

DATUM 2025-01-31 FÖRORDNING T. BERGSTRÖM ANFÖRANDE PM KFU01

REVISOR



PROJEKTNAMN

ROBERTSFORS KOMMUN

PROJEKTNUMMER

YTTRE RINGVÄGEN 4

DIARIENUMMER

FORDONET 1

DISCIPLIN

NORCONSULT SVERIGE AB

UPPDRAGSRUMMER

108 83 71

TELEFON

010 141 80 00

BYGGNADSRUMMER

+44.60, +45.07, +45.54 (FG)

VÄRNINGSPÅN

1

DEL 4, 5

SYSTEM

40 SAMMANSATT REDOVISNING

SPECIFIKATION

PLAN 1 - ÖVERSIKT, BRAND

BYGGNADSRUMMER

PLAN

A-40-1-100

SKALA

1:100

FORMAT

A1

ANVÄNDNING

A

FLN:AMN: C:\Norconsult\Autodesk\Revit\1088371-Centralkök Robertsfors_Centraltrifli-2024_mastia.rvt



PLAN 1
1 : 100

SKALA 1:100 0 1 10 METER