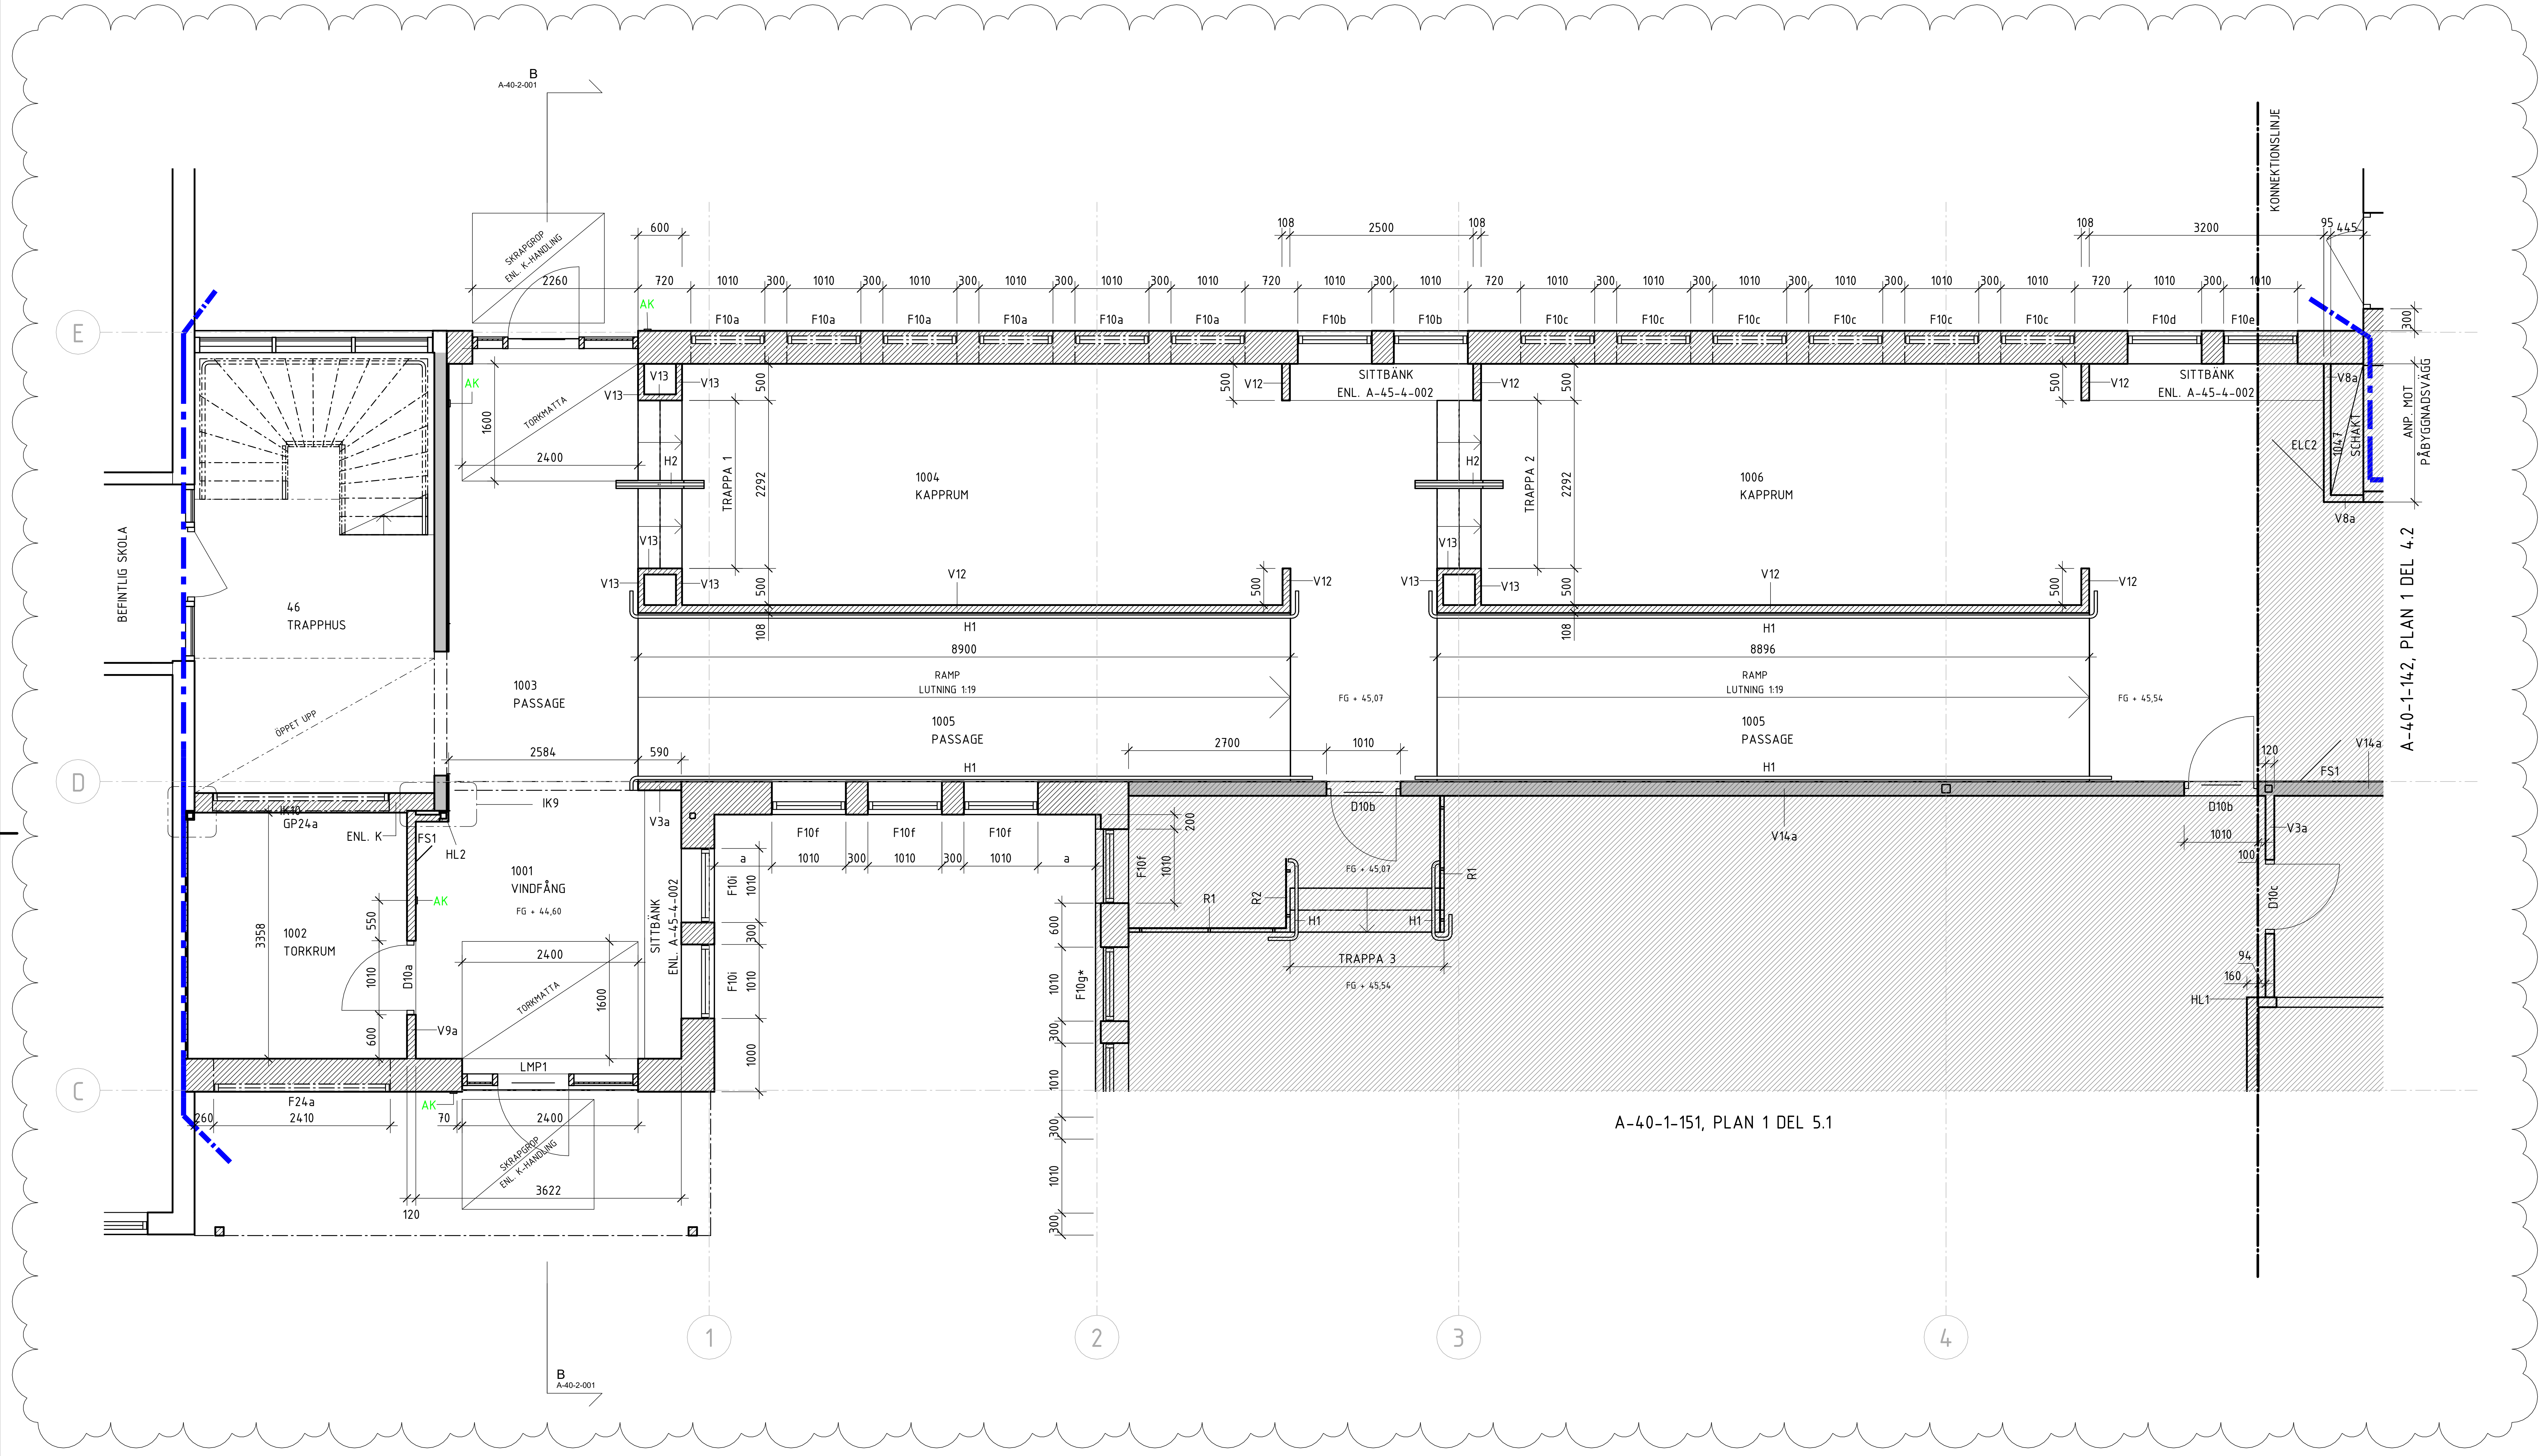
B
A-40-2-001
SKRAPGROP ENL. K-HANDLING
2260
600
720
1010
300
108
2500
3200
95
445
KONNEKTIONSLINJE
F10a
F10b
F10c
F10d
F10e
F10f
F10g*
F10i
AK
E
D
C
1
2
3
4
46
TRAPPHUS
BEFINTLIG SKOLA
ÖPPET UPP
TORKMATTA
1600
2400
1003
PASSAGE
2584
590
V13
V12
H1
H2
TRAPPA 1
TRAPPA 2
TRAPPA 3
2292
500
1004
KAPPRUM
1006
KAPPRUM
SITTBÄNK
ENL. A-45-4-002
8900
8896
RAMP
LUTNING 1:19
1005
PASSAGE
FG + 45,07
FG + 45,54
2700
D10b
D10c
V14a
V8a
ELC2
SCHAKT
1047
ANP. MOT PÅBYGGNADSVÄGG
300
120
FS1
V3a
100
94
160
HL1
A-40-1-142, PLAN 1 DEL 4.2
IK9
IK10
GP24a
ENL. K
HL2
1001
VINDFÅNG
FG + 44,60
1002
TORKRUM
3358
550
600
D10a
V9a
LMP1
F24a
260
2410
70
3622
1000
200
a
R1
R2
A-40-1-151, PLAN 1 DEL 5.1

FÖRKLARINGAR

MÅTT ANGES I MILLIMETER DÄR EJ ANNAT ANGES.

—·—·— = BRANDCELLSGRÄNS EI30

A = VITMÅLAD SLÄTPLÅT.
LÄNGD ANP. SÅ 50mm INFÄSTNINGNSYTA PÅ
VARDERA SIDA ERHÅLLS, HÖJD LIKA KYL-/FRYSRUM

FS1 = FÖRDELARSKÅP GOLVVÄRME ENL. VS

FS2 = FÖRDELARSKÅP FÖR TAPPVATTEN ENL. VS

AK = ARMBÅGSKONTAKT

KL = KORTLÄSARE

ÖK = ÖPPNAKNAPP

HL1 = HÖRNLIST ROSTFRI ENLIGT BESKRIVNING
HL2 = HÖRNLIST PLAST ENLIGT BESKRIVNING

H1,H2=HANDLEDARE &
R1,R2=RÄCKE SE A-45-4-001

ILx = LÅSBAR INSPEKTIONSLUCKA TYP GYPROC INEO,
INFÄSTNING ENL. LEVERANTÖRENS ANVISNINGAR.
STORLEK ENL. RESP. LITTRA
IL1: 150x150mm, 500mm ÖFG
IL2: 400x400mm, 500mm ÖFG

☐ = BEFINTLIG VÄGG

■ = BÄRANDE INNERVÄGG ENL. K

▩ = KYL-/FRYSRUMSVÄGG

▨ = NY INNERVÄGG ENL. LITTERA
VX

HÄNVISNINGAR

FÖNSTER	A-42-4-001
LÄTTMETALLPARTIER	A-42-4-002
STÅLDÖRRAR	A-42-4-021
INNERDÖRRAR AV TRÄ	A-43-4-011
INVÄNDIGA GLASPARTIER	A-43-4-012
INVÄNDIGA GLASFIBERDÖRRAR	A-43-4-031
ELCENTRALFRONTER	A-43-4-041
INNNERVÄGGSTYPER	A-43-5-001 --002
INVÄNDIGA DETALJER	A-43-6-001 --003
TRAPPA, HANDLEDARE, RÄCKE	A-45-4-001
KONSTRUKTIONSRITNINGAR	

RITNING KRÄVER FÄRGUTSKRIFT FÖR KORREKT UTSEENDE

SEKTION

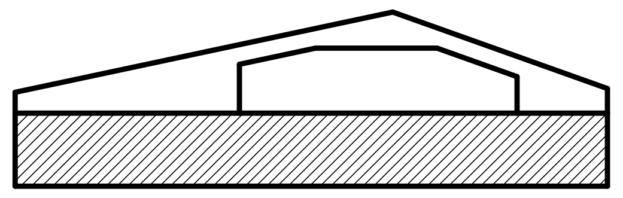

ORIENTERINGSFIGUR

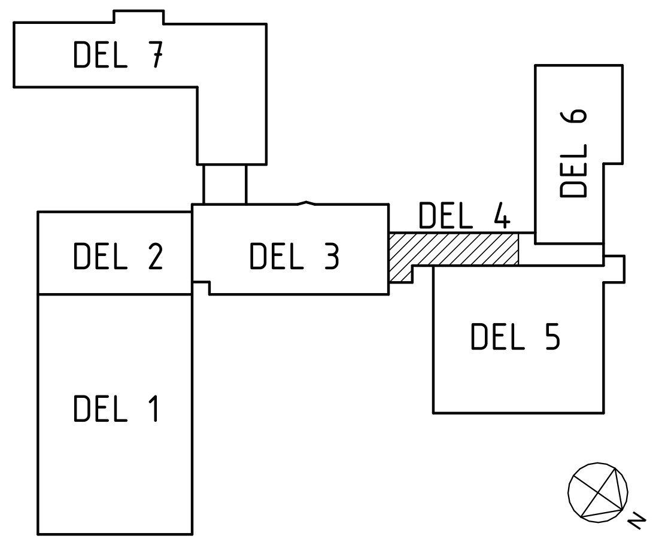
DEL 7
DEL 6
DEL 4
DEL 2
DEL 3
DEL 5
DEL 1
N

STATUS
FÖRFRÅGNINGSUNDERLAG
HANDLING
BYGGHANDLING
DATUM 2025-01-31
GODKÄND AV T. BERGSTRÖM
ÄNDRINGS PM KFU01
BESTÄLLARE
ROBERTSFORS KOMMUN
PROJEKTNAMN
CENTRALKÖK
OMRÅDE
ROBERTSFORS KOMMUN
PROJEKTNUMMER
ADRESS YTTRE RINGVÄGEN 4
DIARIENUMMER
FASTIGHET FORDONET 1
DISCIPLIN A
FÖRETAG NORCONSULT SVERIGE AB
UPPDRAGSNUMMER 108 83 71
SKAPAD AV SBS
TELEFON 010 141 80 00
KONTAKTPERSON TOMAS BERGSTRÖM
BYGGNADSVERK
PLUSHÖJD (RH 2000) +44.60, +45.07, +45.54 (FG)
VÅNINGSPLAN 1
VÅNINGSDEL
DELOMRÅDE DEL 4.1
SYSTEM
40 SAMMANSATT REDOVISNING
SPECIFIKATION
PLAN 1, DEL 4.1
RITNINGSKATEGORI PLAN
SKALA 1:50
FORMAT A1
DOKUMENTNUMMER A-40-1-141
ÄNDRING A

SKALA 1:50 0 1 5 METER

2025-01-31 14:13:50

FILNAMN: C:\Norconsult\Autodesk\Revit\1088371-Centralkök Robertsfors_centralfil-2024_matsta.rvt