

MÅTT ANGES I MILLIMETER DÄR EJ ANNAT ANGES.

===== BRANDCELLSGRÄNS EI30

LÄNGD ANP. SÅ 50mm INFÄSTNINGEN SYTA PÅ
VARDERA SIDA ERHÅLLS, HÖJD LIKA KYL-/FRYSRUM

FS1 = FÖRDELARSKÅP GOLVVÄRME ENL. VS

FS2 = FÖRDELARSKÅP FÖR TAPPVATTEN ENL. VS

AK = ARMBÅGSKONTAKT

KL = KORTLÄSARE

ÖK = ÖPPNAKNAPP

HL1 = HÖRNLIST ROSTFRI ENLIGT BESKRIVNING
HL2 = HÖRNLIST PLAST ENLIGT BESKRIVNING

H1,H2=HANDLEDARE &
R1,R2=RÄCKE SE A-45-4-001

Lx = LÅSBAR INSPEKTIONSLUCKA TYP GYPROC INEO,
INFÄSTNING ENL. LEVERANTÖRENS ANVISNINGAR.
STORLEK ENL. RESP. LITTRA
IL1: 150x150mm, 500mm ÖFG
IL2: 400x400mm, 500mm ÖFG

☐ = BEFINTLIG VÄGG

 = BÄRANDE INNERVÄGG ENL. K



 = KYL-/FRYSRUMSVÄGG

 = NY INNERVÄGG ENL. LITTERA

 $\nabla \wedge$

FRONTER	A-42-4-001
ÄTTMETALLPARTIER	A-42-4-002
STÅLDÖRRAR	A-42-4-021
INNERDÖRRAR AV TRÄ	A-43-4-011
NVÄNDIGA GLASPARTIER	A-43-4-012
NVÄNDIGA GLASFIBERDÖRRAR	A-43-4-031
ELECENTRALFRONTER	A-43-4-041
NNERNVÄGGSTYPER	A-43-5-001 --002
NVÄNDIGA DETALJER	A-43-6-001 --003
TRAPPA, HANDLEDDAR, RÄCKE	A-45-4-001
KONSTRUKTIONSRITNINGAR	

RITNING KRÄVER FÄRGUTSKRIFT FÖR KORREKT UTSEENDE

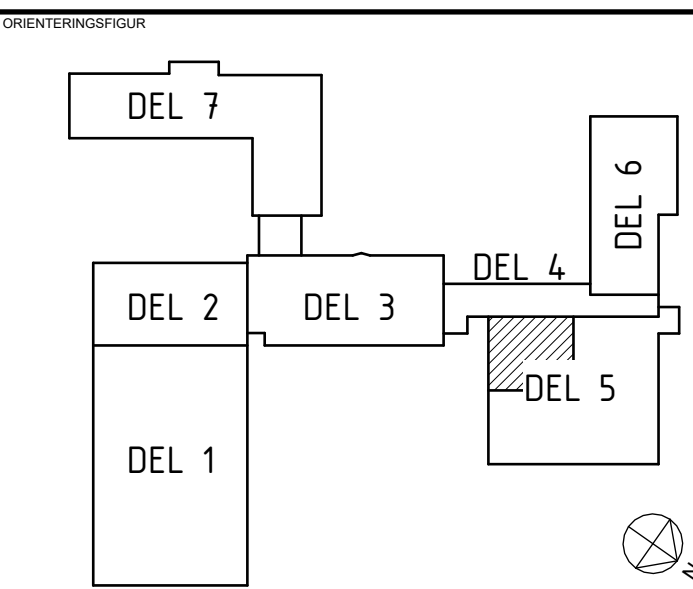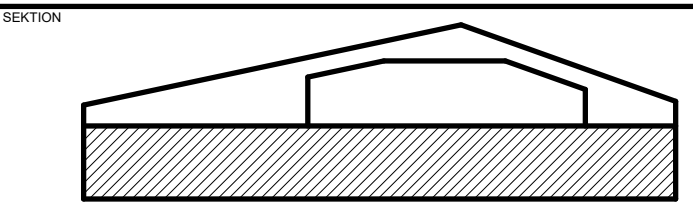

STATUS

BYGGHANDLING

DATUM	GODKÄND AV	ÄNDRING
2025-01-31	T. BERGSTRÖM	KFU

BESTALLARE



PROJEKTNAMN

CENTRAALKÖK

ROBERTSFORS KOMMUN

PROJEKTNUMMER	ADRESS
	YTTRE RINGVÄGEN 4

DIARIENUMMER	FASTIGHET FORDONET 1
--------------	-------------------------

DISCIPLIN	FORETAG
A	NORCONSULT SVERIGE

UPPGIFTSNUMMER	SKAPAD AV
108 83 71	SBS
REVISOR	KONTROLLERAD AV

TELEFON	KONTAKTPERSON
010 141 80 00	TOMAS BERGSTRÖM
RYGGMÄNNUERIK	BLISSHÖJD (Bh 2020)

		Förändring (rel 2010)
		+45.07, +45.54 (FG)
VÄRDESKILLNAD	VÄRDESKILLNAD	DEL OMRÅDE

1		DEL 5.1
---	--	---------


SYSTEM

40 SAMMANSATT REDOVISNING

PLAN 1, DEL 5.1		
RITNINGSKATEGORI	SKALA	FORMAT

PLAN	1:50	A1
DOKUMENTNUMMER		ÄNDRING

A-40-1-151	A
------------	---

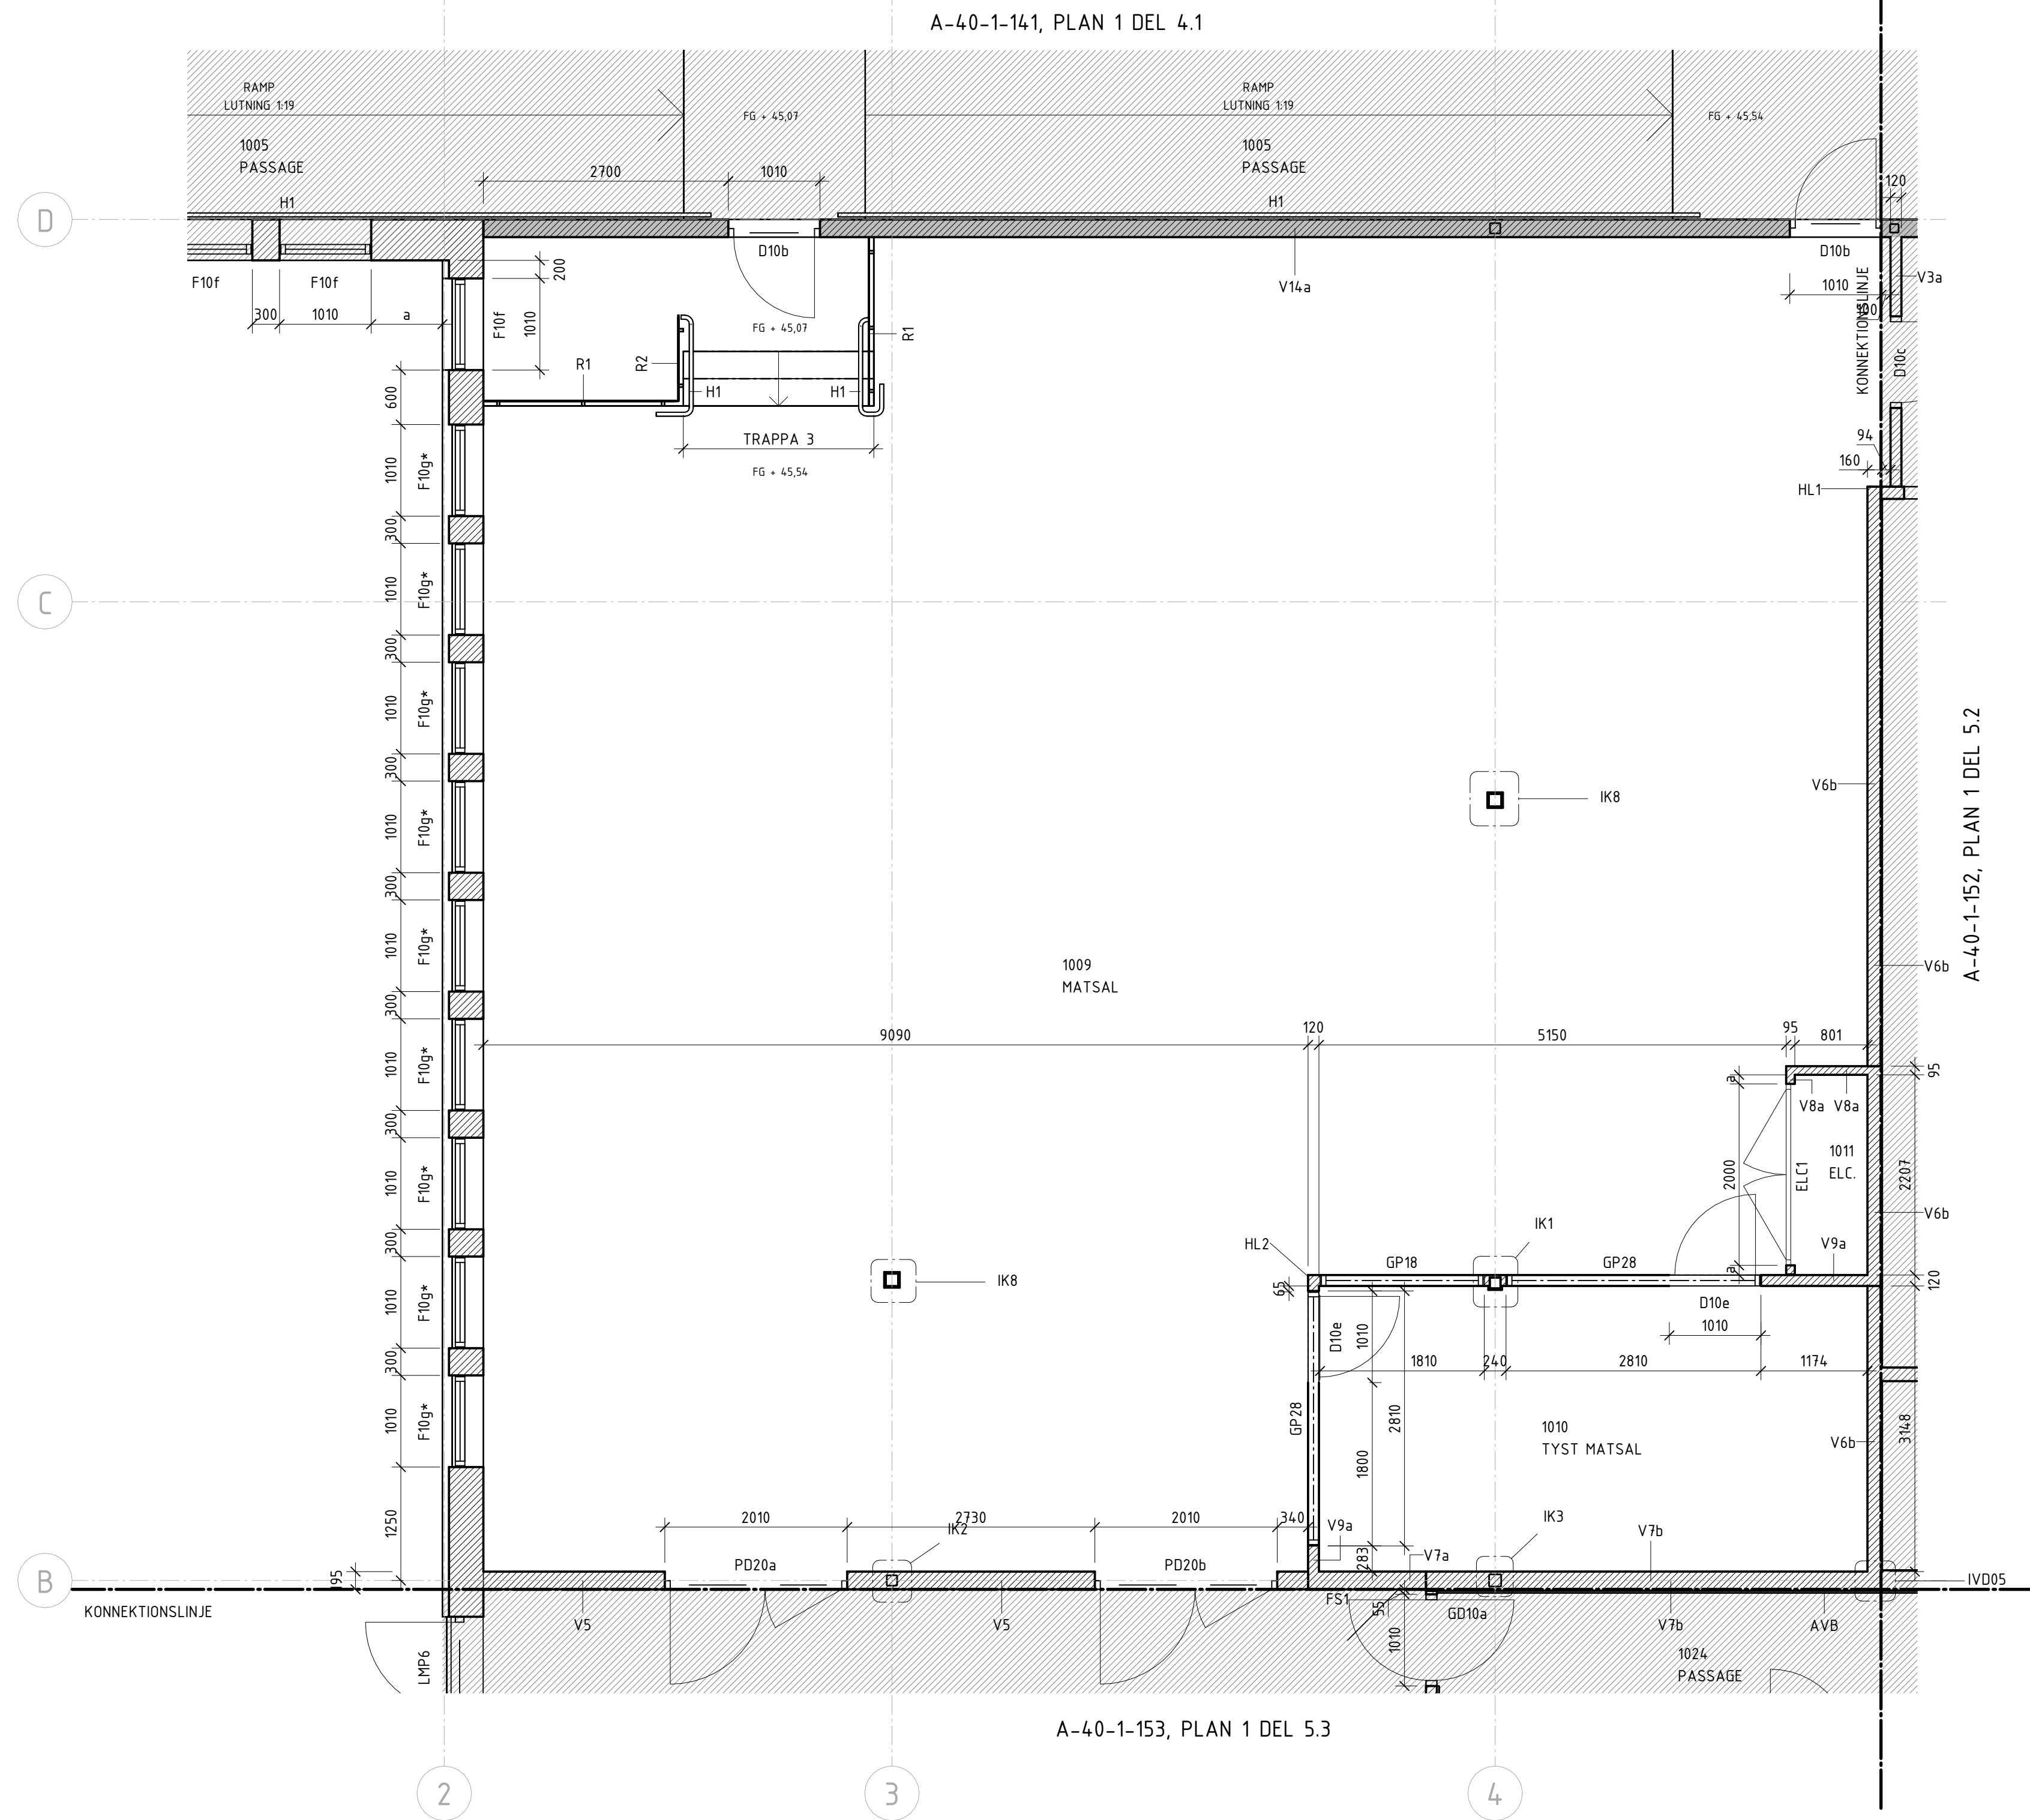

SKALA 1:50 0 1 5 METER