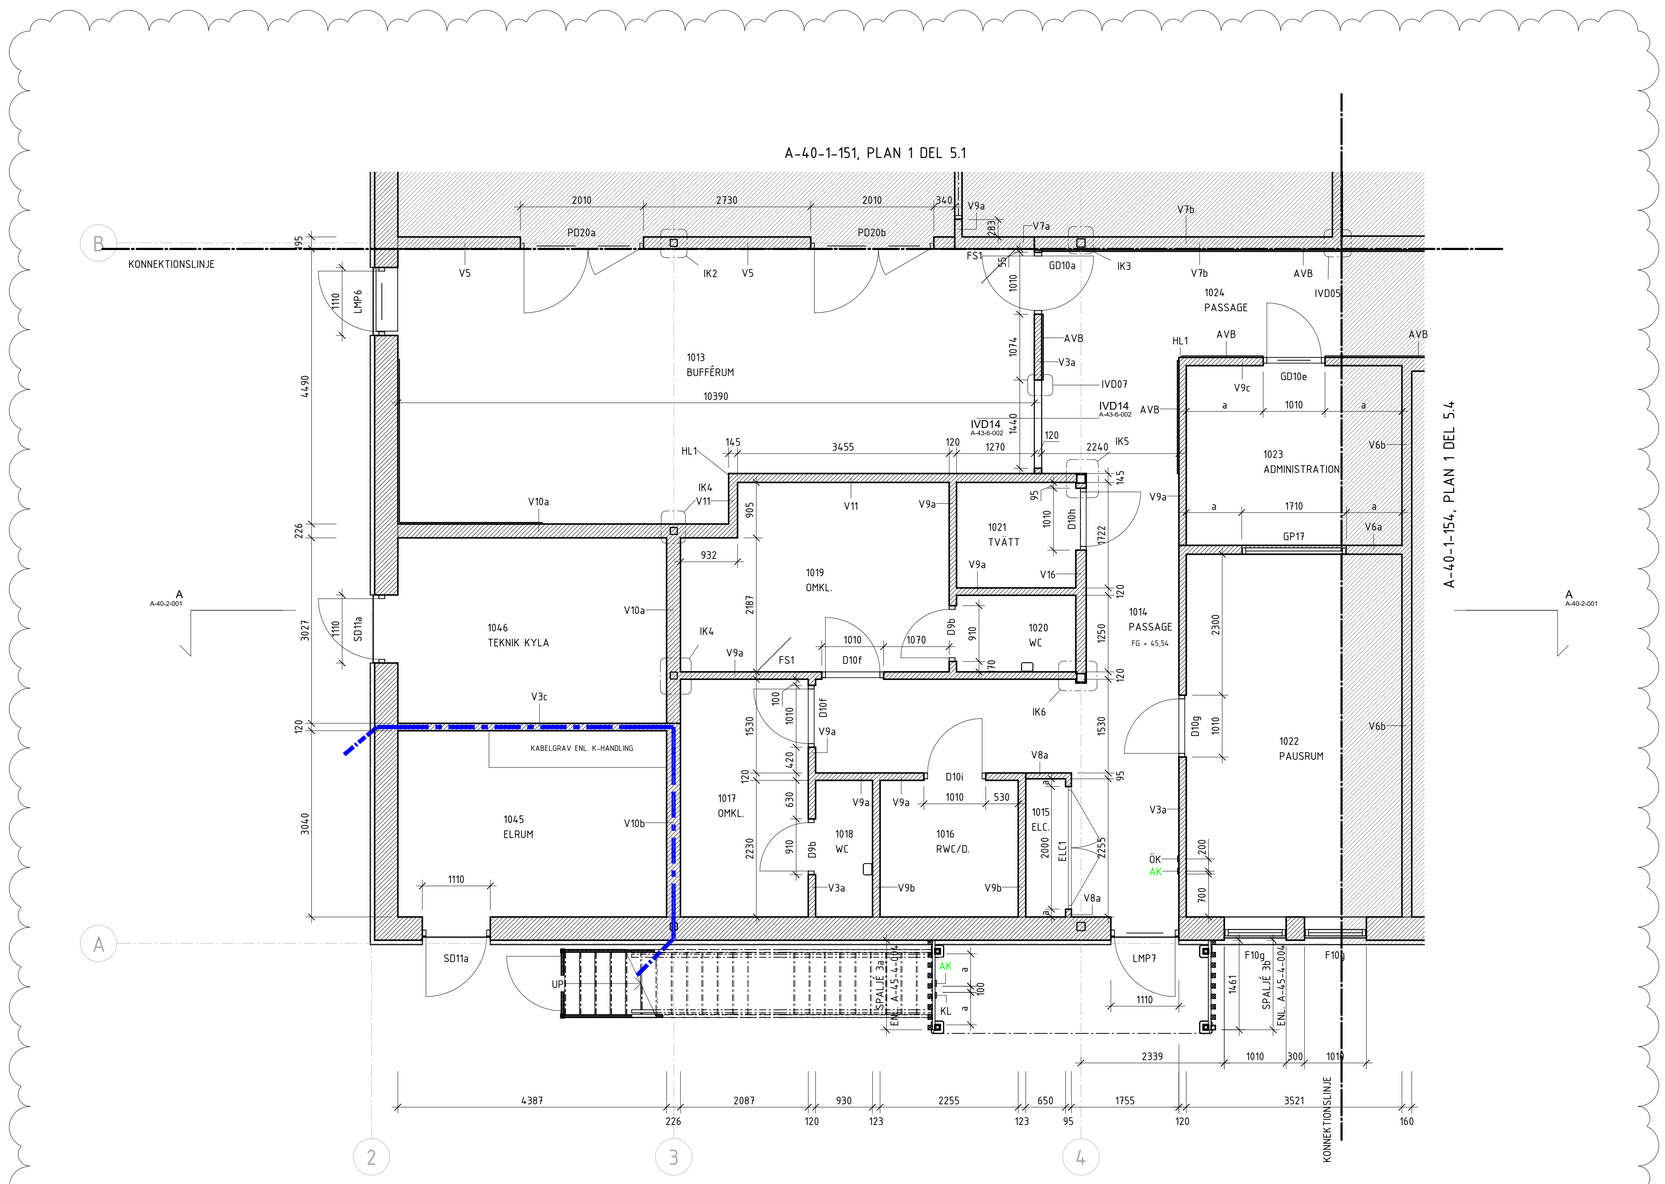

SKALA 1:50 0 1 5 METER

FÖRKLARINGAR

MÅTT ANGES I MILLIMETER DÄR EJ ANNAT ANGES.

= BRANDCELLSGRÄNS EI30

A = VITMÅLAD SLÄTPLÅT.
LÄNGD ANP. SÅ 50mm INFÄSTNINGNSYTA PÅ VARDERA SIDA ERHÅLLS, HÖJD LIKA KYL-/FRYSRUM

FS1 = FÖRDELARSKÅP GOLVVÄRME ENL. VS

FS2 = FÖRDELARSKÅP FÖR TAPPVATTEN ENL. VS

AK = ARMBÅGSKONTAKT

KL = KORTLÄSARE

ÖK = ÖPPNAKNAPP

HL1 = HÖRNLIST ROSTFRI ENLIGT BESKRIVNING
HL2 = HÖRNLIST PLAST ENLIGT BESKRIVNING

H1,H2=HANDLEDARE &
R1,R2=RÄCKE SE A-45-4-001

ILx = LÅSBAR INSPEKTIONSLUCKA TYP GYPROC INEO, INFÄSTNING ENL. LEVERANTÖRENS ANVISNINGAR.
STORLEK ENL. RESP. LITTRA
IL1: 150x150mm, 500mm ÖFG
IL2: 400x400mm, 500mm ÖFG

= BEFINTLIG VÄGG

= BÄRANDE INNERVÄGG ENL. K

= KYL-/FRYSRUMSVÄGG

= NY INNERVÄGG ENL. LITTERA VX

HÄNVISNINGAR

FÖNSTER	A-42-4-001
LÄTTMETALLPARTIER	A-42-4-002
STÅLDÖRRAR	A-42-4-021
INNERDÖRRAR AV TRÄ	A-43-4-011
INVÄNDIGA GLASPARTIER	A-43-4-012
INVÄNDIGA GLASFIBERDÖRRAR	A-43-4-031
ELCENTRALFRONTER	A-43-4-041
INNNERVÄGGSTYPER	A-43-5-001 --002
INVÄNDIGA DETALJER	A-43-6-001 --003
TRAPPA, HANDLEDARE, RÄCKE	A-45-4-001
KONSTRUKTIONSRITNINGAR	

RITNING KRÄVER FÄRGUTSKRIFT FÖR KORREKT UTSEENDE

SEKTION

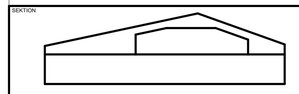

ORIENTERINGSFIGUR

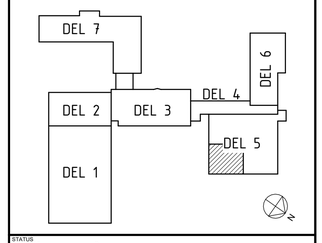

STATUS: FÖRFRÅGNINGSUNDERLAG
HANDLING: BYGGHANDLING

DATUM	GODKÄND AV	ÄNDRINGS PM
2025-01-31	T. BERGSTRÖM	KFU01

BESTÄLLARE: ROBERTSFORS KOMMUN

PROJEKTNAMN: CENTRALKÖK
OMRÅDE: ROBERTSFORS KOMMUN

PROJEKTNUMMER	ADRESS: YTTRE RINGVÄGEN 4
DIARIENUMMER	FASTIGHET: FORDONET 1
DISCIPLIN: A	FÖRETAG: NORCONSULT SVERIGE AB
UPPDRAGSNUMMER: 108 83 71	SKAPAD AV: SBS
TELEFON: 010 141 80 00	KONTAKTPERSON: TOMAS BERGSTRÖM
BYGGNADSVERK	PLUSHÖJD (RH 2000): +45,54 (FG)
VÅNINGSPLAN: 1 / VÅNINGSDEL	DELOMRÅDE: DEL 5.3
SYSTEM: 40 SAMMANSATT REDOVISNING	
SPECIFIKATION: PLAN 1, DEL 5.3	
RITNINGSKATEGORI: PLAN	SKALA: 1:50 / FORMAT: A1
DOKUMENTNUMMER: A-40-1-153	ÄNDRING: A

2025-01-31 14:14:02

FILNAMN: C:\Norconsult\Autodesk\Revit\108371-Centralkök Robertsfors_centralfil-2024_matsta.rvt