

FÖRKLARINGAR

MÅTT ANGES I MILLIMETER DÄR EJ ANNAT ANGES.

= BRANDCELLSGRÄNS EI30

A = VITMÅLAD SLÄTPLÅT.
LÄNGD ANP. SÅ 50mm INFÄSTNINGSYTA PÅ
VARDERA SIDA ERHÅLLS, HÖJD LIKA KYL-/FRYSRUM

FS1 = FÖRDELARSKÅP GOLVVÄRME ENL. VS

FS2 = FÖRDELARSKÅP FÖR TAPPVATTEN ENL. VS

AK = ARMBÅGSKONTAKT

KL = KORTLÄSARE

ÖK = ÖPPNAKNAPP

HL1 = HÖRNLIST ROSTFRI ENLIGT BESKRIVNING

HL2 = HÖRNLIST PLAST ENLIGT BESKRIVNING

H1,H2=HANDLEDARE &
R1,R2=RÄCKE SE A-45-4-001

ILx = LÅSBAR INSPEKTIONSLUCKA TYP GYPROC INEO,
INFÄSTNING ENL. LEVERANTÖRENS ANVISNINGAR.
STORLEK ENL. RESP. LITTRA
IL1: 150x150mm, 500mm ÖFG
IL2: 400x400mm, 500mm ÖFG

= BEFINTLIG VÄGG

= BÄRANDE INNERVÄGG ENL. K


= KYL-/FRYSRUMSVÄGG

= NY INNERVÄGG ENL. LITTERA
VX


HÄNVISNINGAR

FÖNSTER	A-42-4-001
LÄTTMETALLPARTIER	A-42-4-002
STÅLDÖRRAR	A-42-4-021
INNERDÖRRAR AV TRÄ	A-43-4-011
INVÄNDIGA GLASPARTIER	A-43-4-012
INVÄNDIGA GLASFIBERDÖRRAR	A-43-4-031
ELCENTRALFRONTER	A-43-4-041
INNERVÄGGSTYPER	A-43-5-001 --002
INVÄNDIGA DETALJER	A-43-6-001 --003
TRAPPA, HANDLEDARE, RÄCKE	A-45-4-001
KONSTRUKTIONSRITNINGAR	

RITNING KRÄVER FÄRGUTSKRIFT FÖR KORREKT UTSEENDE

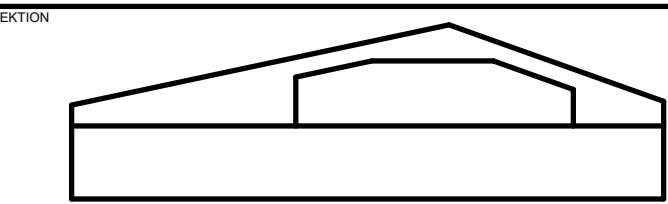

ORIENTERINGSSKISS

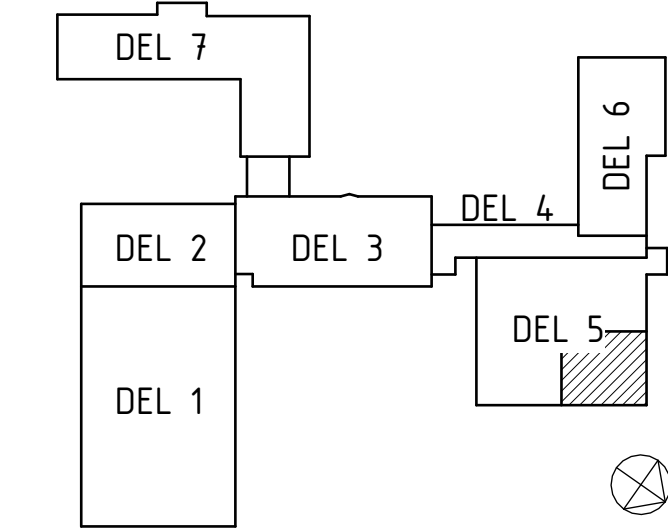

STATUS

FÖRFRÅGNINGSUNDERLAG

HANDLING

BYGGHANDLING

DATUM 2025-01-31 ÖSKAD AV T. BERGSTRÖM ANDRINGS PM KFU01

BESTÄLLARE



PROJEKTNAMN

ROBERTSFORS KOMMUN

PROJEKTNUMMER

YTTRE RINGVÄGEN 4

DIARENSNUMMER

FORDONET 1

DISCIPLIN

NORCONSULT SVERIGE AB

UPPROGGSNUMMER

108 83 71

TELEFON

010 141 80 00

BYGGGÄLDSBEHÖR

+45,54 (FG)

VÄNINGSPLAN

1

DEL 5.4

SYSTEM

40 SAMMANSATT REDOVISNING

SPECIFIKATION

PLAN 1, DEL 5.4

FORMAT

A1

SKALA

1:50


ANORDNING

A

DOCUMENTNUMMER

A-40-1-154

A-40-1-152, PLAN 1 DEL 5.2

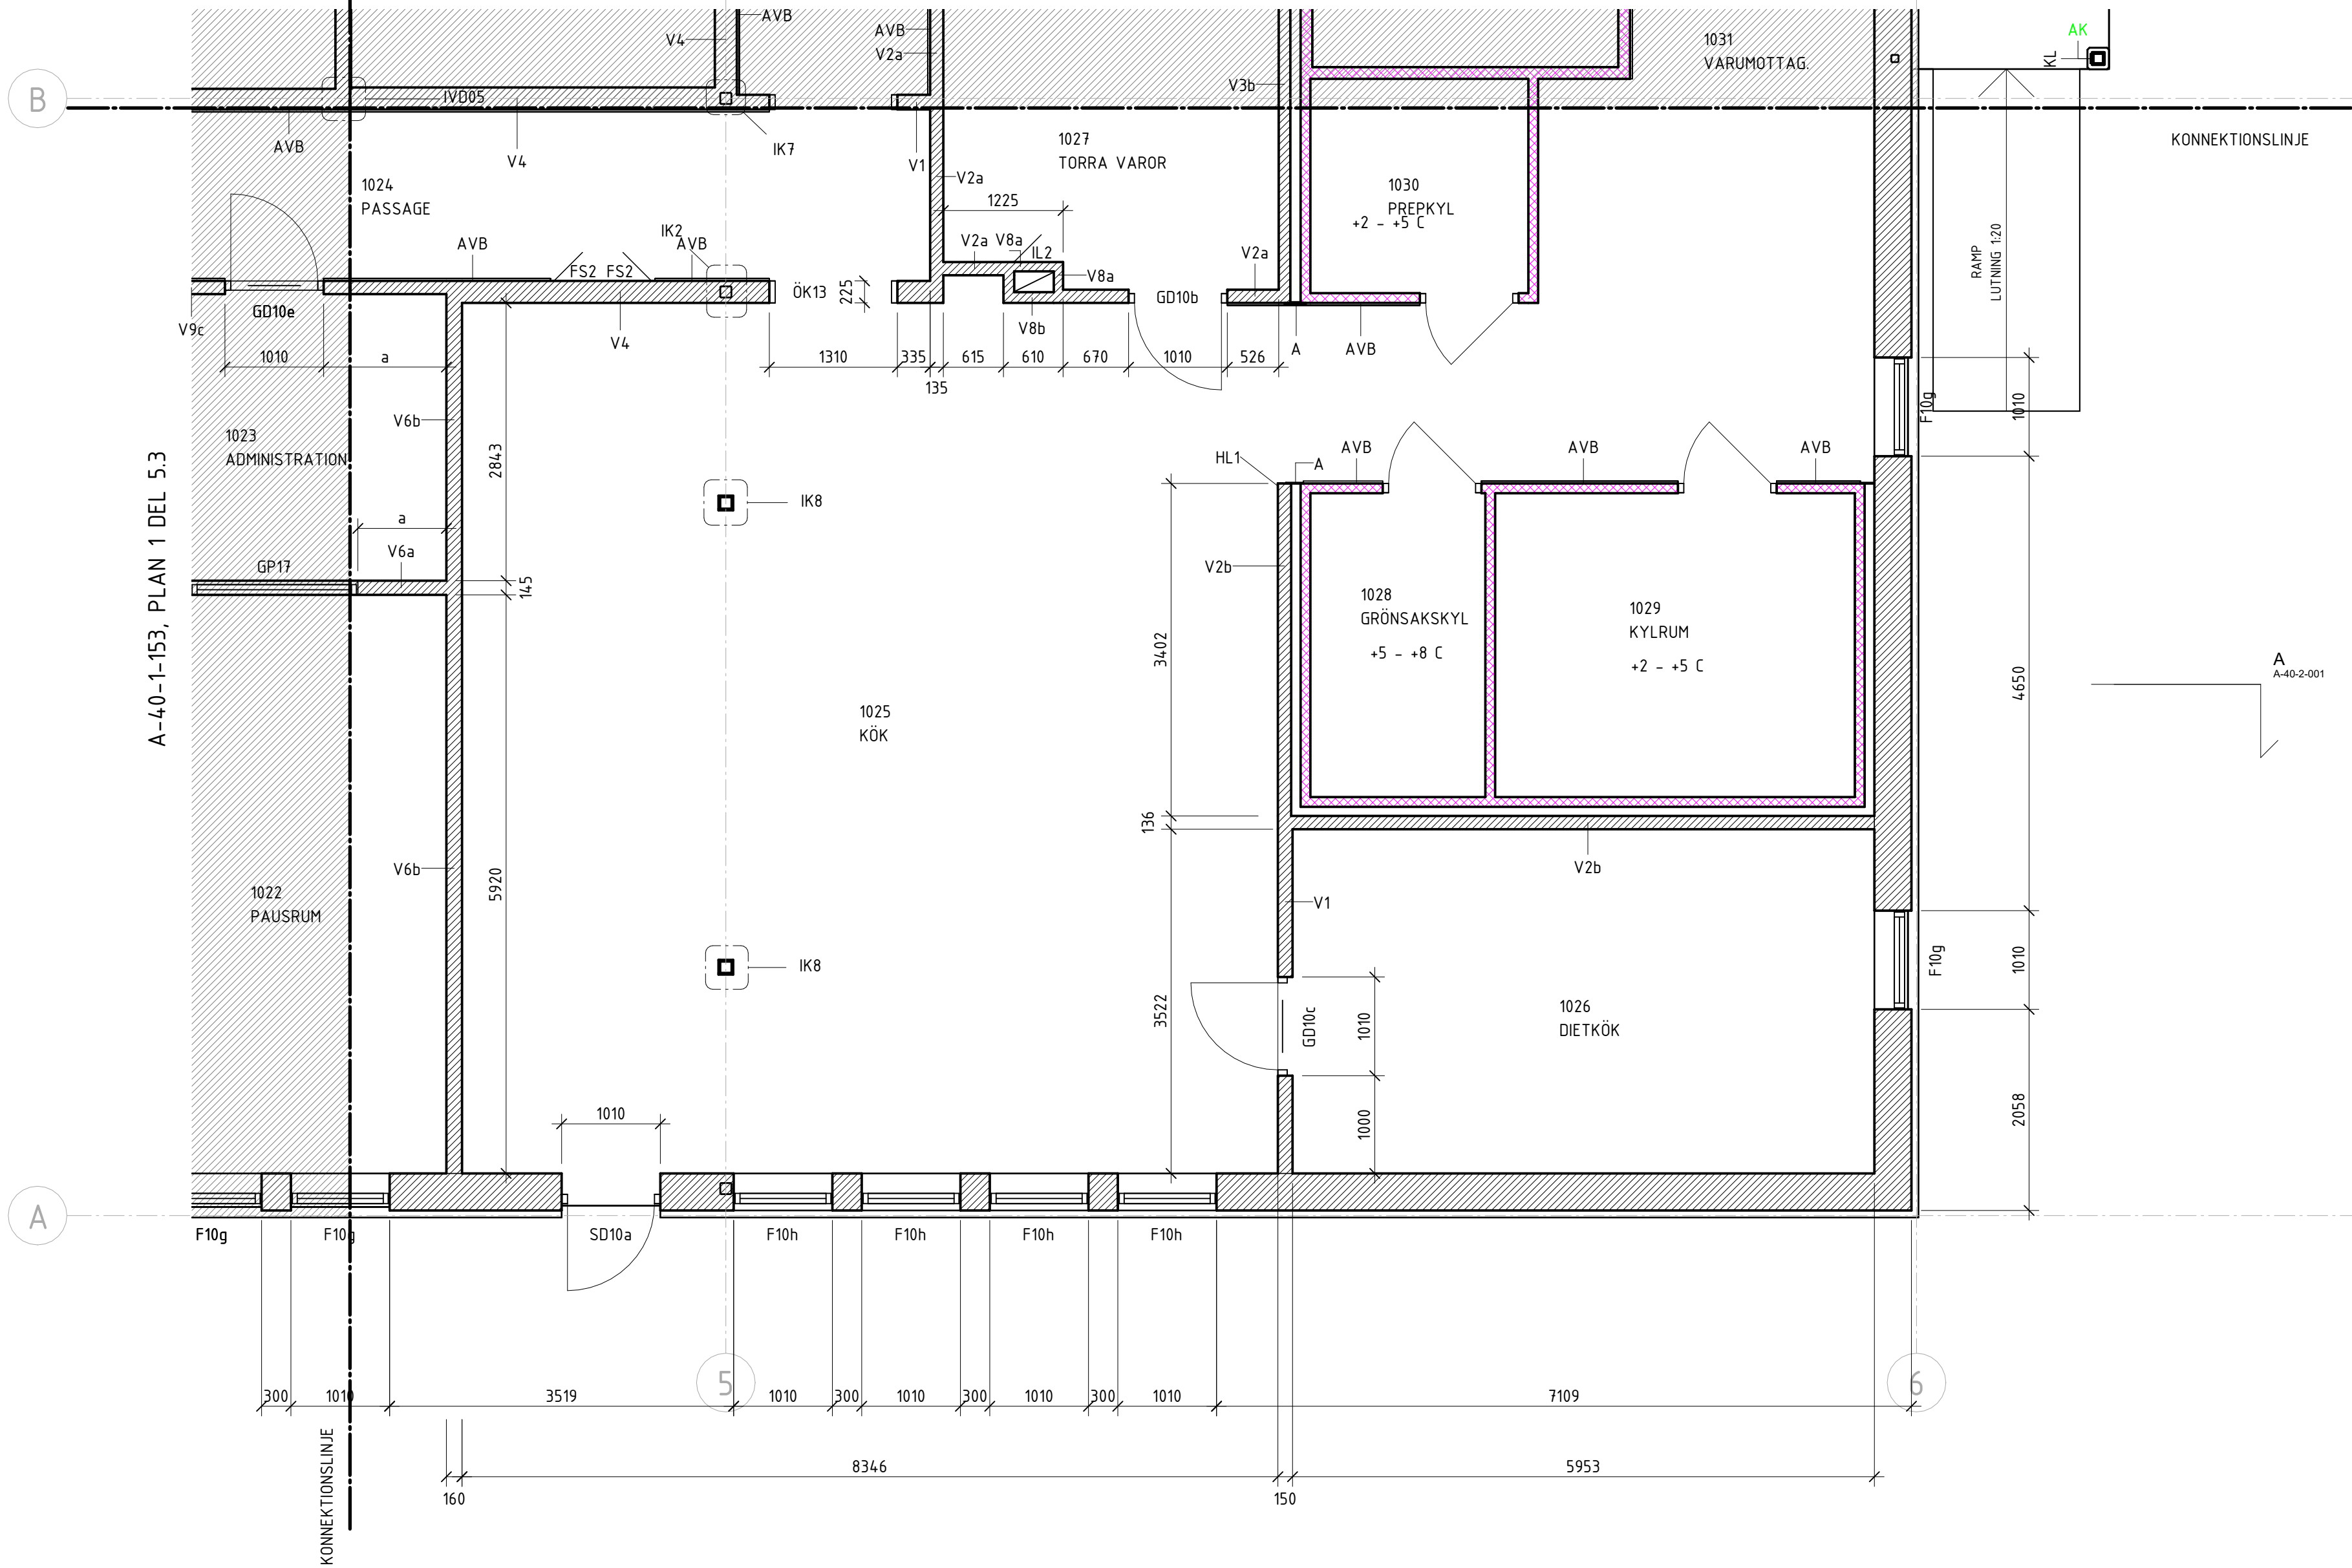

SKALA 1:50 0 1 5 METER