

MÅTT I MILLIMETER OCH PLUSHÖJDER I METER OM
INGET ANNAT ANGES.

1) SOCKEL AV BETONG

- SYNLIGA STÅPELARE & STÅLBALKAR
KULÖR RAL 7033 (DOVGRÖN), DÄR EJ ANNAT ANGES
GLANS 30

DÖRRAR MED GLAS
KULÖR RAL 7044 (SILKESGRÅ) DÄR EJ ANNAT ANGES



HÄNVISNINGAR

UTVÄNDIG TRAPPA	A-45-4-003
RAMP, LEJDARE	A-45-4-005


HÄNGRÄNNA, STUPRÖR, VINDSKIVA, VINDSKIVELIST, FOTPLÅT,
TAKFOT, GAVELSPRÅNG I PLÅT, SAMT ÖVRIGA PLÅTINKLÄDNADER
KULÖR RAL 9006 (SILVERMETALLIC)

HÖRNPLÅT ENL. K-HANDLING
KULÖR RAL 7044 (SILKESGRÅ)


FASAD MOT NORDVÄST - ENTRÉ
1 : 100

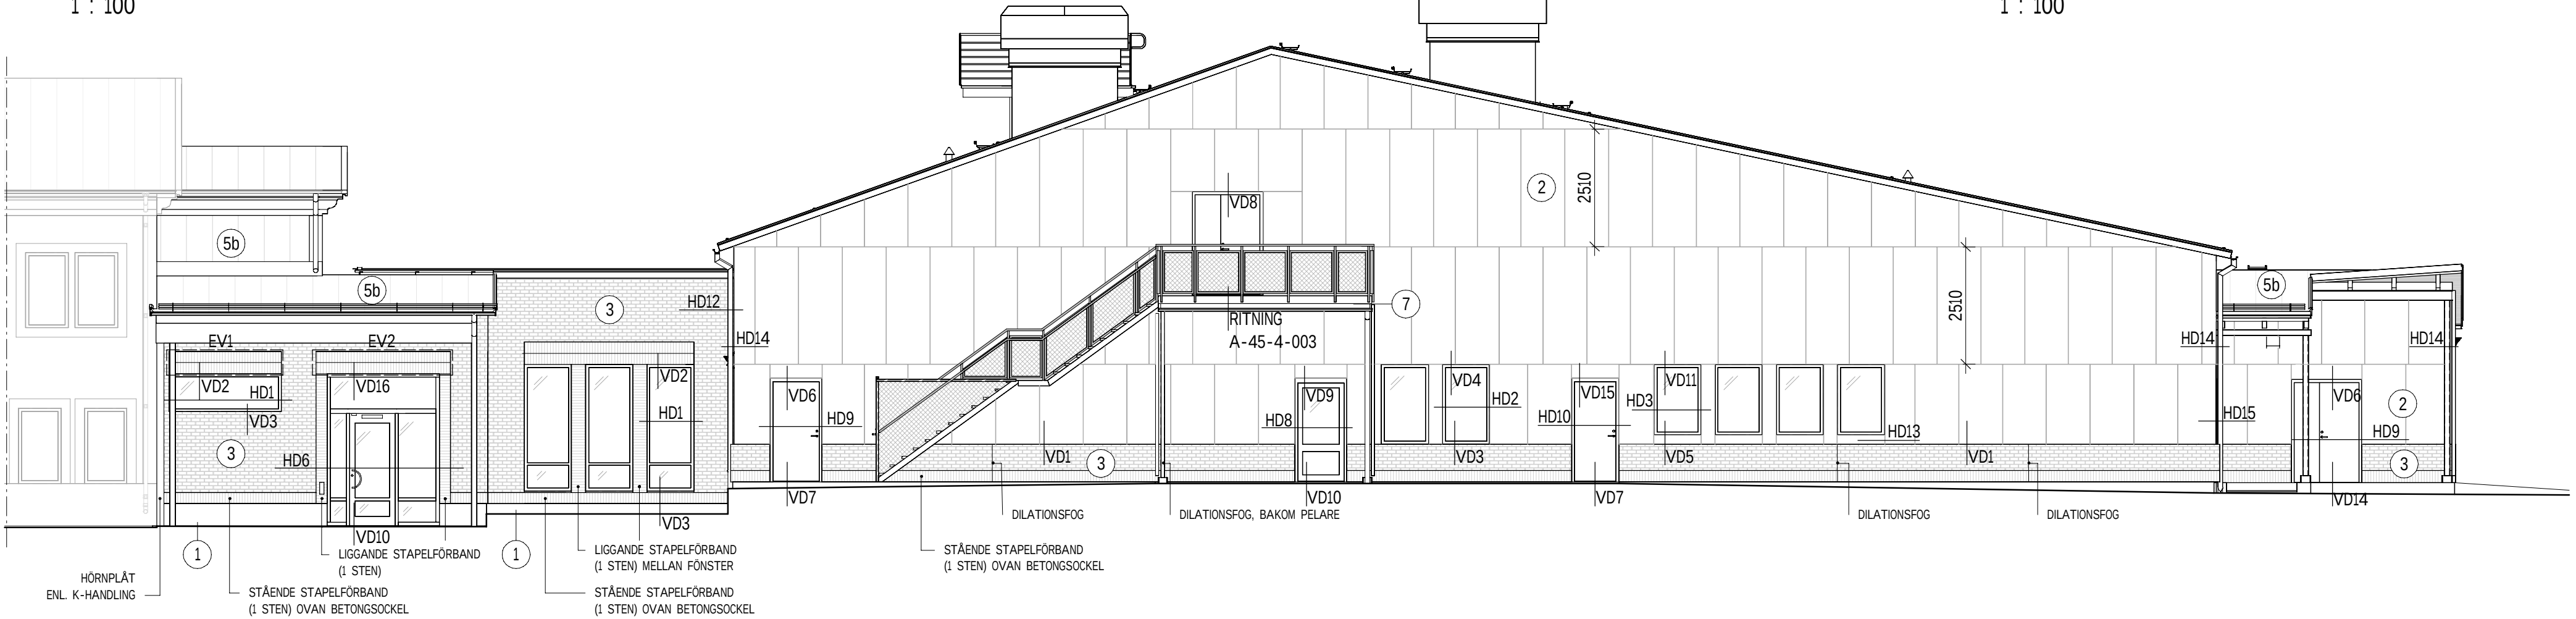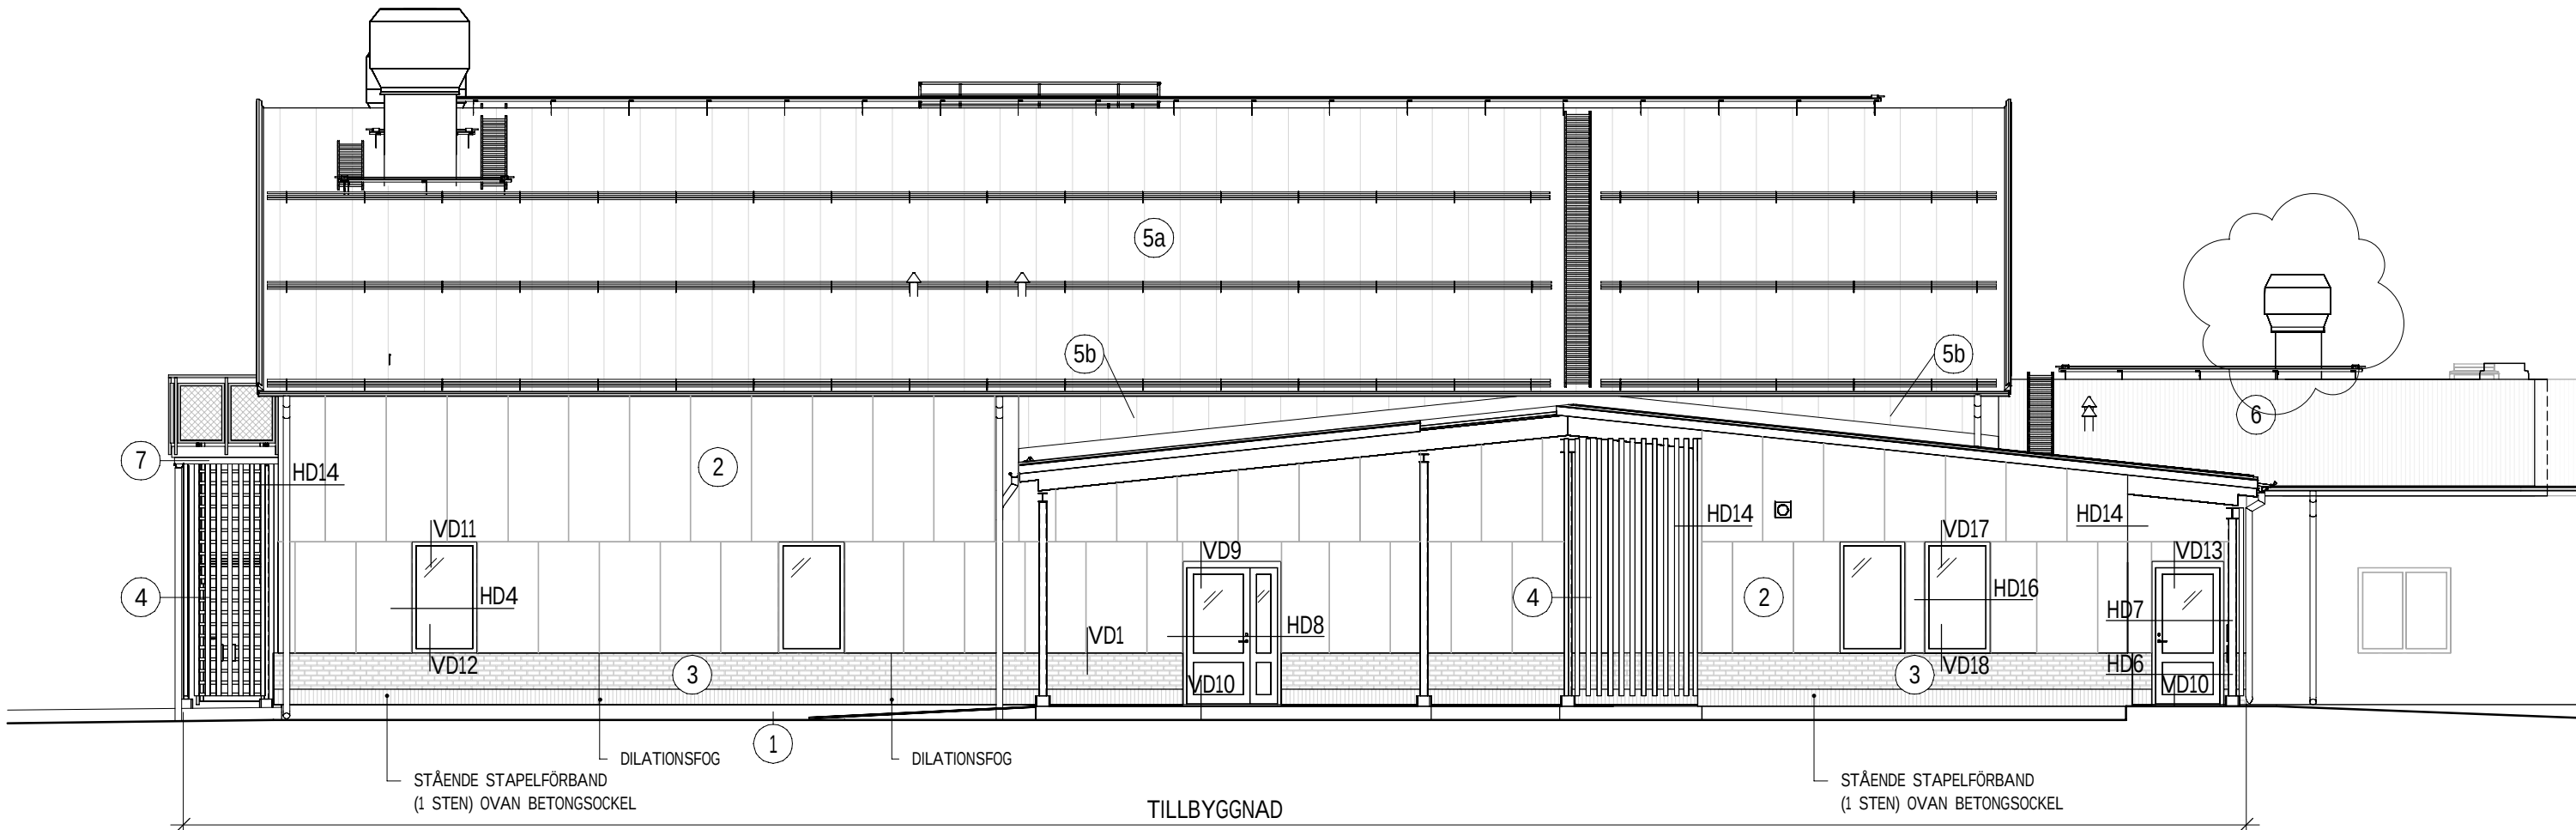

FASAD MOT NORDÖST
1 : 100


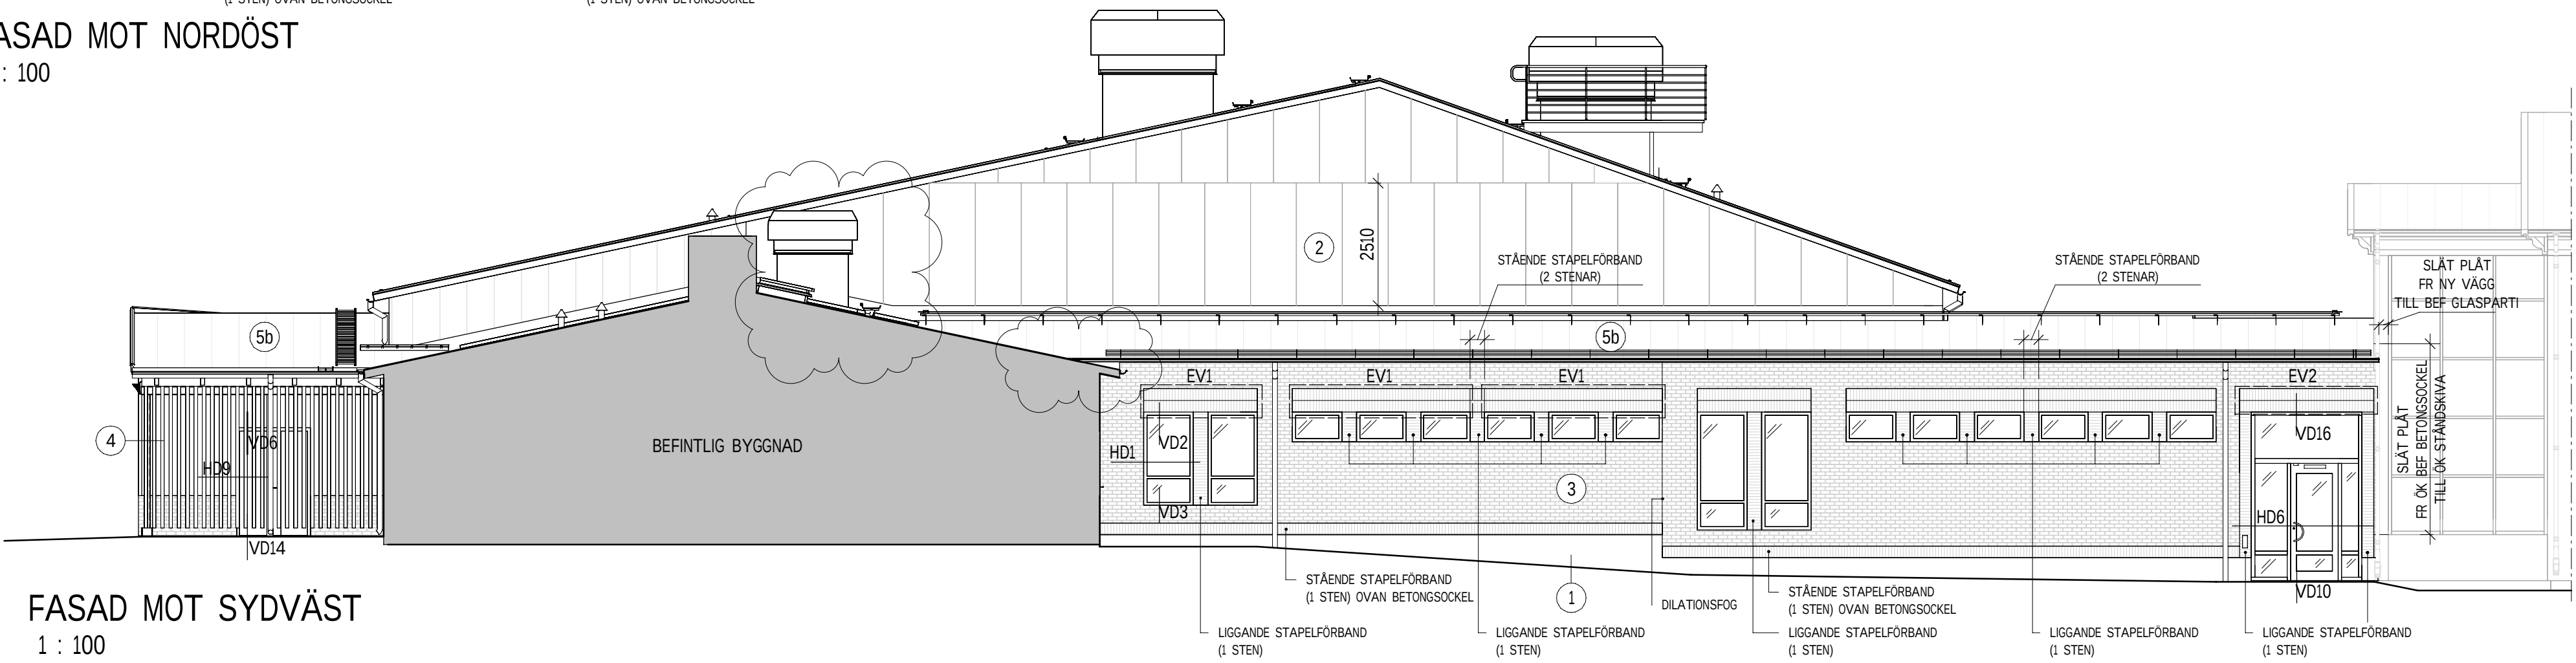


FASAD MOT SYDVÄST
1 : 100

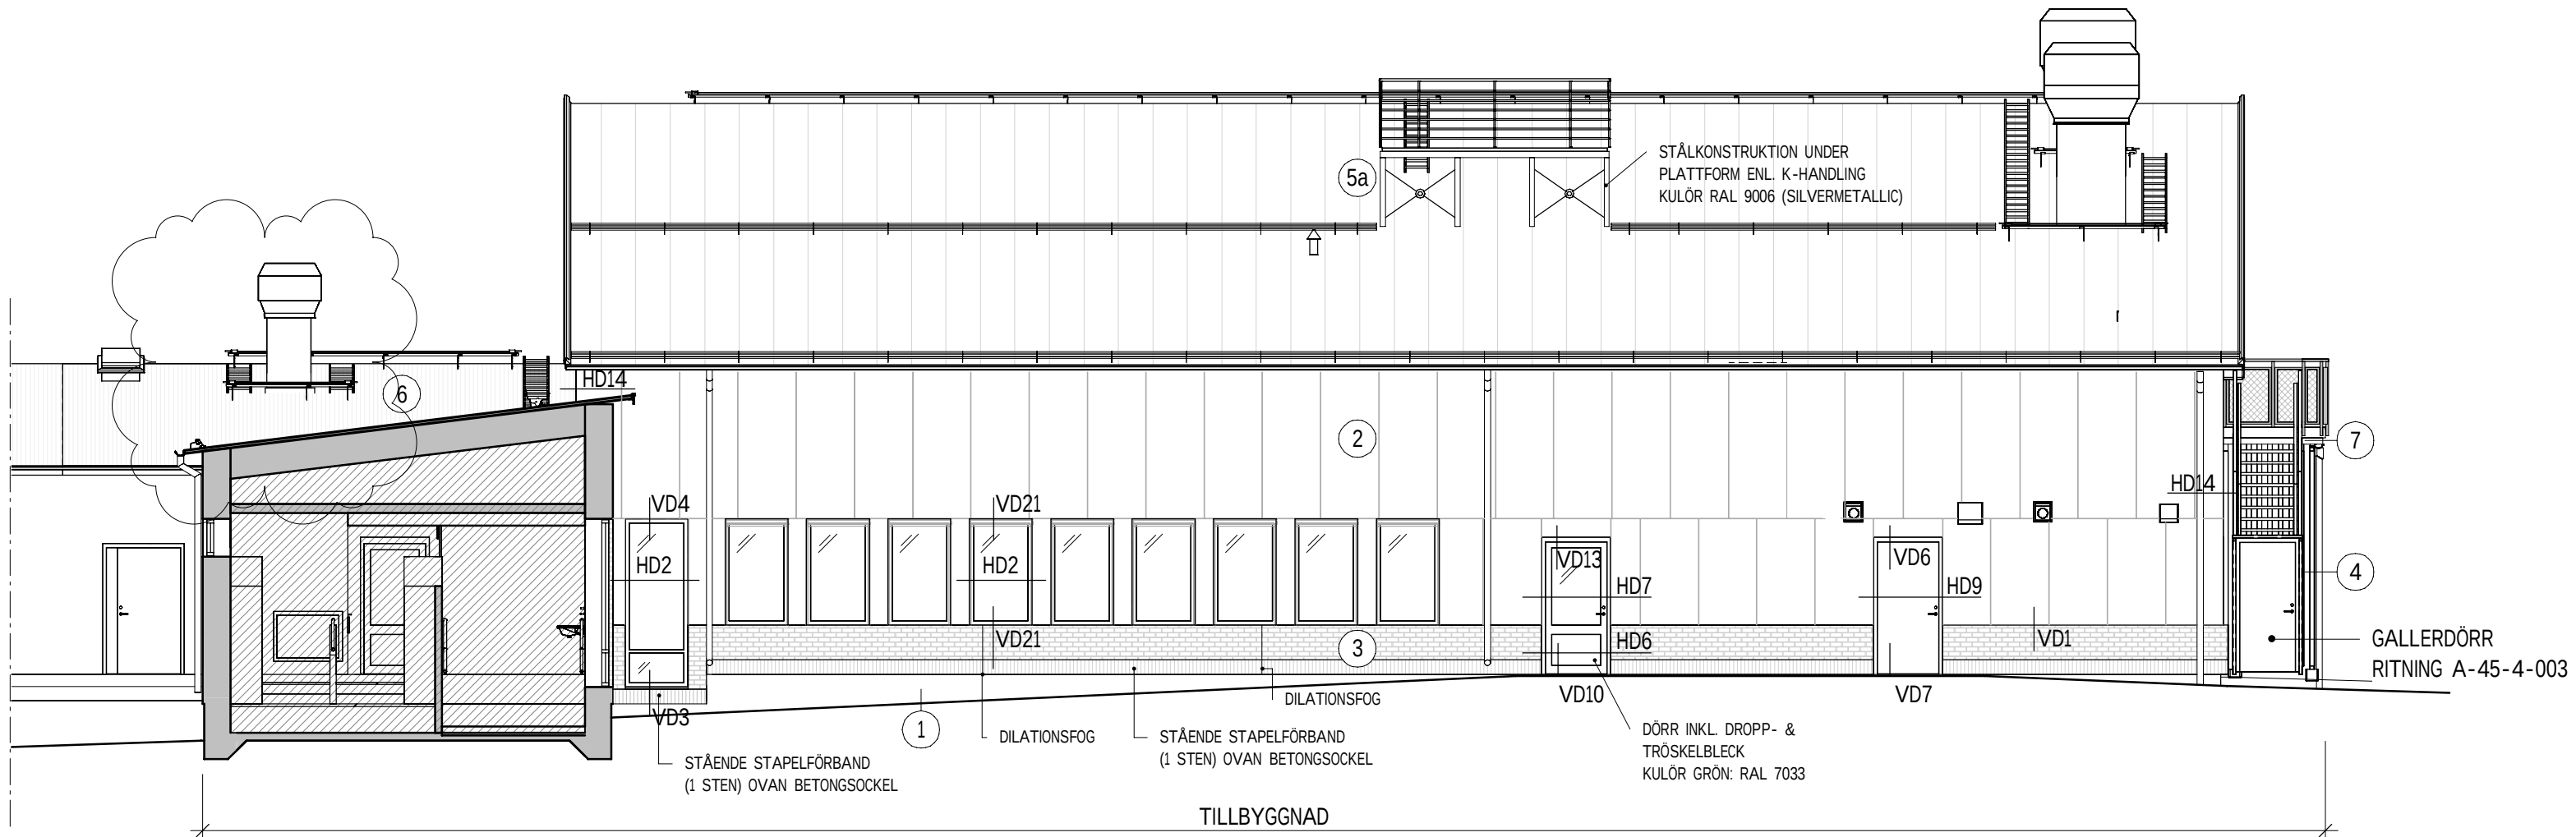

FASAD MOT SYDÖST
1 : 100

SKALA 1:100 0 1 10 METER

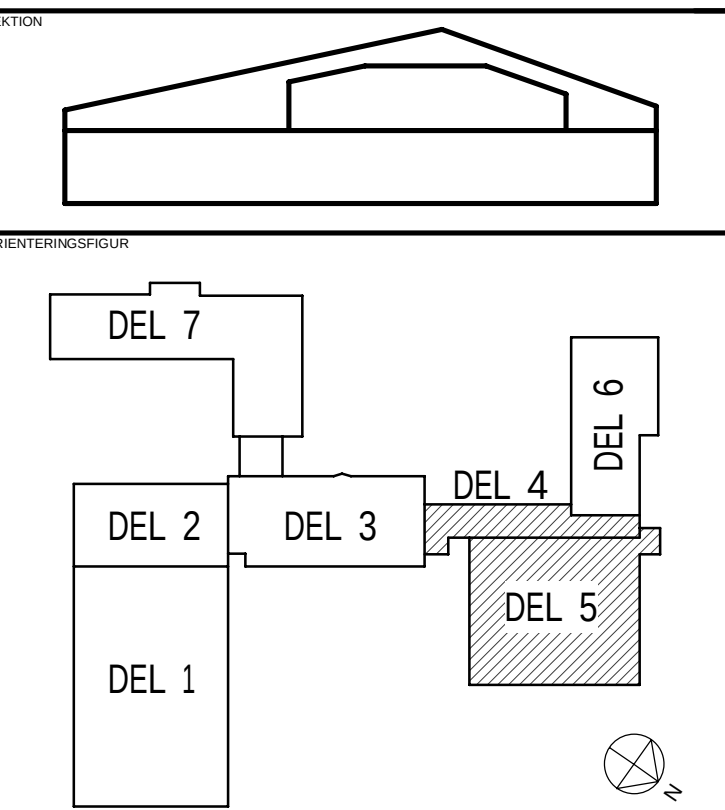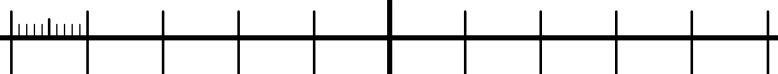

FÖRFRÅGNINGSUNDERLAG

BYGGHANDLING

2025-01-31	T. BERGSTRÖM	KFU01
------------	--------------	-------



OJEKTNAMN

CENTRAL KÖK

ROBERTSFORS KOMMUN

OBJEKTNUMMER	ADRESS
	YTTRE RINGVÄGEN 4
ADRIENUMMER	FÄSTIGHET

	FORDONET 1
DISCIPLIN	FORETAG

PDRAGSNUMMER	SKAPAD AV
00 02 71	SBC

00 03 71	SBS
LEFON	KONTAKTPERSON
010 141 80 00	TOMAS BERGSTRÖM

GGNADSVÆRK	PLUSHØJD (RH 2000)
------------	--------------------

INHOUDSPLAN	VANINGSDIEL	DELOMRADE
-------------	-------------	-----------

10 SAMMANSATT REDOVISNING

INOMRÄT	KATEGORI	SKALA	FORMAT
ASAD		1:100	A1

ASAD	1.100	A1
DOKUMENTNUMMER		ÄNDERUNG
A 10 2 001		A