


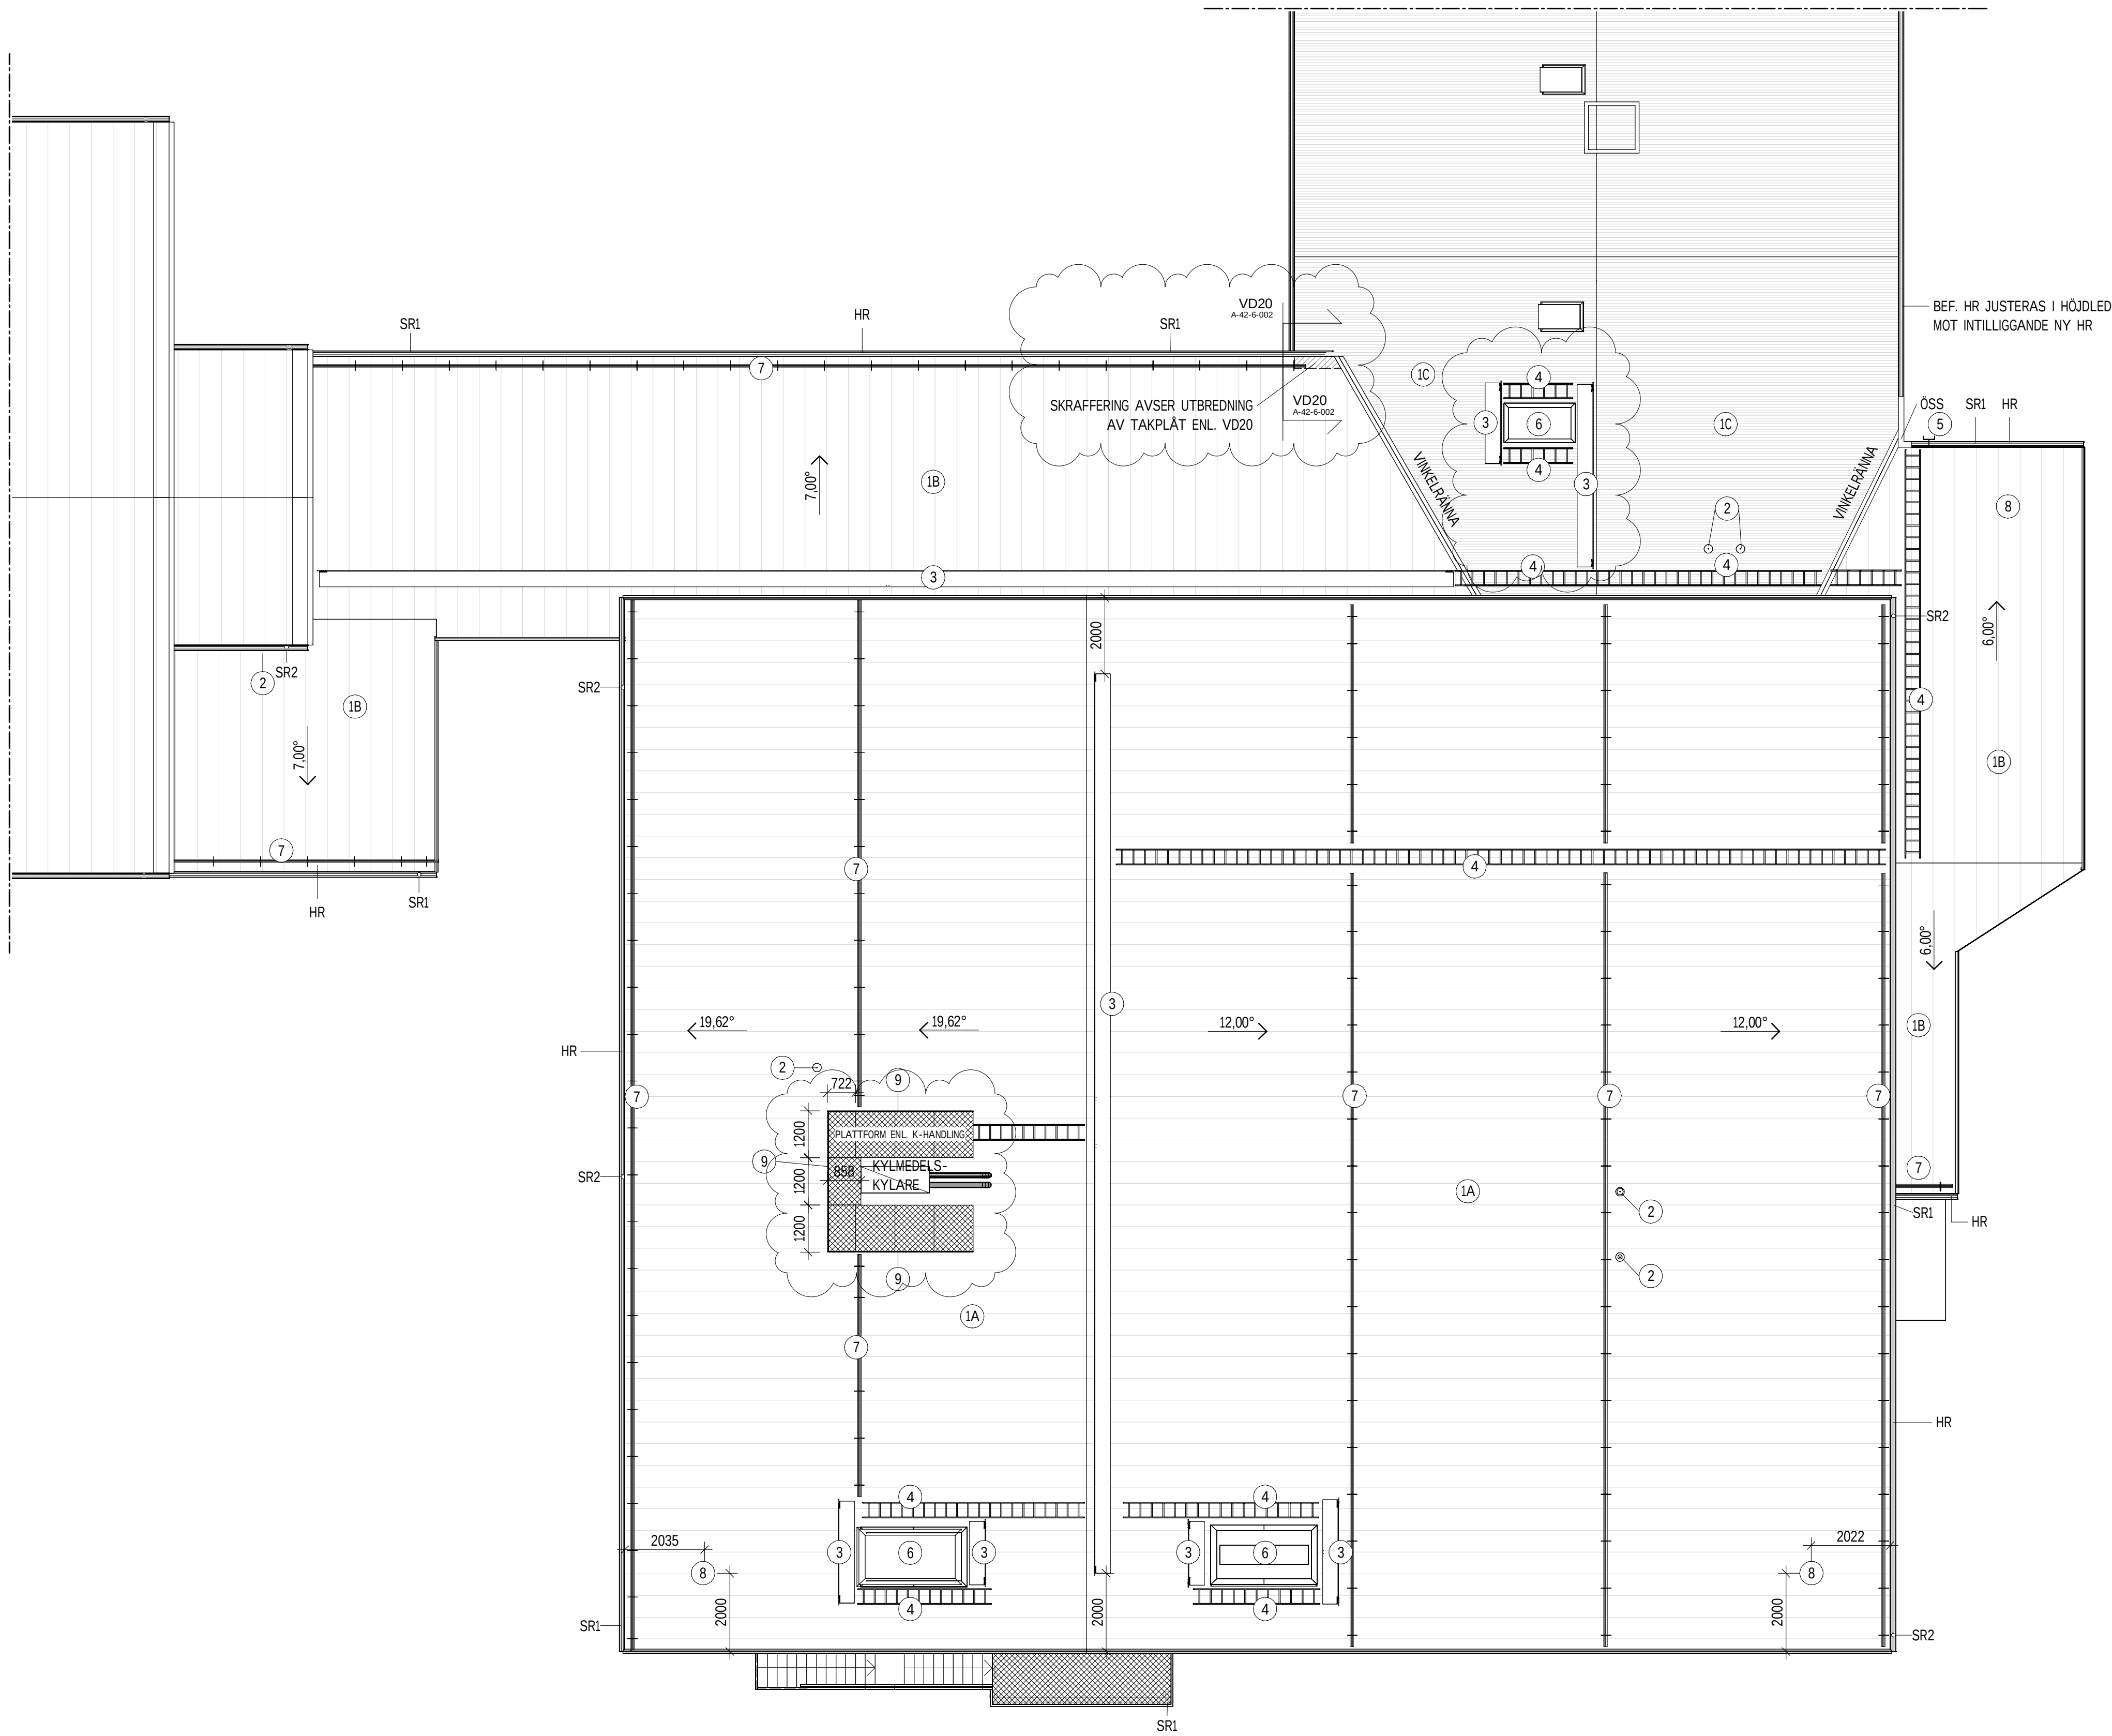

TAKPLAN
1 : 100

SKALA 1:100 0 1 10 METER

FÖRKLARINGAR

- 1A TAK AV PANNPLÅT PLANNJA MODERN, KULÖR SILVERMETALLIC (RAL 9006)
- 1B PLÅTBANDTÄCKNING, KULÖR SILVERMETALLIC (RAL 9006)
- 1C TRP 20, KULÖR SVART LIKA BEFINTLIG
- 2 AVLÜFTNING ENL. VS-HANDLING, KULÖR SILVERMETALLIC (RAL 9006)
- 3 GÅNGBRYGGA MED LIVLINEFÄSTE, KULÖR SILVERMETALLIC (RAL 9006)
- 4 TAKSTEGE I KULÖR SILVERMETALLIC (RAL 9006)
- 5 GLIDSKYDD FÖR LÖS STEGE, KULÖR SILVERMETALLIC (RAL 9006)
- 6 VENTILATIONSHUV ENL. VENT-HANDLING, KULÖR SILVERMETALLIC (RAL 9006)
- 7 SNÖRASSKYDD ENL. SS 831335:2017 ANP. FÖR FALLSKYDDSUTRUSTNING, KULÖR SILVERMETALLIC (RAL 9006)
- 8 FÖRANKRINGSÖGLA, KULÖR SILVERMETALLIC (RAL 9006)
- 9 SEKTIONSRÄCKE, TYP WELAND RÄCKE FÖLJARE EL. LIKV. TOPPMONTAGE.

XX.XX° = TAKLUTNING I GRADER

TAKAVVATTNING

SR1 = STUPRÖR Ø100 MM MARKANSLUTET
KULÖR: SILVERMETALLIC (RAL 9006)


SR2 = STUPRÖR Ø100 MM MED UTKASTARE
KULÖR: SILVERMETALLIC (RAL 9006)

HR = HÄNGRÄNNA 150 MM
KULÖR: SILVERMETALLIC (RAL 9006)

ÖSS = ÖVERSPOLNINGSSKYDD ENL. BESKRIVNING
KULÖR: SILVERMETALLIC (RAL 9006)
LIKA HÄNGRÄNNA

HÄNVISNINGAR

TAKGENOMFÖRINGAR ENL. K, SE K-25-6-001

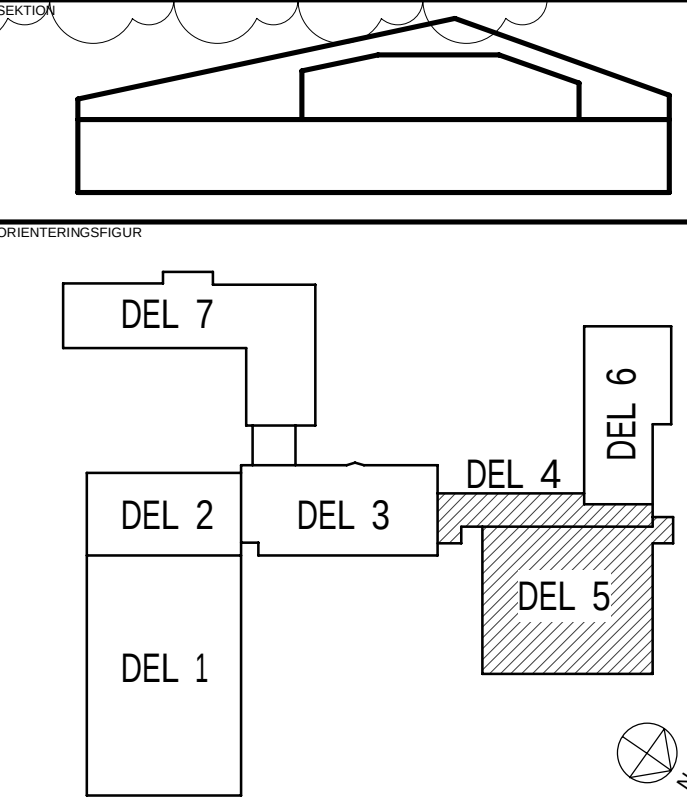

FÖRFRÅGNINGSUNDERLAG		
BYGGHANDLING		
DATUM	2025-01-31	ANSÖKAN NR
2025-01-31	T. BERGSTRÖM	KFU01



CENTRALEKÖK		
ROBERTSFORS KOMMUN		
PROJEKTNUMMER	YTTRE RINGVÄGEN 4	
DIARIENUMMER	FORDONET 1	
DISCIPLIN	NORCONSULT SVERIGE AB	
UPPDRAGSNUMMER	108 83 71	
TELEFON	010 141 80 00	
BYGGNADSTYP	TOMAS BERGSTRÖM	
VÄRNINGSPLAN	VÄRNINGSDIREKTÖR	DELOMRÅDE
		DEL 4, 5
SYSTEM		
41 YTTERTAK OCH YTTREBJÄLKLAG		
SPECIFIKATION		
TAKPLAN		
BYGGNADSTYP	SKALA	FORMAT
PLAN	1:100	A1
DOKUMENTNUMMER	A-41-1-001	
	A	