



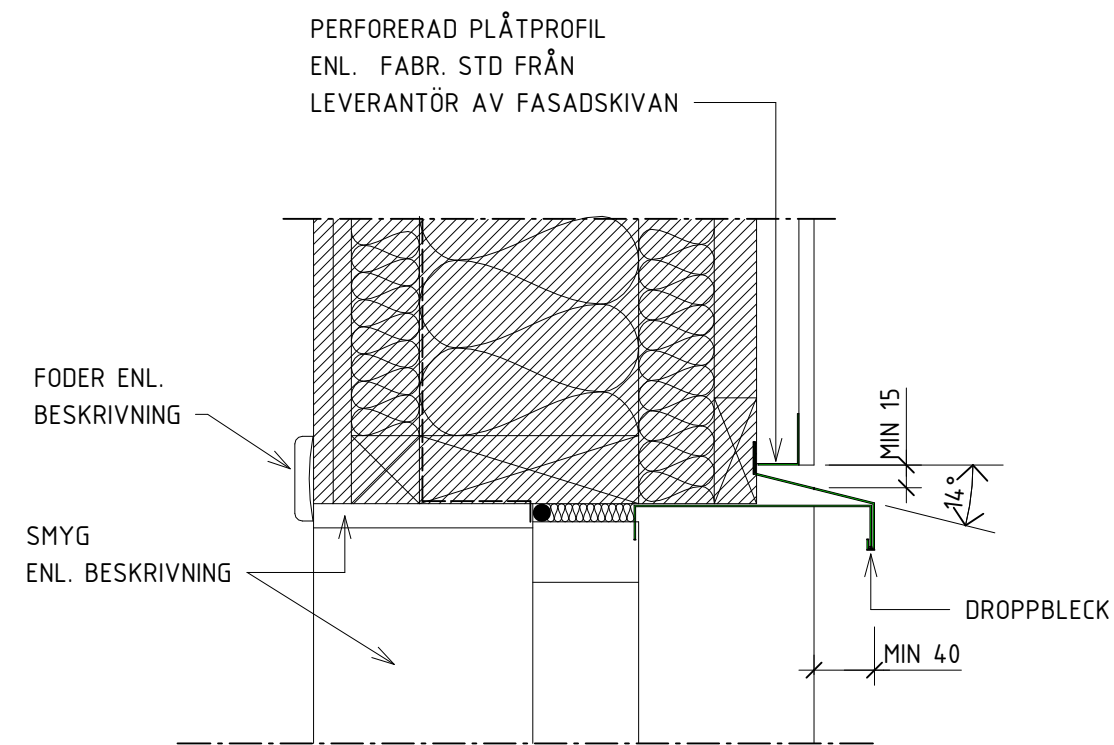


VD17 PRINCIPDETALJ

1:5 FÖNSTER SOPRUM

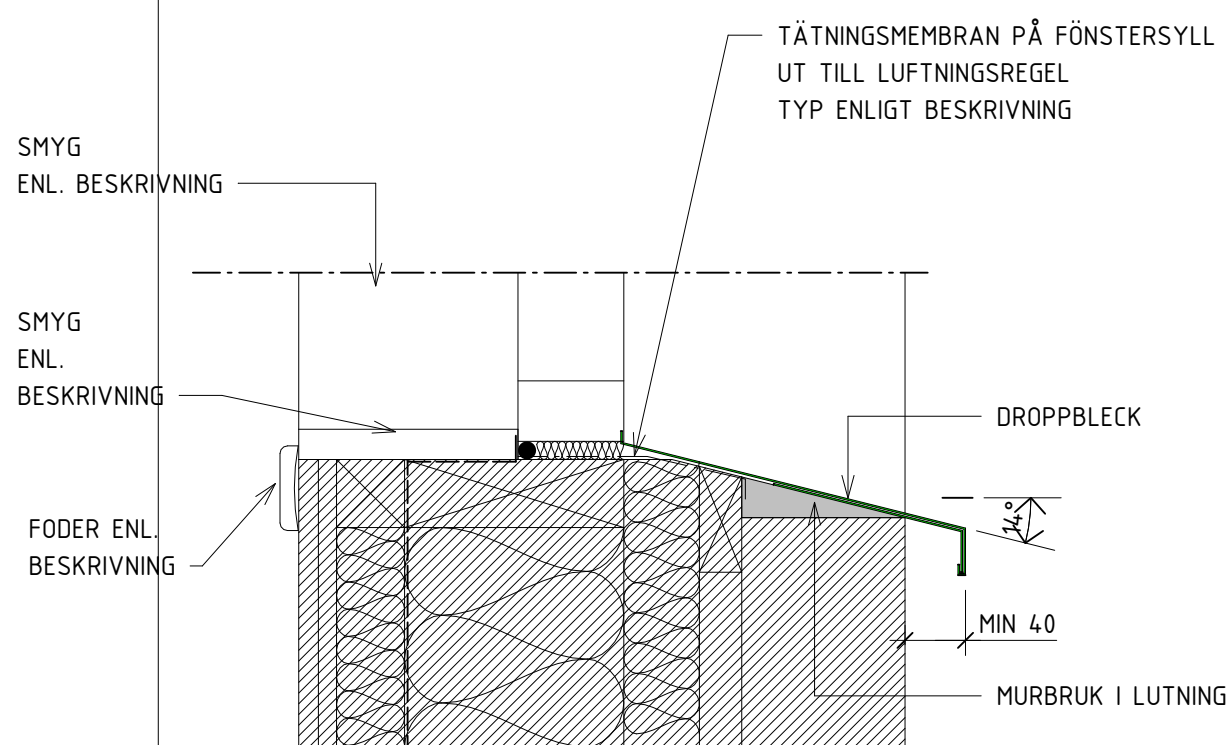

VD18 PRINCIPDETALJ


1:5 FÖNSTER SOPRUM

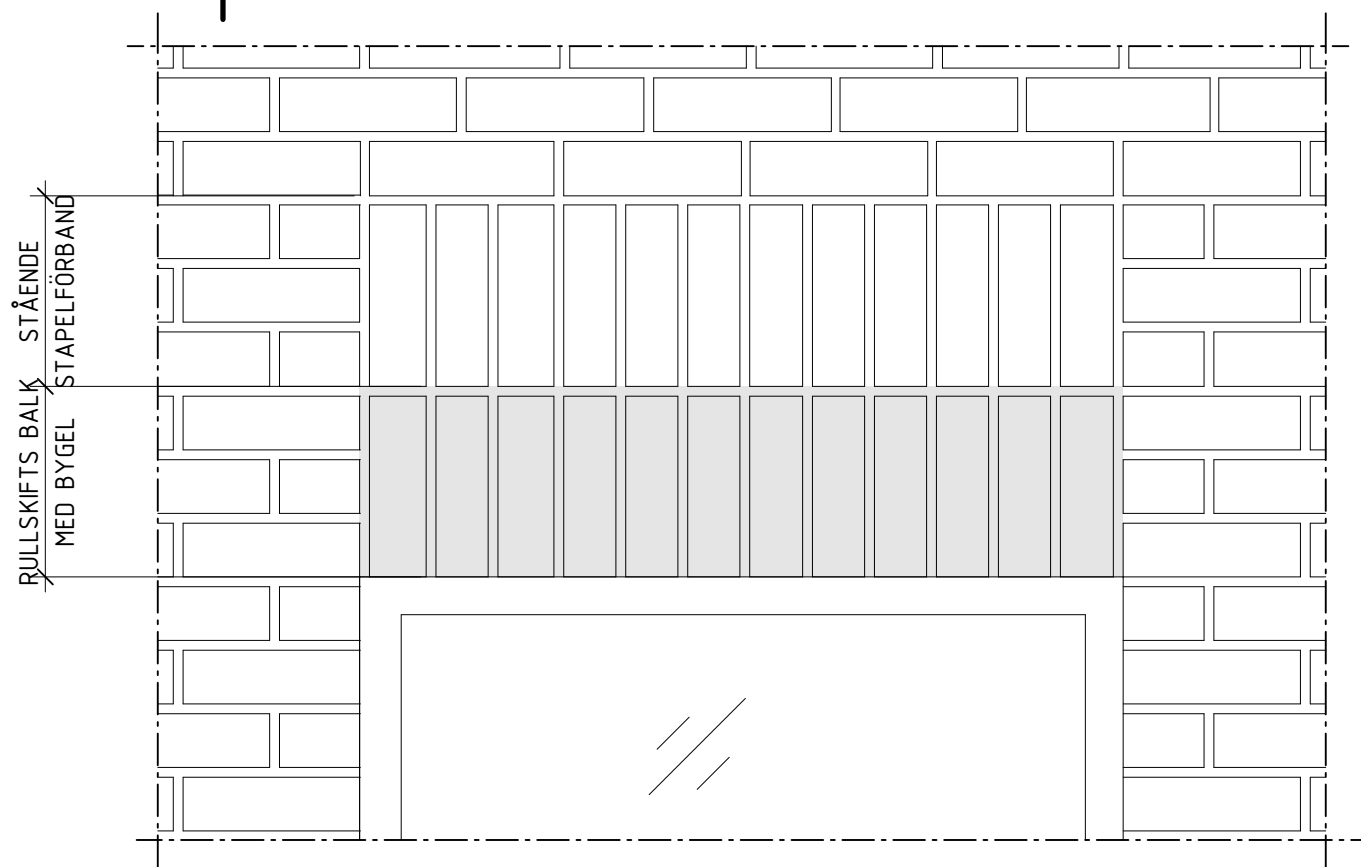

EV1 PRINCIP ELEVATION

1:10


RULLSKIFTS BALK - MED BYGEL

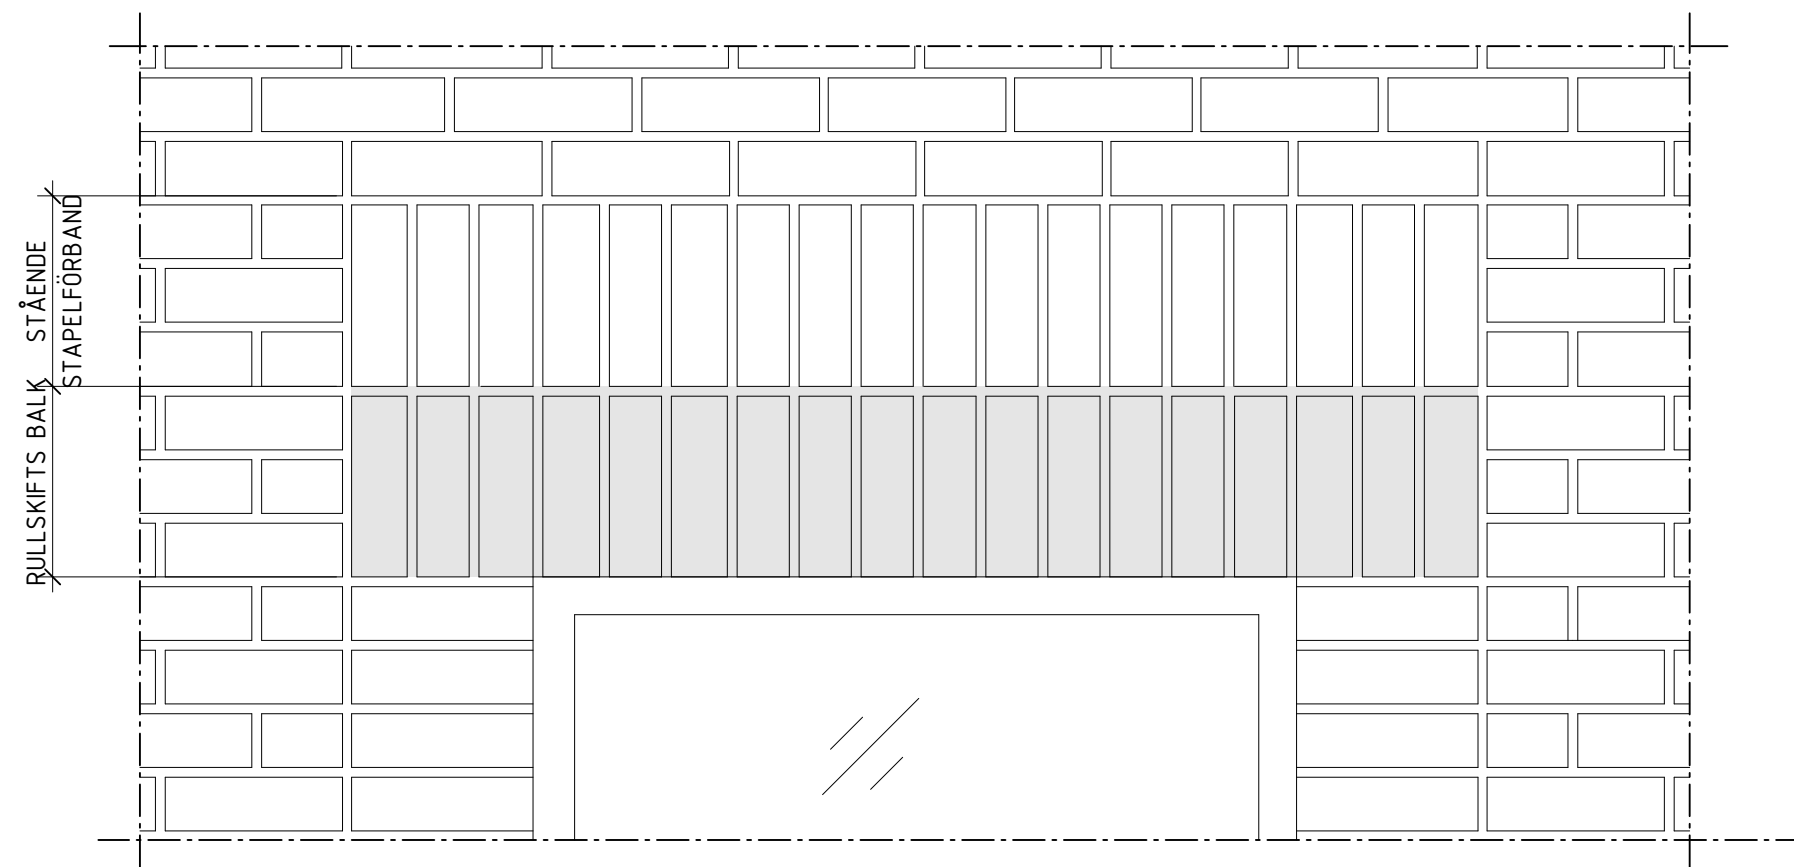

EV2 PRINCIP ELEVATION


1:10

RULLSKIFTS BALK

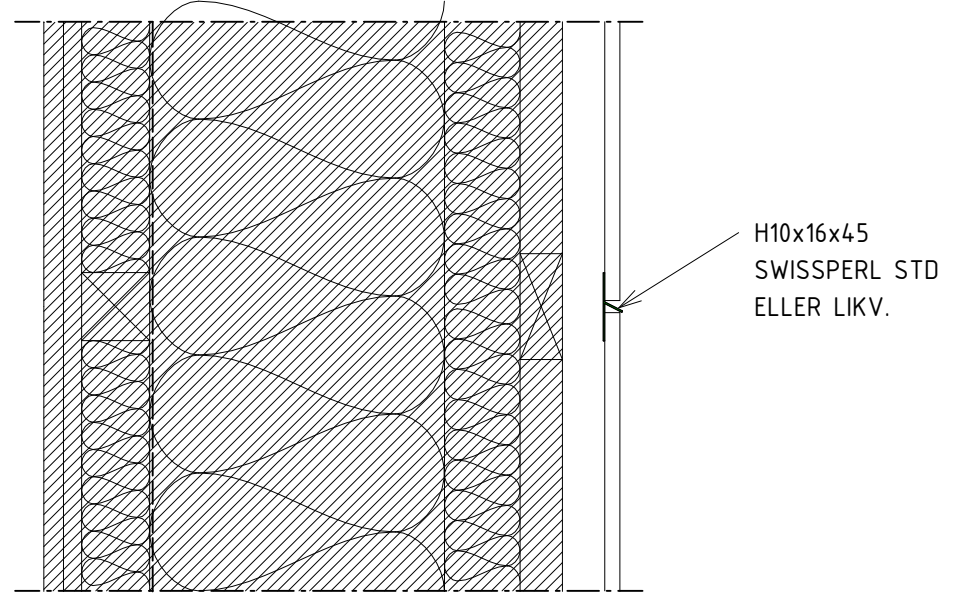


VD19 PRINCIPDETALJ

1:5 LIST MELLAN FASADSKIVOR

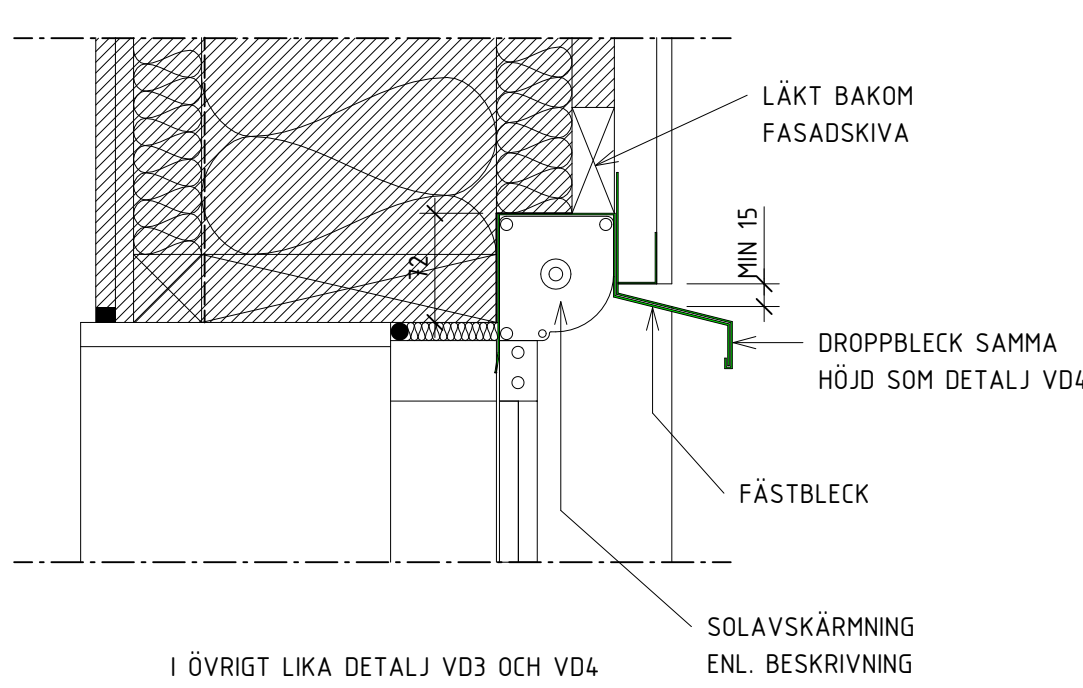


VD21 PRINCIPDETALJ

1:5 FÖNSTER MED VERTIKALMARKIS

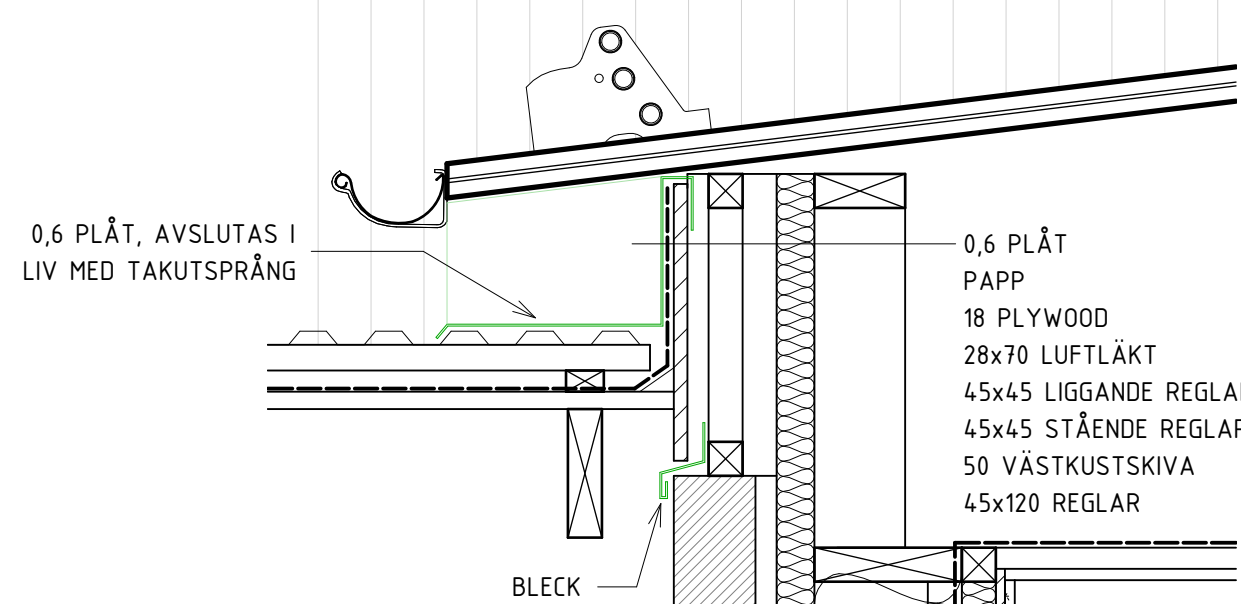


VD20 - TAKMÖTE

1:10

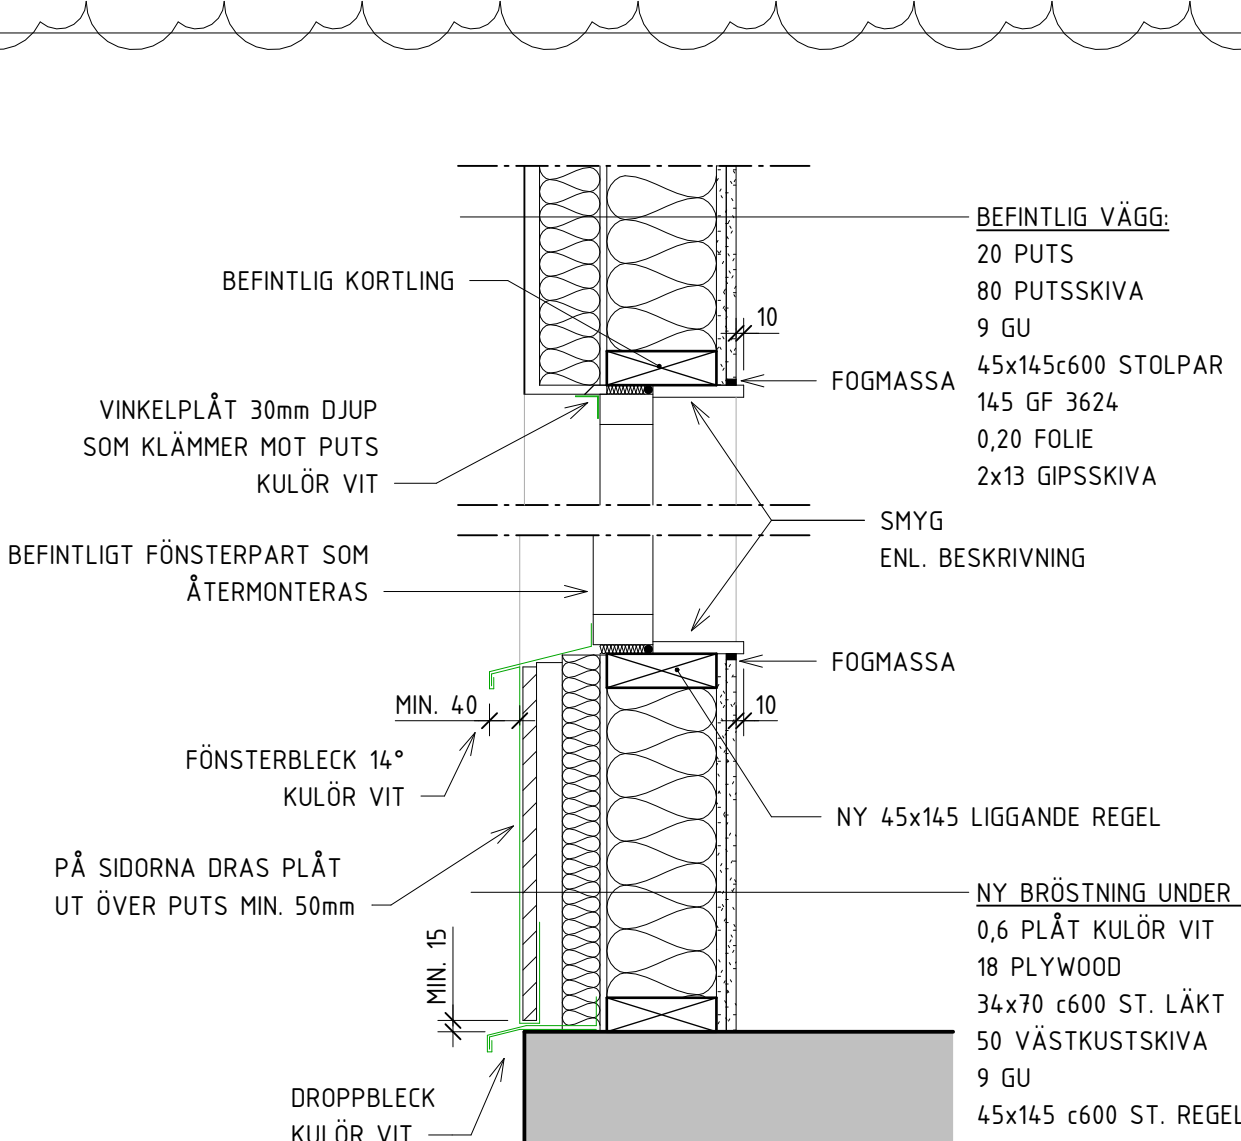

VD22 - IGENBYGGNAD FÖNSTER FRITIDS

1:10

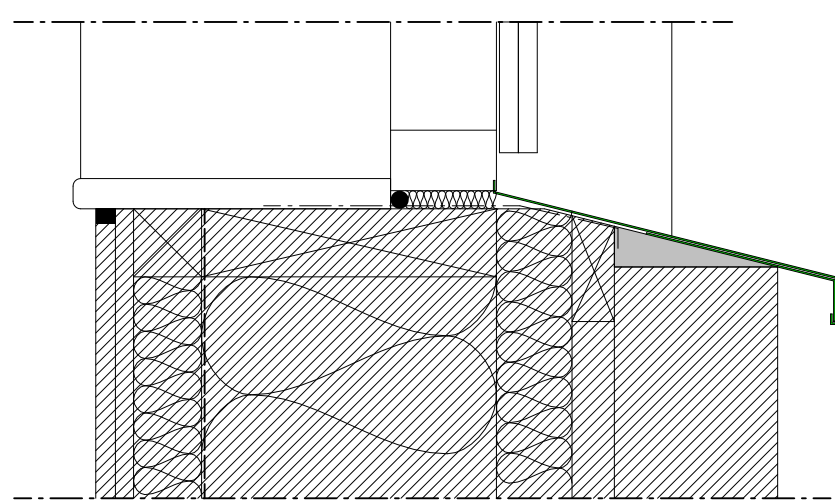

VD23 - IGENBYGGNAD FÖNSTER TRAPPHUS

1:10

EV1 PRINCIP ELEVATION

1:10

RULLSKIFTS BALK - MED BYGEL

EV2 PRINCIP ELEVATION

1:10

RULLSKIFTS BALK

FÖRKLARINGAR

ALLA MÅTT ANGES I MILLIMETER

= ENL. K

HÄNVISNINGAR

FASADER - ÖVERSIKT


VERTIKALA OCH HORIZONTELLA DETALJER

A-40-3-001

A-42-6-001--003

IGENBYGGNAD MOT UC, PLAN


1:20

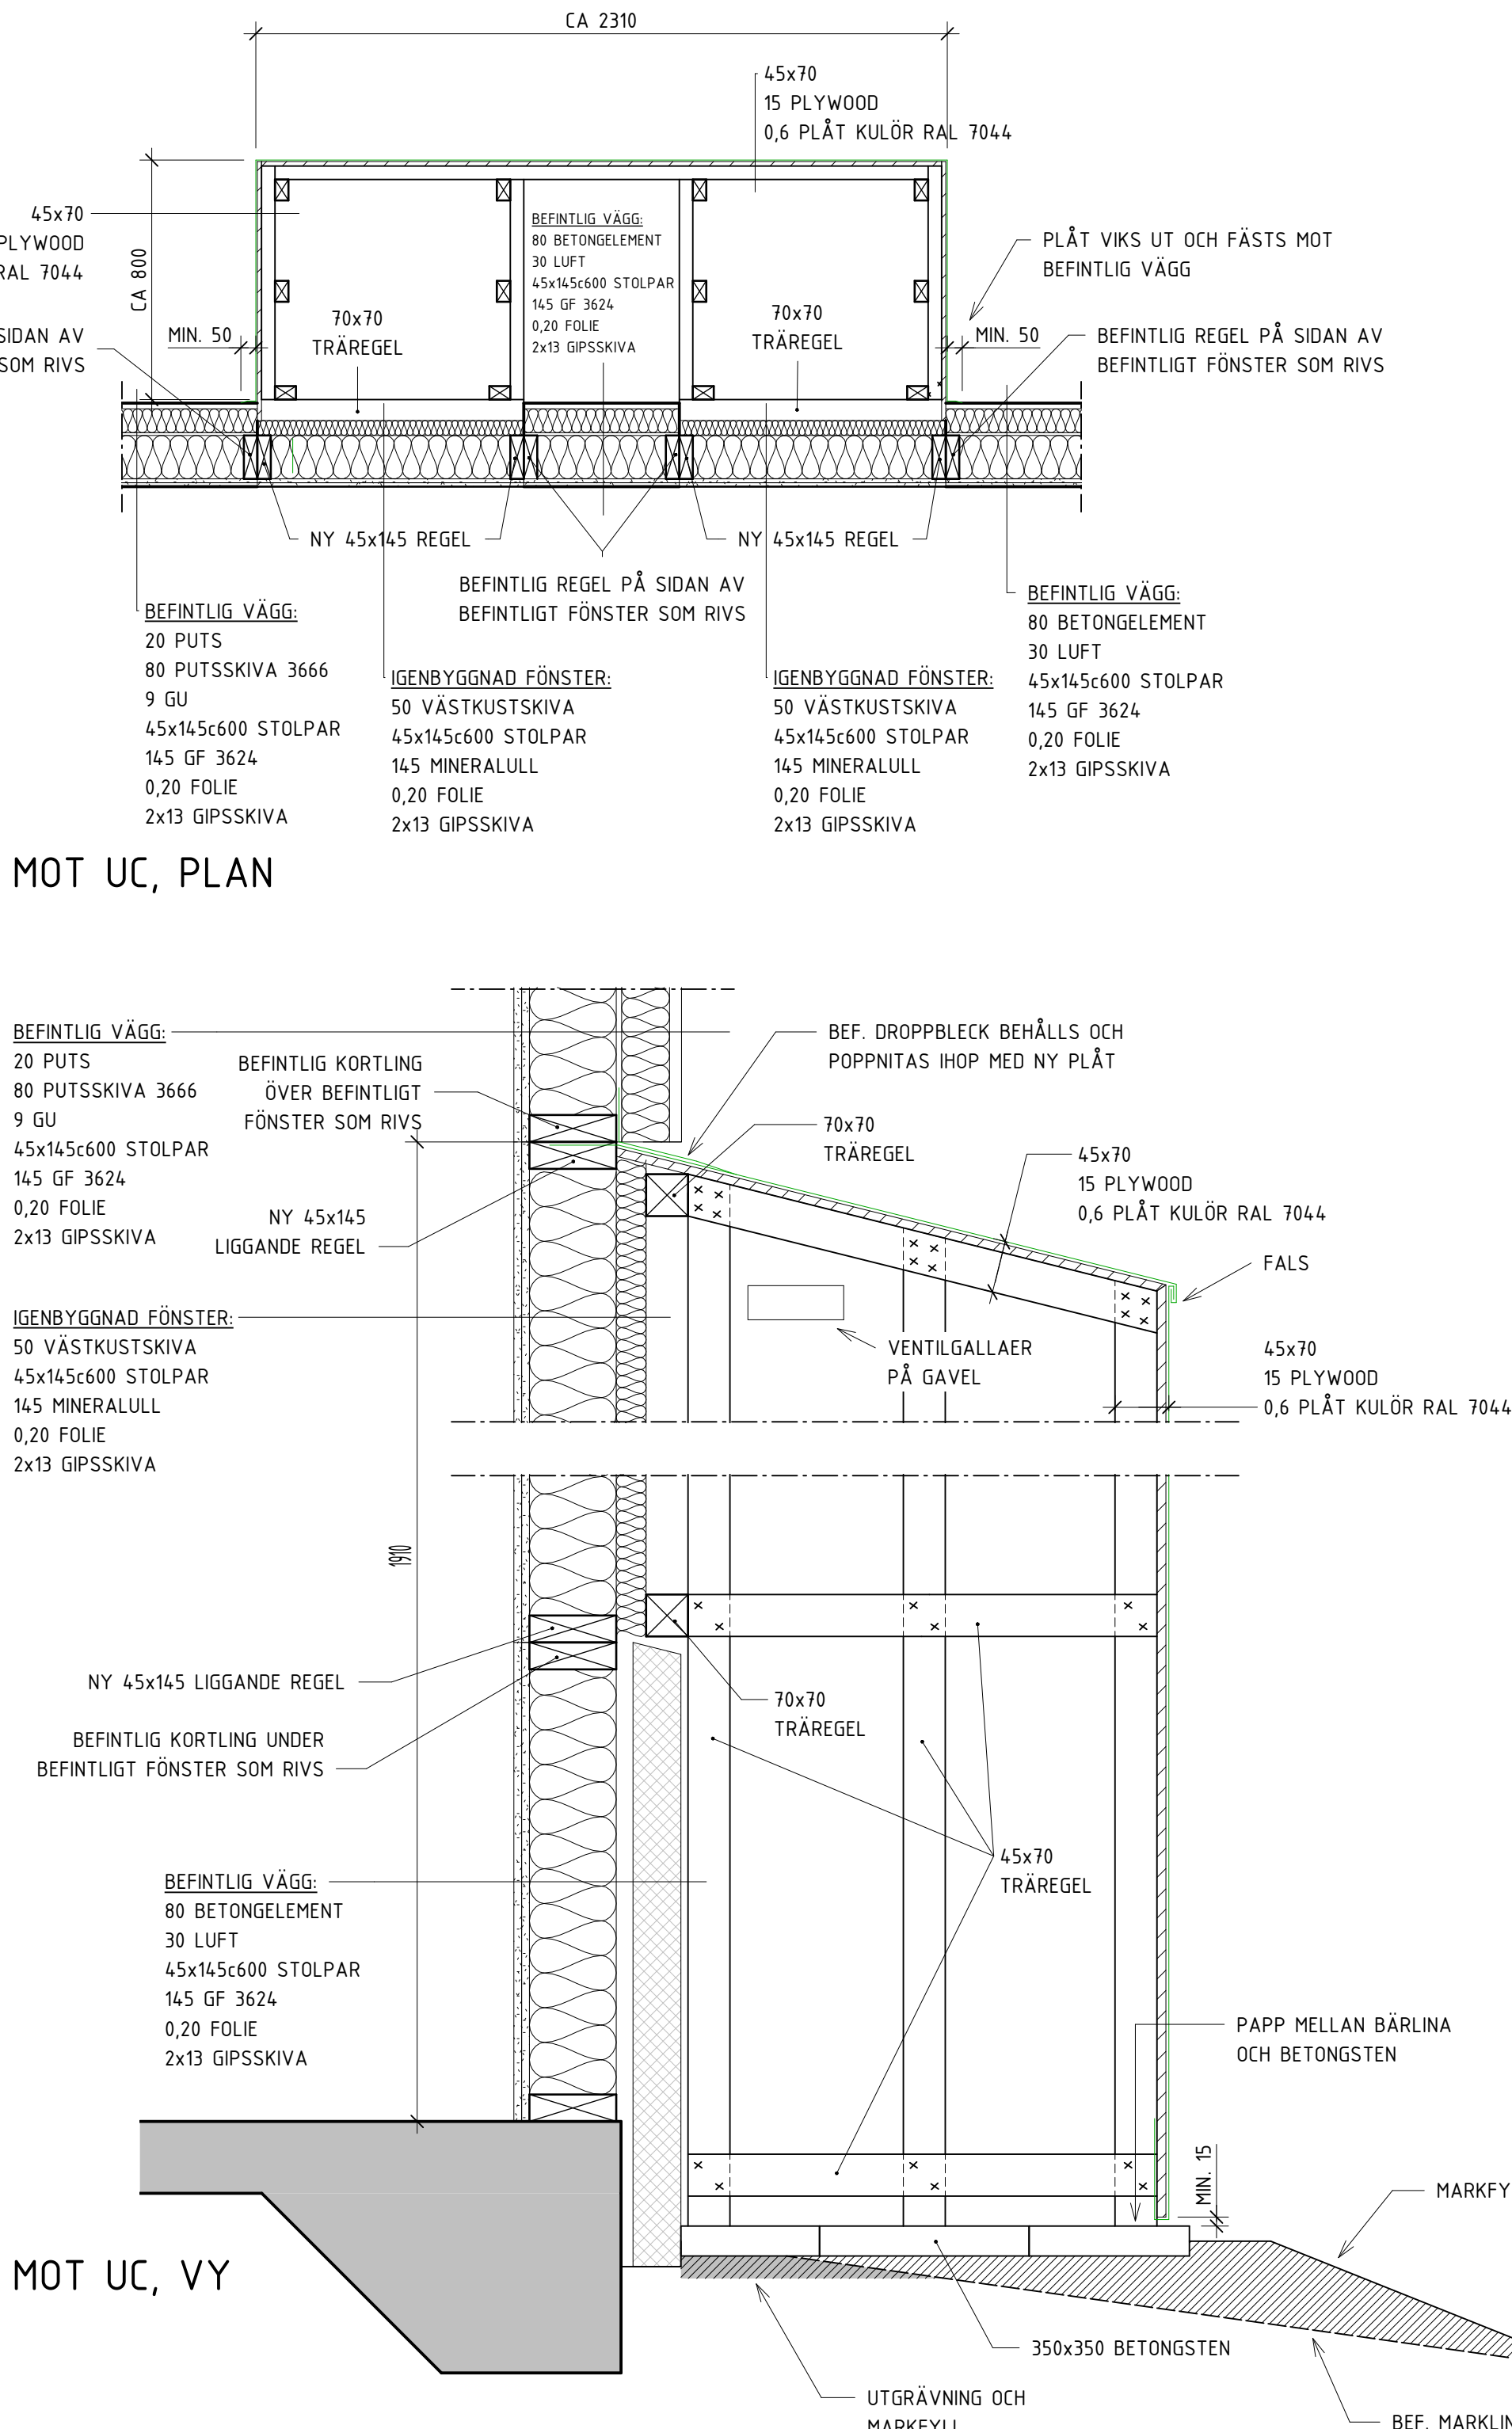

IGENBYGGNAD MOT UC, VY

1:10

SKALA 1:5 0 100 500 MILLIMETER

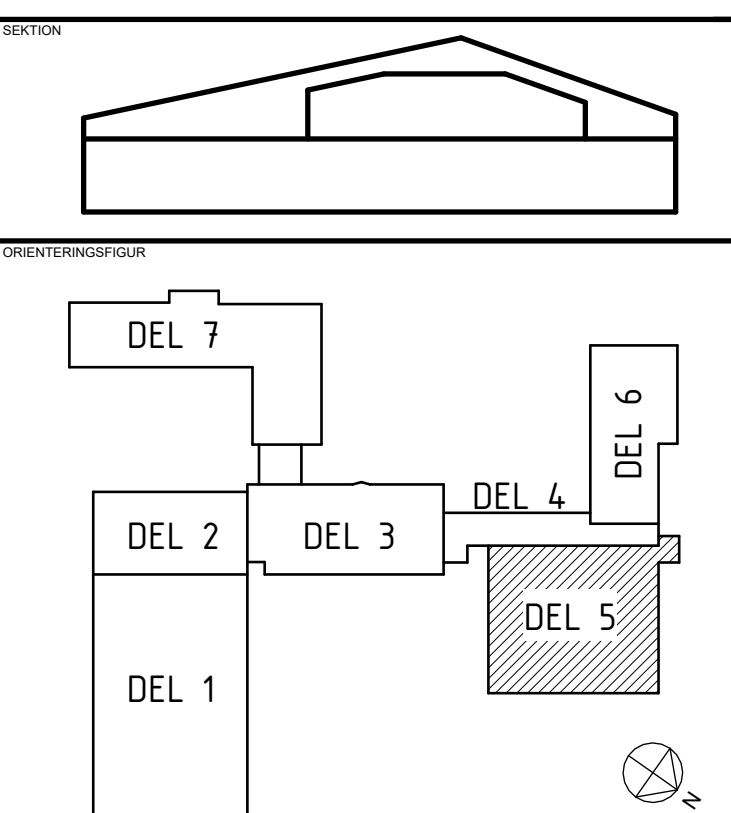

FÖRFRÅGNINGSUNDERLAG

BYGGHANDLING

DATUM 2025-01-31

ANSÖKAN T. BERGSTRÖM

ANSÖKAN KFU01

BYGGHANDLING

BYGGHANDLING

