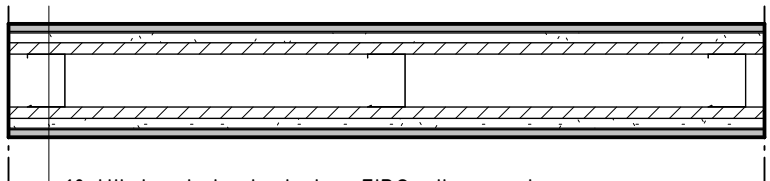
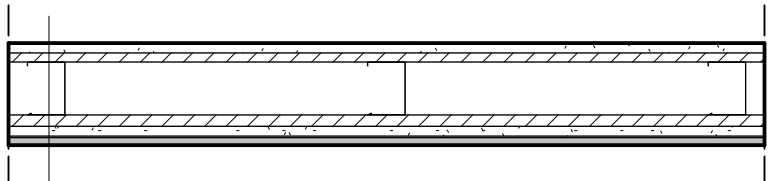
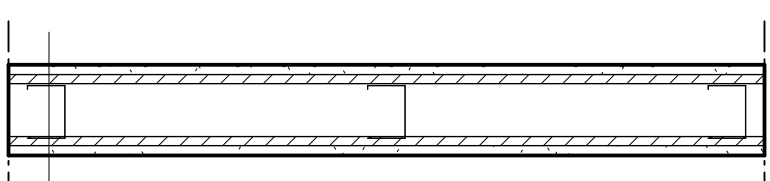
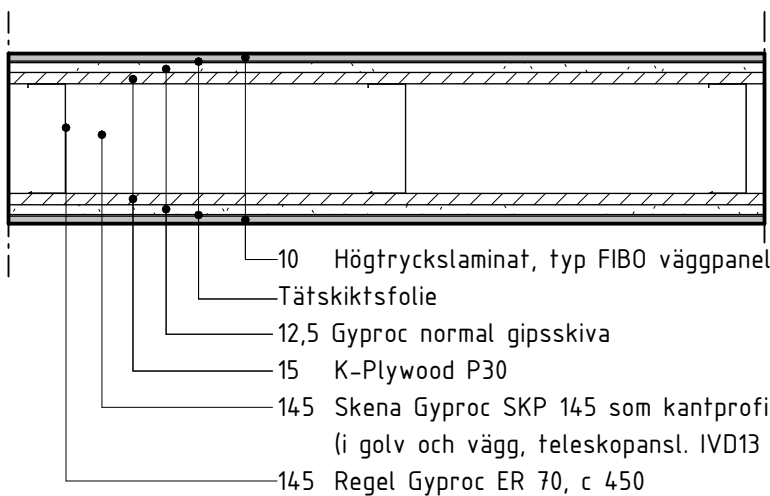
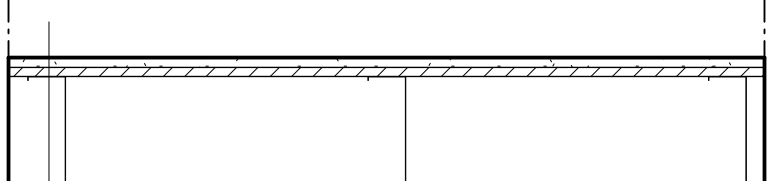
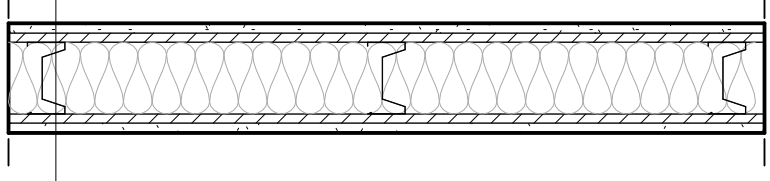
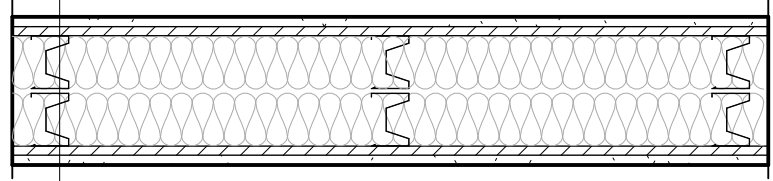
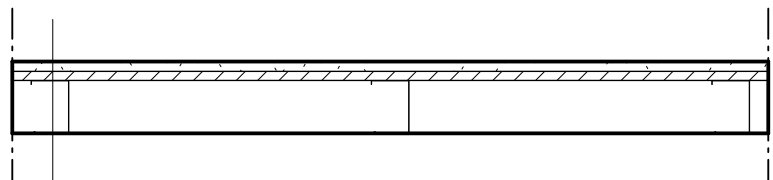


2025-01-31 14:14:16

TYP	UPPSTÄLLNING	BREDD	VÄGGTYP ENL. GYPROC	LJUD-KLASS	BRAND-KLASS	KOMMENTAR
V1	 10 Högtryckslaminat, typ FIBO väggpanel Tättskiktsfolie 12,5 Gyproc Normal Gipsskiva 15 K-Plywood P30 70 Skena Gyproc SKP 70 som kantprofil (i golv och vägg, teleskopansl. IVD13 i tak) 70 Regel Gyproc ER 70, c 450 15 K-Plywood P30 12,5 Gyproc Normal Gipsskiva Tättskiktsfolie 10 Högtryckslaminat, typ FIBO väggpanel	150	-	-	-	
V2a	 12,5 Gyproc Normal Gipsskiva 12 Plywood 70 Skena Gyproc SKP 70 som kantprofil (i golv och vägg, teleskopansl. IVD13 i tak) 70 Regel Gyproc ER 70, c 450 12,5 Gyproc Normal Gipsskiva 15 K-Plywood P30 Tättskiktsfolie 10 Högtryckslaminat, typ FIBO väggpanel	135	-	-	-	
V2b		136	-	-	-	Yttre gipsskiva byts till Swissperal Multiforce (på sida mot kylrumsvägg)
V3a	 12,5 Gyproc Normal Gipsskiva 12 Plywood 70 Skena Gyproc SKP 70 som kantprofil (i golv och vägg, teleskopansl. IVD13 i tak) 70 Regel Gyproc ER 70, c 450 12 Plywood 12,5 Gyproc Normal Gipsskiva	120	GYPROC ER 70/70 (450) NN-NN M0	-	-	Inre gipsskivor är utbytta mot 12 mm plywood
V3b		119	-	-	-	Yttre gipsskiva byts till Swissperal Multiforce (på sida mot kylrumsvägg). Övrigt lika V3a
V3c		120	GYPROC ER 70/70 (450) NN-NN M0	-	EI30	Inre gipsskivor är utbytta mot 12 mm plywood
V4	 10 Högtryckslaminat, typ FIBO väggpanel Tättskiktsfolie 12,5 Gyproc normal gipsskiva 15 K-Plywood P30 145 Skena Gyproc SKP 145 som kantprofil (i golv och vägg, teleskopansl. IVD13 i tak) 145 Regel Gyproc ER 70, c 450	225	-	-	-	
V5	 12,5 Gyproc normal gipsskiva 12 Plywood 145 Skena Gyproc SKP 145 som kantprofil (i golv och vägg, teleskopansl. IVD13 i tak) 145 Regel Gyproc ER 70, c 450 12 Plywood 12,5 Gyproc normal gipsskiva	195	-	-	-	
V6a	 12,5 Gyproc Normal Gipsskiva 12 Plywood 95 Kantprofil Gyproc AC 95 (i golv och vägg, teleskopansl. IVD13 i tak) 95 Regel Gyproc XR 95, c 450 95 Mineralull 12 Plywood 12,5 Gyproc Normal Gipsskiva	145	GYPROC XR 95/95 (450) NN-NN M95	48dB	-	Inre gipsskivor är utbytta mot 12 mm plywood, vilket innebär att ljudreduktion försämras med 3dB

SKALA 1:10 0 100

1000 MILLIMETER

TYP	UPPSTÄLLNING	BREDD	VÄGGTYP ENL. GYPROC	LJUD-KLASS	BRAND-KLASS	KOMMENTAR
V6b		160	GYPROC XR 95/95 (450) NN-NN M95	48dB	-	Förändringar enl. *. Övrigt lika typ a
V7a	 12,5 Gyproc Normal Gipsskiva 12 Plywood 70x2 Kantprofil Gyproc AC 70 (i golv och vägg, teleskopansl. IVD13 i tak) 70x2 Regel Gyproc XR 70, c 450 70x2 Mineralull 12 Plywood 12,5 Gyproc Normal Gipsskiva	196	GYPROC XR 70/70x2 (450) NN-NN M140	48dB	-	Inre gipsskivor är utbytta mot 12 mm plywood, vilket innebär att ljudreduktion försämras med 3dB
V7b		211	GYPROC XR 70/70x2 (450) NN-NN M140	48dB	-	Förändringar enl. *. Övrigt lika typ a
V8a	 12,5 Gyproc Normal Gipsskiva 12 Plywood 70 Skena Gyproc SKP 70 som kantprofil (i golv och vägg, teleskopansl. IVD13 i tak) 70 Regel Gyproc ER 70, c 450	95	GYPROC ER 70/70 (450) NN-0 M0	-	-	Inre gipsskivor är utbytta mot 12 mm plywood
V8b		110	GYPROC ER 70/70 (450) NN-0 M0	-	-	Förändringar enl. *. Övrigt lika typ a

* = På väggsida mot kök byts samtliga skivmaterial till: 15 K-Plywood P30
12,5 Gyproc Normal Gipsskiva
Tättskiktsfolie
10 Högtryckslaminat, typ FIBO väggpanel

FÖRESKRIFTER

Anslutningsdetaljer som inte är redovisade skall utföras enligt Gyproc och Wallsystems Space anvisningar.

ANMÄRKNING
Beakta särskilt utförande av innerväggar med ljudklass >40dB och dess anslutningar mot golv, mötande inner- och yttervägg samt mot bjälklag.
De skall fyllas med isolering i de fack (mellan regler) där installationer ska gå genom vägg.



Runt dörrar, glaspartier och fönster med brand och ljudkrav utföres erforderlig drevning samt tätning med fogmassa för att klara ställda krav.

Omfattning av väggar med ställda brandkrav enligt planritningar.

FÖRSTÄRKNINGAR
Utfärgående hörn utförs med inspacklade hörnlistor typ Gyproc Aquabead Gab 90 eller likv.

HÄNVISNINGAR

PLAN 1, DELPLANER A-40-1-141 -- 154
INVÄNDIGA DETALJER A-43-6-001 -- 002

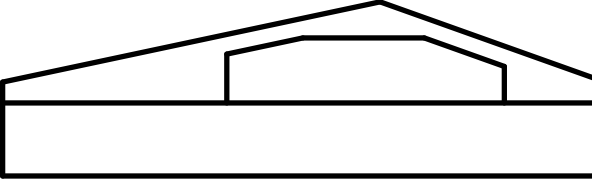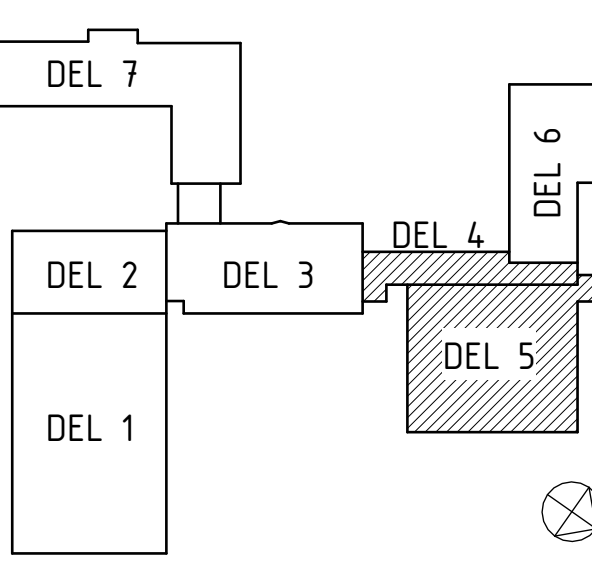SEKTION		
		
ORIENTERINGSSKISS		
		
STATUS		
FÖRFRÅGNINGSUNDERLAG		
HANDLING		
BYGGHANDLING		
DATUM	ÖSKAD AV	ÄNDRING PM
2025-01-31	T. BERGSTRÖM	KFU01
BESTÄLLARE		
 ROBERTSFORS KOMMUN		
PROJEKTNAMN		
CENTRALKÖK		
OMRÅDE		
ROBERTSFORS KOMMUN		
PROJEKTNUMMER	FÄRDIGT	
	YTTRE RINGVÄGEN 4	
DIREKTOR	FÖRETAG	
	FORDONET 1	
DIREKTOR	FÖRETAG	
A	NORCONSULT SVERIGE AB	
UPPDRAGSNUMMER	SKAPAD AV	
108 83 71	MSR	
TELEFON	KONTAKTPERSON	
010 141 80 00	TOMAS BERGSTRÖM	
BYGGNADSTYRELSE	FÄRDIGT (BY 2025)	
VÄNINGSPLAN	VÄNINGSDEL	DELOMRÅDE
SYSTEM		
43 INRE RUMSBILDANDE BYGGDELAR		
SPECIFIKATION		
INNERVÄGGSTYPER		
UPPSTÄLLNING		
SKALA 1:10		
FORMAT A1		
DOCUMENTNUMMER		
A-43-5-001		
ÄNDRING		
A		

FILENAMN: C:\Norconsult\Autodesk\Revit\1088371-Centralkok Robertsfors_centralfil-2024_matsta.rvt