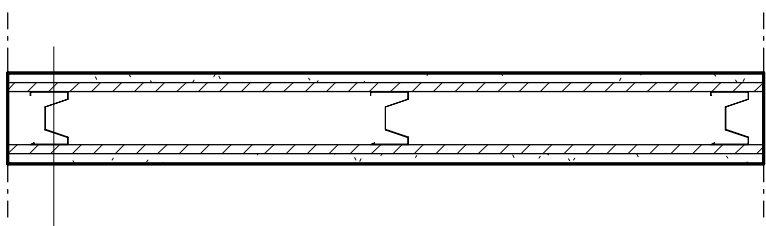
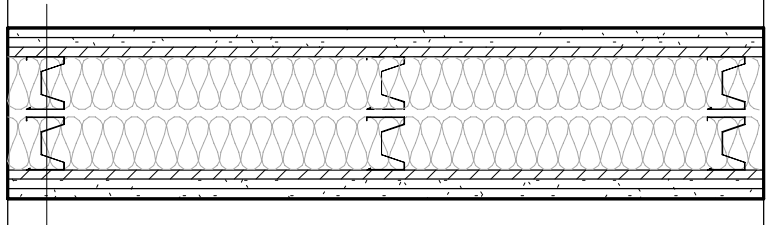
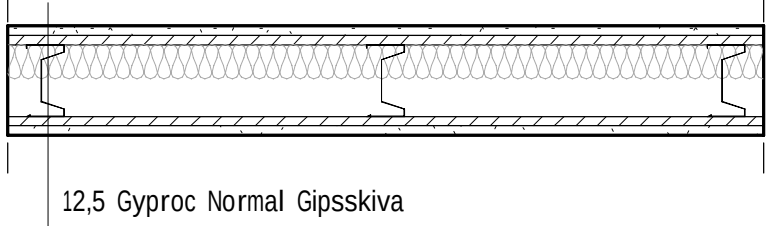
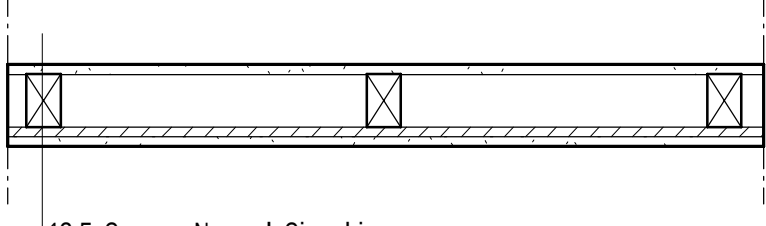
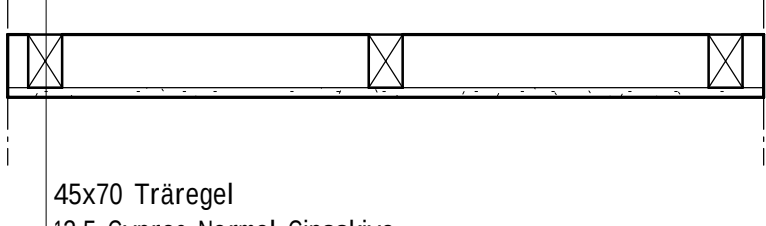
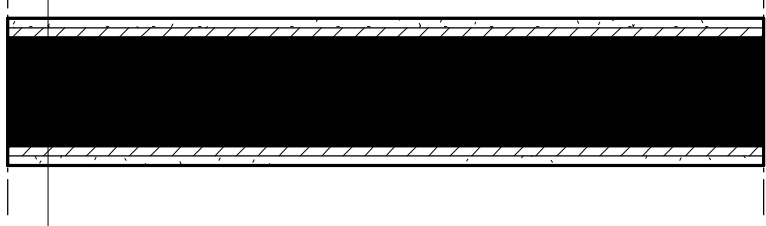
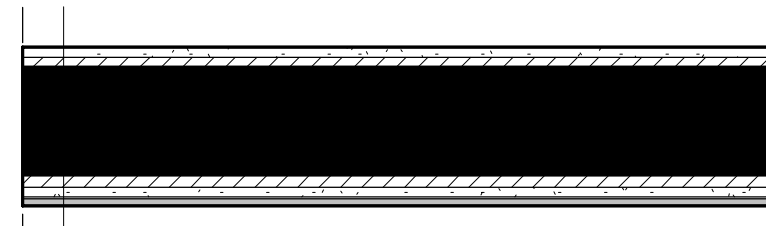
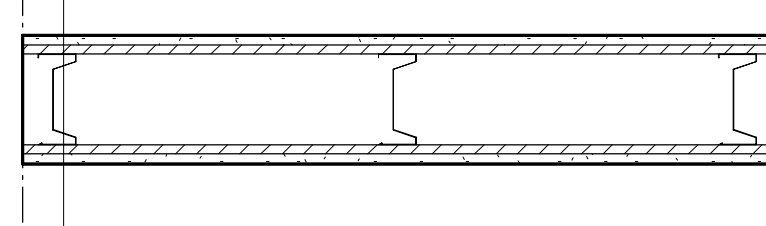


TYP	UPPSTÄLLNING	BREDD	VÄGGTYP ENL. GYPROC	LJUD-KLASS	BRAND-KLASS	KOMMENTAR
V9a	 12,5 Gyproc Normal Gips skiva 12 Plywood 70 Kantprofil Gyproc AC (i golv och vägg, teleskopansl. IVD13 i tak) 12 Plywood 12,5 Gyproc Normal Gips skiva	120	GYPROC XR 70/70 (450) NN-NN M0	40dB	-	Inre gipsskivor är utbytta mot 12 mm plywood, vilket innebär att ljudreduktion försämras med 3dB
V9b		123	GYPROC XR 70/70 (450) NN-NN M0	40dB	-	Inre skiva av 15 mm K-plywood samt tätskiktsfolie utsida gips mot RWC/D. Övrigt lika V9a
V9c		135	GYPROC XR 70/70 (450) NN-NN M0	40dB	-	Förändringar enl. *. Övrigt lika typ a
V10a	 12,5x2 Gyproc Normal Gips skiva 12 Plywood 70x2 Kantprofil Gyproc AC 70 (i golv och vägg, teleskopansl. IVD13 i tak) 70x2 Regel Gyproc XR 70, c 450 70x2 Mineralull 12 Plywood 12,5x2 Gyproc Normal Gips skiva	226	GYPROC XR 70/70x2 (450) NNN-NNN M140	52dB	-	Inre gipsskivor är utbytta mot 12 mm plywood, vilket innebär att ljudreduktion försämras med 3dB
V10b		226	GYPROC XR 70/70x2 (450) NNN-NNN M140	52dB	EI30	Inre gipsskivor är utbytta mot 12 mm plywood, vilket innebär att ljudreduktion försämras med 3dB
V11	 12,5 Gyproc Normal Gips skiva 12 Plywood 95 Kantprofil Gyproc AC 95 (i golv och vägg, teleskopansl. IVD13 i tak) 95 Regel Gyproc XR 95, c 450 45 Mineralull 12 Plywood 12,5 Gyproc Normal Gips skiva	145	GYPROC XR 95/95 (450) NN-NN M45	48dB	-	Inre gipsskivor är utbytta mot 12 mm plywood, vilket innebär att ljudreduktion försämras med 3dB
V12	 12,5 Gyproc Normal Gips skiva 45x70 Träreger 12 Plywood 12,5 Gyproc Normal Gips skiva	108	-	-	-	
V13	 45x70 Träreger 12,5 Gyproc Normal Gips skiva	83	-	-	-	
V14a	 12,5 Gyproc Normal Gips skiva 12 Plywood Stomme enl. K 12 Plywood 12,5 Gyproc Normal Gips skiva	195	-	-	-	

SKALA 1:10 0 100

1000 MILLIMETER

TYP	UPPSTÄLLNING	BREDD	VÄGGTYP ENL. GYPROC	LJUD-KLASS	BRAND-KLASS	KOMMENTAR
V14b		194	-	-	-	Yttre gipsskiva byts till Swissperal Multiforce (på sida mot kylrumsvägg)
V14c		195	-	44dB	-	Fack mellan reglar fylls med 145 mm mineralull. Övrigt lika V14b
V14d		145	-	-	-	På sida mot befintlig vägg monteras inga skivor
V15	 12,5 Gyproc Normal Gips skiva 12 Plywood Stomme enl. K 15 K-Plywood P30 12,5 Gyproc Normal Gips skiva Tätskiktsfolie 10 Högtryckslaminat, typ FIBO väggpanel	210	-	-	-	
V16	 12,5x2 Gyproc Normal Gips skiva 12 Plywood 120 Kantprofil Gyproc AC 120 (i golv och vägg, teleskopansl. IVD13 i tak) 120 Regel Gyproc XR 120, c 450 12 Plywood 12,5x2 Gyproc Normal Gips skiva	170	GYPROC XR 120/120 (450) NN-NN M0	40dB	-	Inre gipsskivor är utbytta mot 12 mm plywood, vilket innebär att ljudreduktion försämras med 3dB

* = På väggsida mot kök byts samtliga skivmaterial till: 15 K-Plywood P30
12,5 Gyproc Normal Gips skiva
Tätskiktsfolie
10 Högtryckslaminat, typ FIBO väggpanel

FÖRESKRIFTER

Anslutningsdetaljer som inte är redovisade skall utföras enligt Gyproc och Wallsystems Space anvisningar.

ANMÄRKNING

Beakta särskilt utförande av innerväggar med ljudklass >40dB och dess anslutningar mot golv, mötande inner- och yttervägg samt mot bjälklag. De skall fyllas med isolering i de fack (mellan reglar) där installationer ska gå genom vägg.

Runt dörrar, glaspartier och fönster med brand och ljudkrav utföres erforderlig drevning samt tätning med fogmassa för att klara ställda krav.

Omfattning av väggar med ställda brandkrav enligt planritningar.

FÖRSTÄRKNINGAR

Utåtgående hörn utförs med inspacklade hörnlister typ Gyproc Aquabead Gab 90 eller likv.

HÄNVISNINGAR

PLAN 1, DELPLANER A-40-1-141 -- 154
INVÄNDIGA DETALJER A-43-6-001 -- 002

SEKTION

ORIENTERINGSSKISS

STATUS

FÖRFRÅGNINGSUNDERLAG

HANDLING

DATUM

2025-01-31

GÖRKÄNG AV

T. BERGSTRÖM

ÄNDRINGS RM

KFU01

BESTÄLLARE



ROBERTSFORS
KOMMUN

PROJEKTNAMN

CENTRALKÖK

OMRÅDE

ROBERTSFORS KOMMUN

PROJEKTNUMMER

ADRESS

YTTRE RINGVÄGEN 4

DIREKTÖRSNUMMER

FASTIGHET

FORDONET 1

PROJEKT

NORCONSULT SVERIGE AB

UPPDRAGSNUMMER

SKAPAD AV

108 83 71

MSR

TELEFON

KONTAKTPERSON

010 141 80 00

TOMAS BERGSTRÖM

BYGGNADSVÄRK

FÖLJESKED (RM 2000)

VÄNINGSPLAN

VÄNINGSDEL

DELOMRÅDE

SYSTEM

43 INRE RUMSBILDANDE BYGGDELAR

SPECIFIKATION

INNERRÄGGSTYPER

HITINGSKATEGORI

SKALA

FORMAT

UPPSTÄLLNING

1:10

A1

DOKUMENTNUMMER

ANMÄRKNING

A-43-5-002

A