




INKLÄDNADER

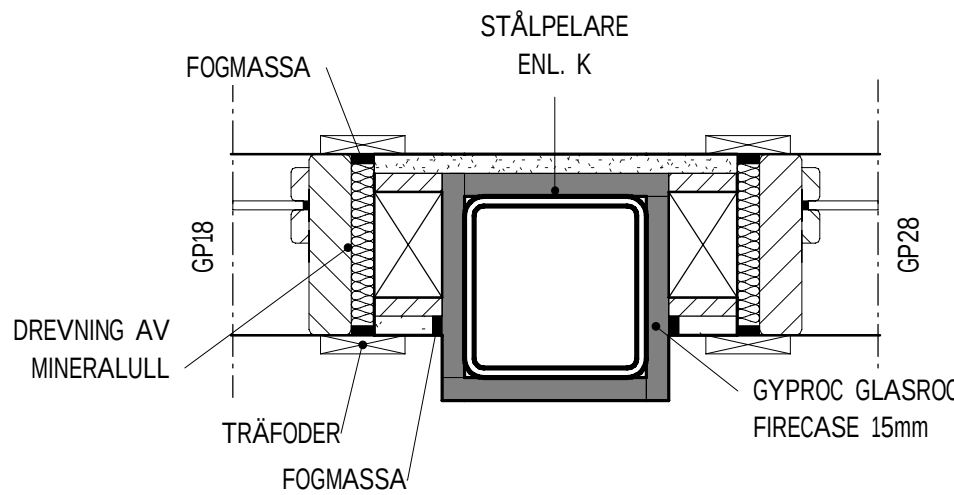


IK1 - STÅLPELARE MELLAN GLASPARTIER
1 : 5

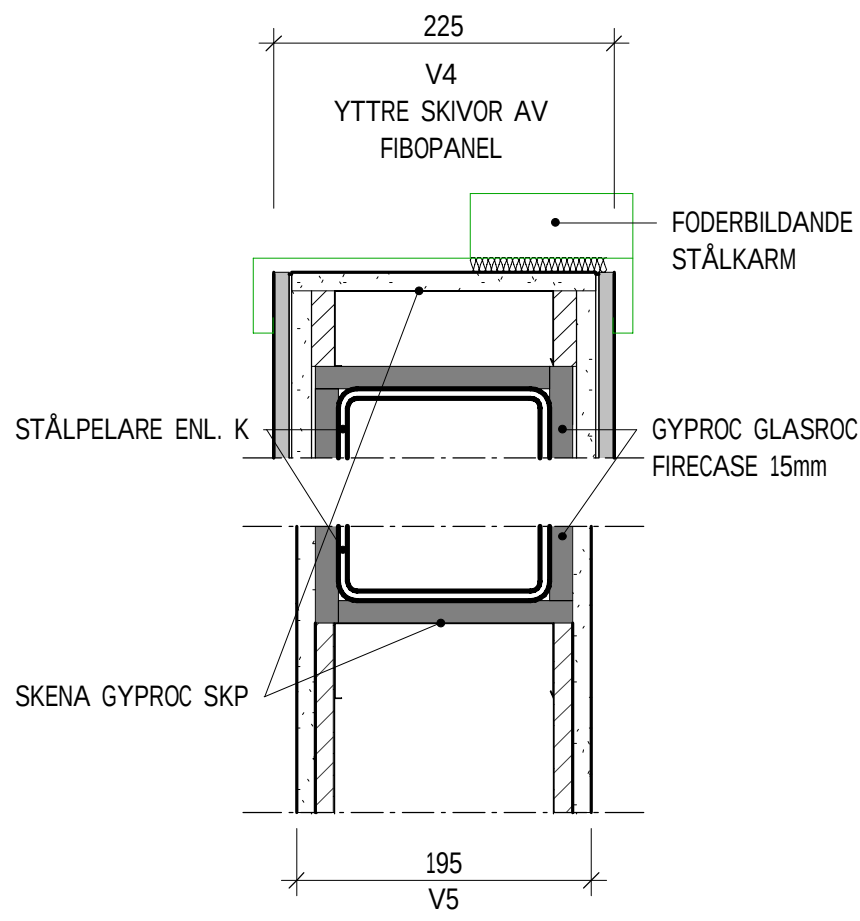


IK2 - STÅLPELARE I INNERVÄGG
1 : 5

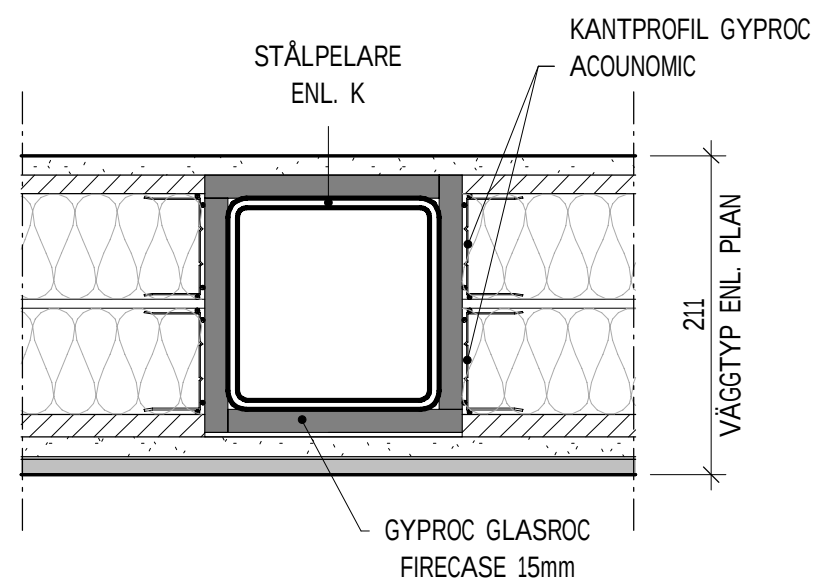


IK3 - STÅLPELARE I DUBBELREGLVÄGG
1 : 5

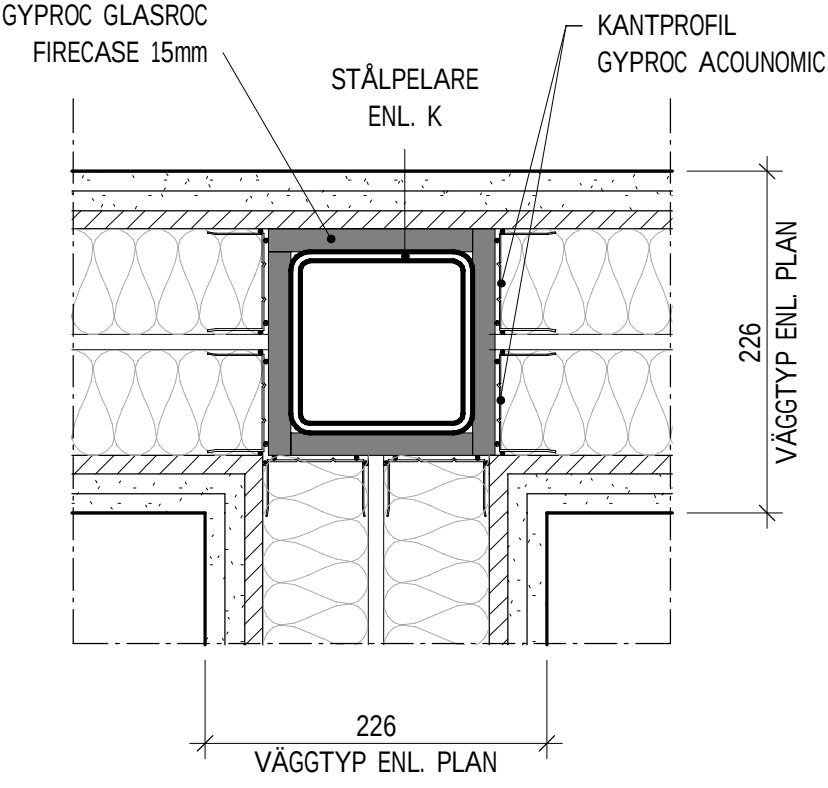


IK4 - STÅLPELARE I VÄGGKORSNING
1 : 5

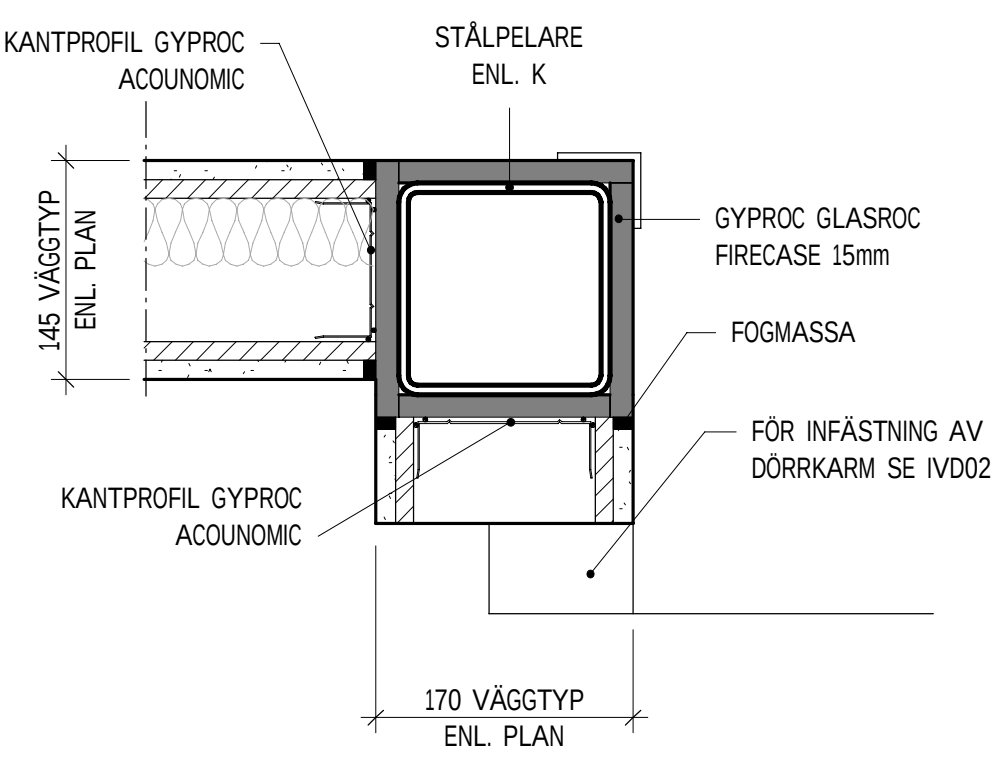


IK5 - STÅLPELARE I INNERVÄGGSHÖRN
1 : 5

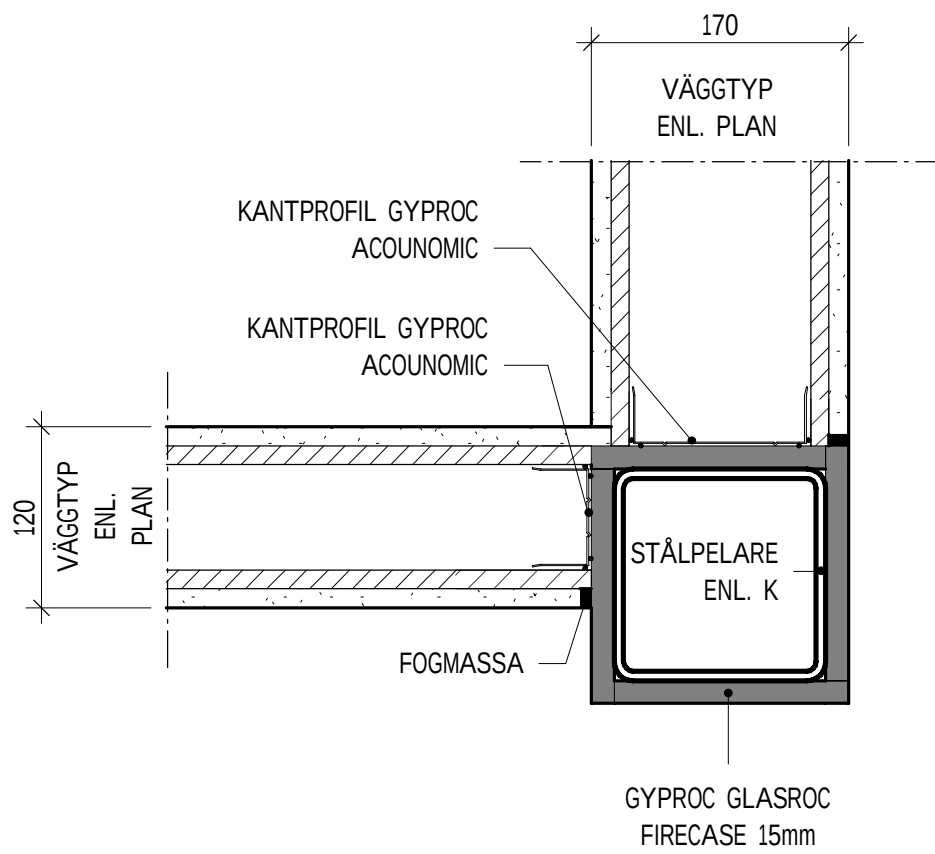


IK6 - HALVT UTSTICKANDE PELARE
1 : 5

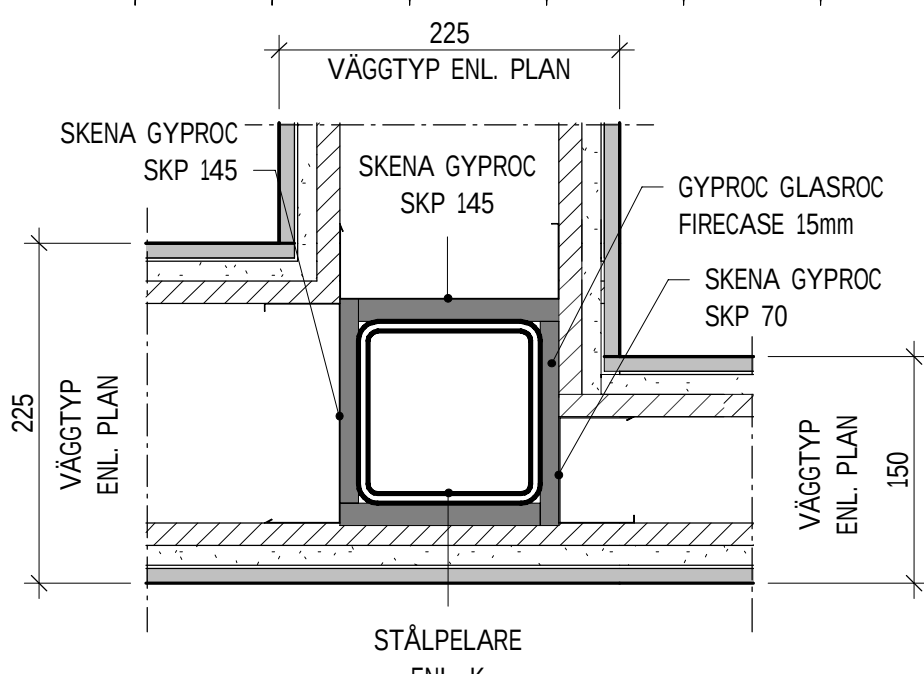


IK7 - STÅLPELARE I VÄGGKORSNING KÖK
1 : 5

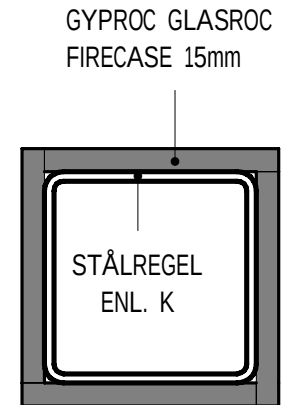

IK8 - PRINCIPDETALJ FRISTÅENDE STÅLPELARE
1 : 5

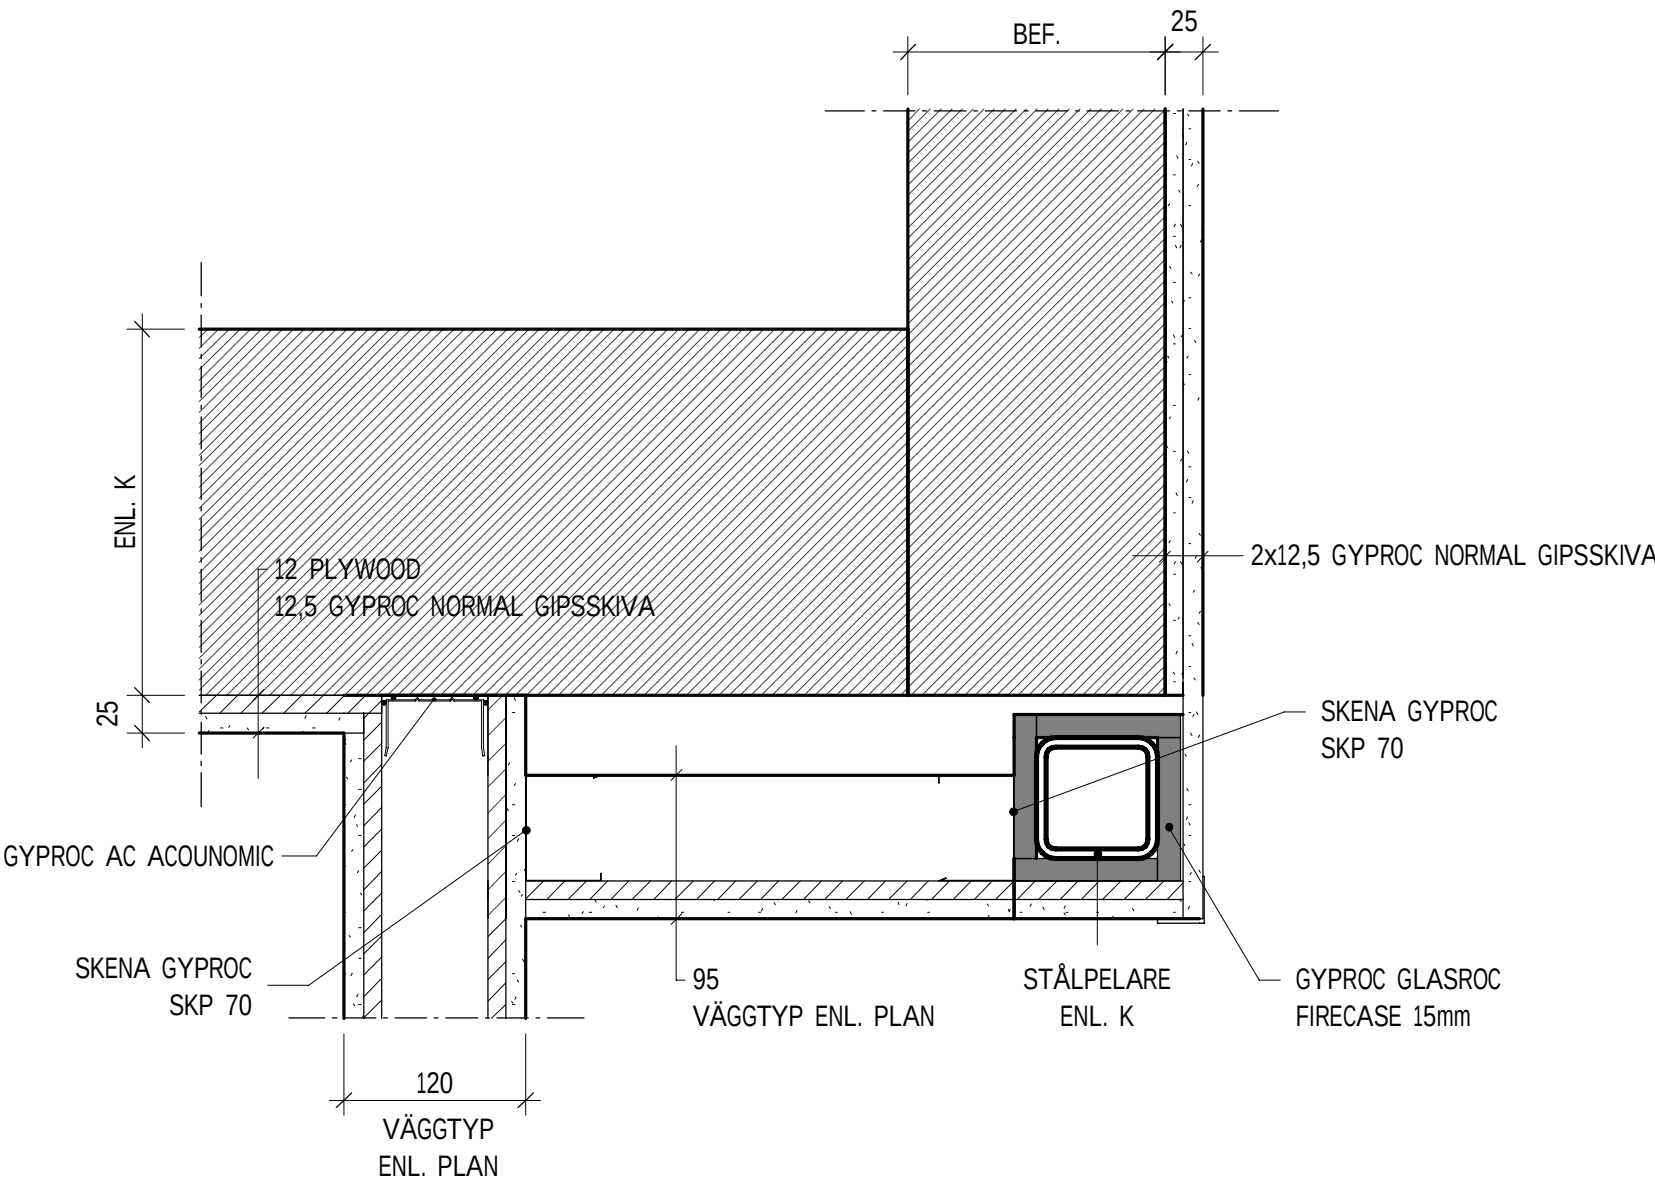

IK9 - STÅLPELARE VID BEFINTLIG VÄGG
1 : 5

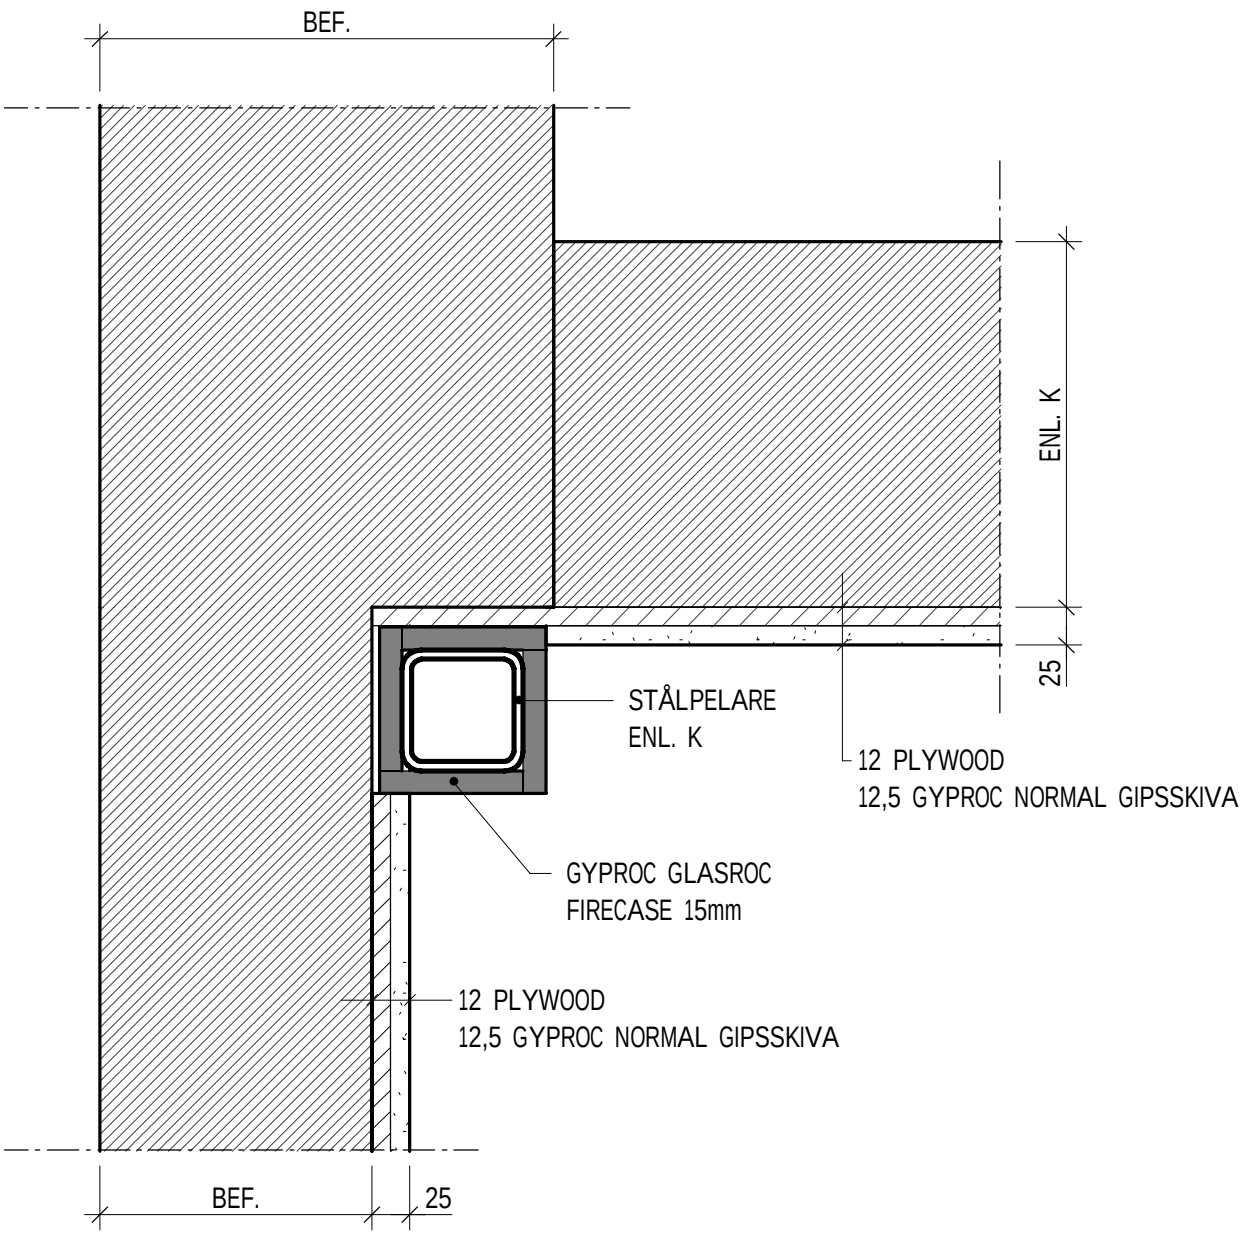

IK10 - STÅLPELARE VID BEF. VÄGGHÖRN
1 : 5

SKALA 1:5 0 100 500 MILLIMETER

SEKTION

ORIENTERINGSSKISS

STATUS

BYGGHANDLING

DATUM

2025-01-31

FÖRBERED AV

T. BERGSTRÖM

ANSVARIG PM

KFU01

BYGGHANDLING

ROBERTSFORS KOMMUN

PROJEKTNAMN

CENTRALEKÖK

PROJEKTNUMMER

YTTRE RINGVÄGEN 4

DIARIENUMMER

FORDONET 1

DISCIPLIN

NORCONSULT SVERIGE AB

UPPRÄGGSNUMMER

108 83 71

TELEFON

010 141 80 00

BYGGHANDLING

FLUGSKOLEN (2008)

VÄRNINGSPÅN

VÄRNINGSDIREKT

DELOMRÅDE

SYSTEM

43 INRE RUMSBILDANDE BYGGDELAR

SPECIFIKATION

INVÄNDIGA DETALJER

DETAILJ

1:5

A1

DOCUMENTNUMMER

A-43-6-001