




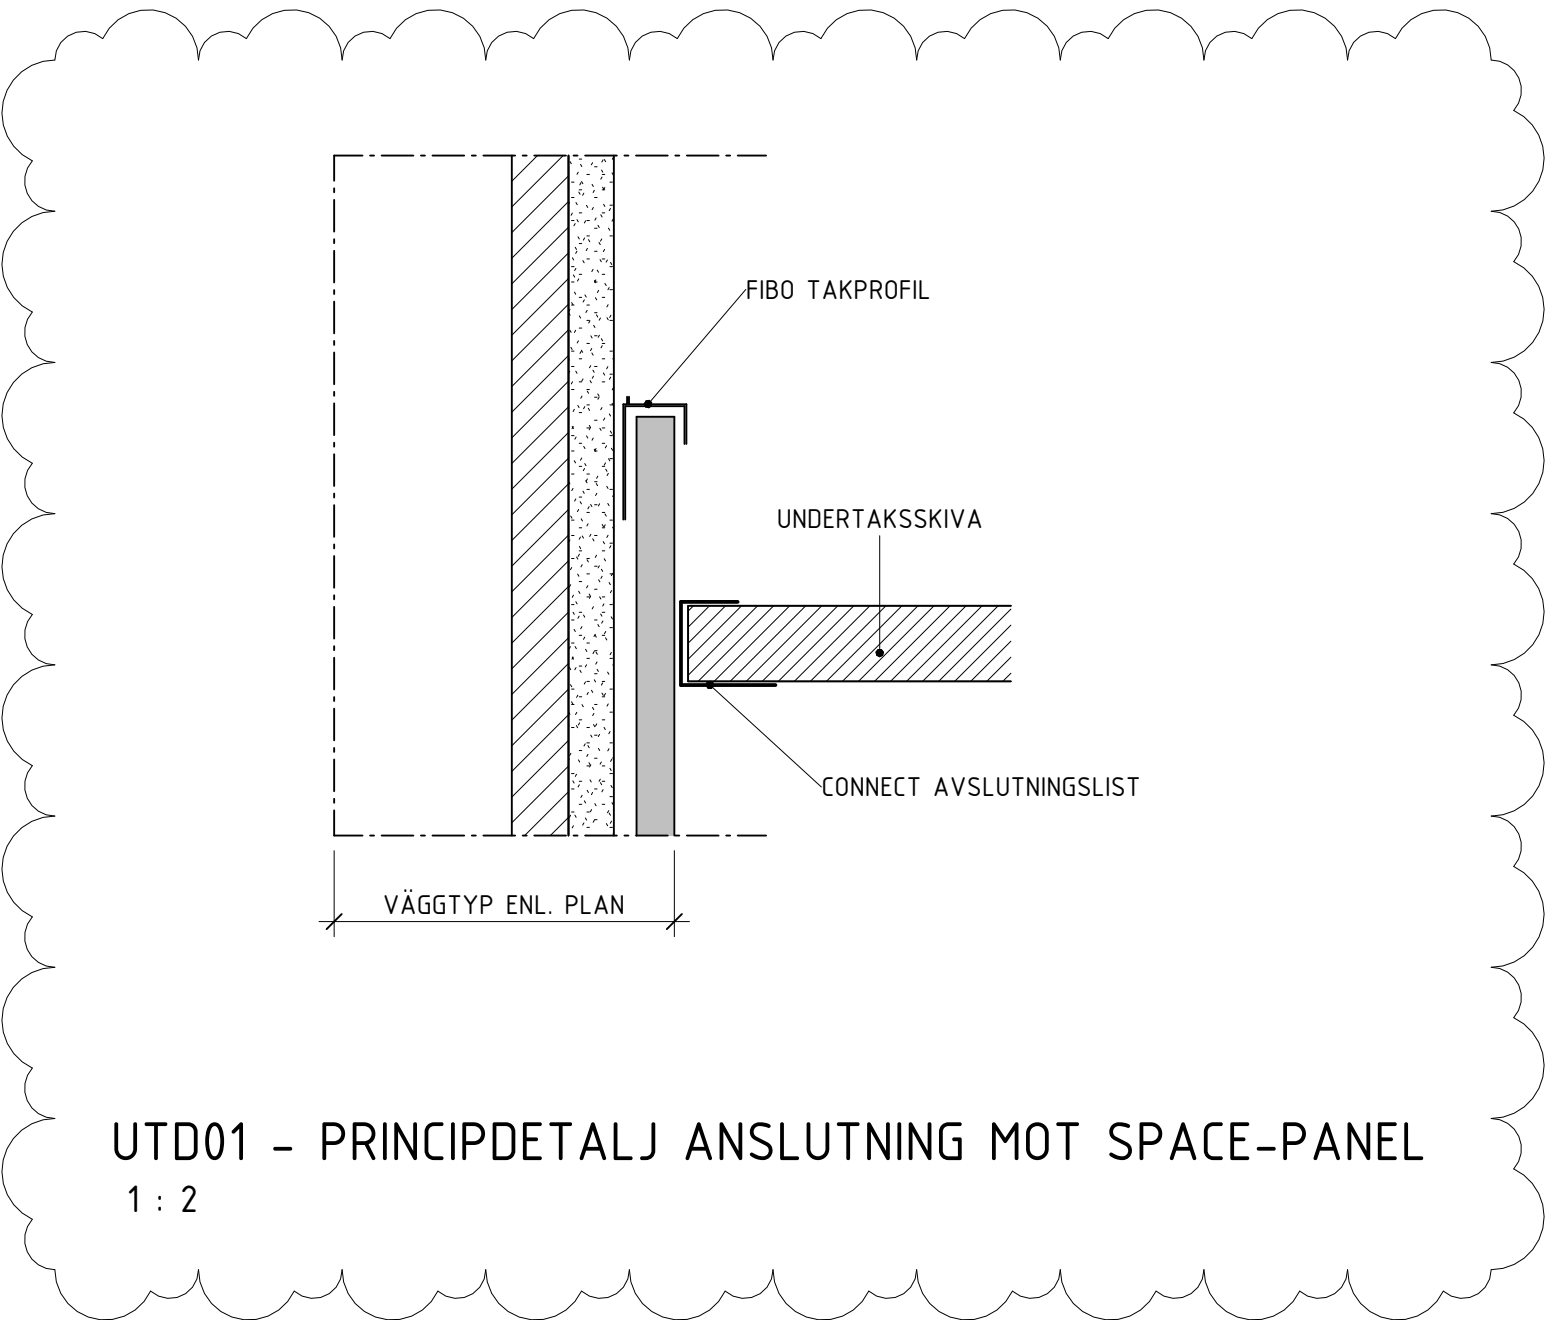


UTD01 - PRINCIPDETALJ ANSLUTNING MOT SPACE-PANEL
1 : 2

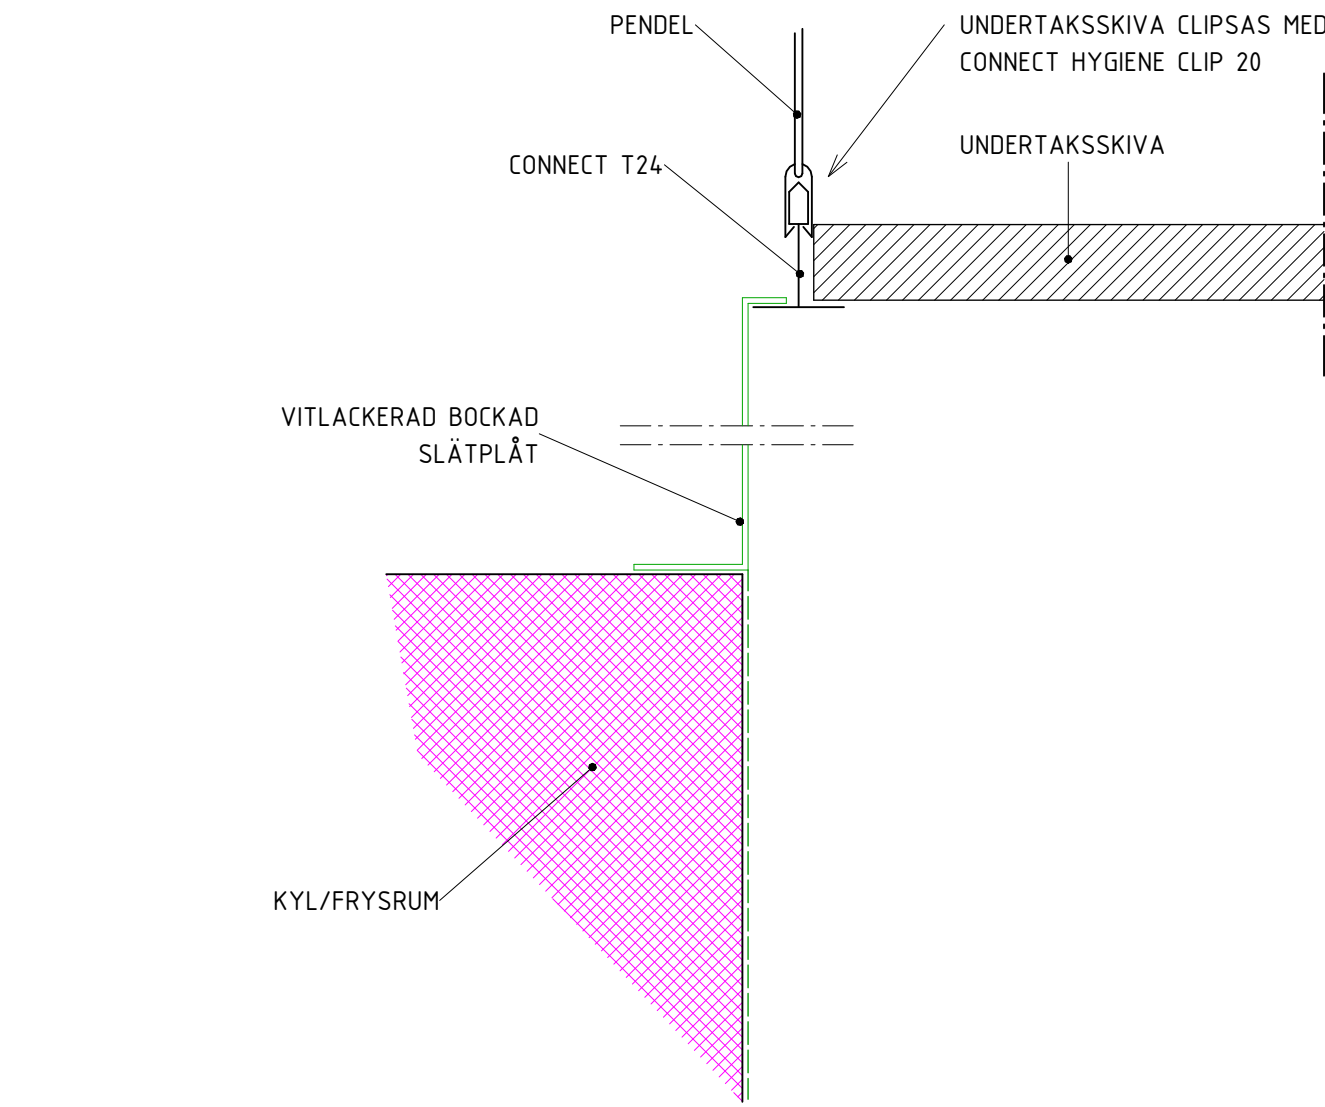


UTD02 - PRINCIPDETALJ ANSLUTNING MOT KYL-/FRYSRUM
1 : 2

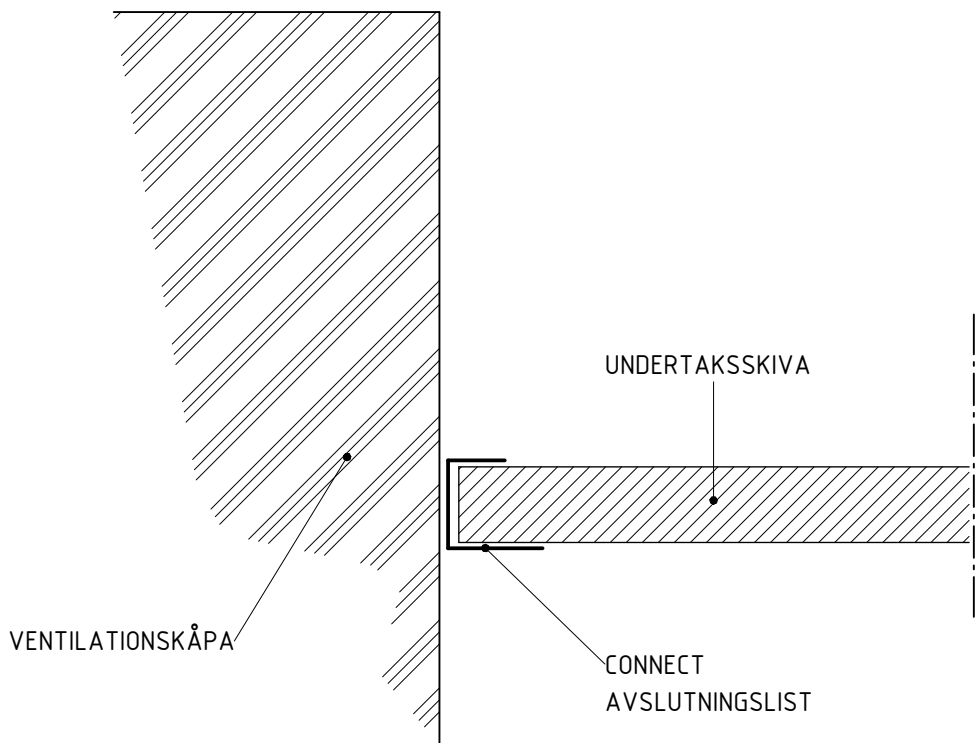


UTD03 - PRINCIPDETALJ ANSLUTNING MOT VENTKÅPA
1 : 2

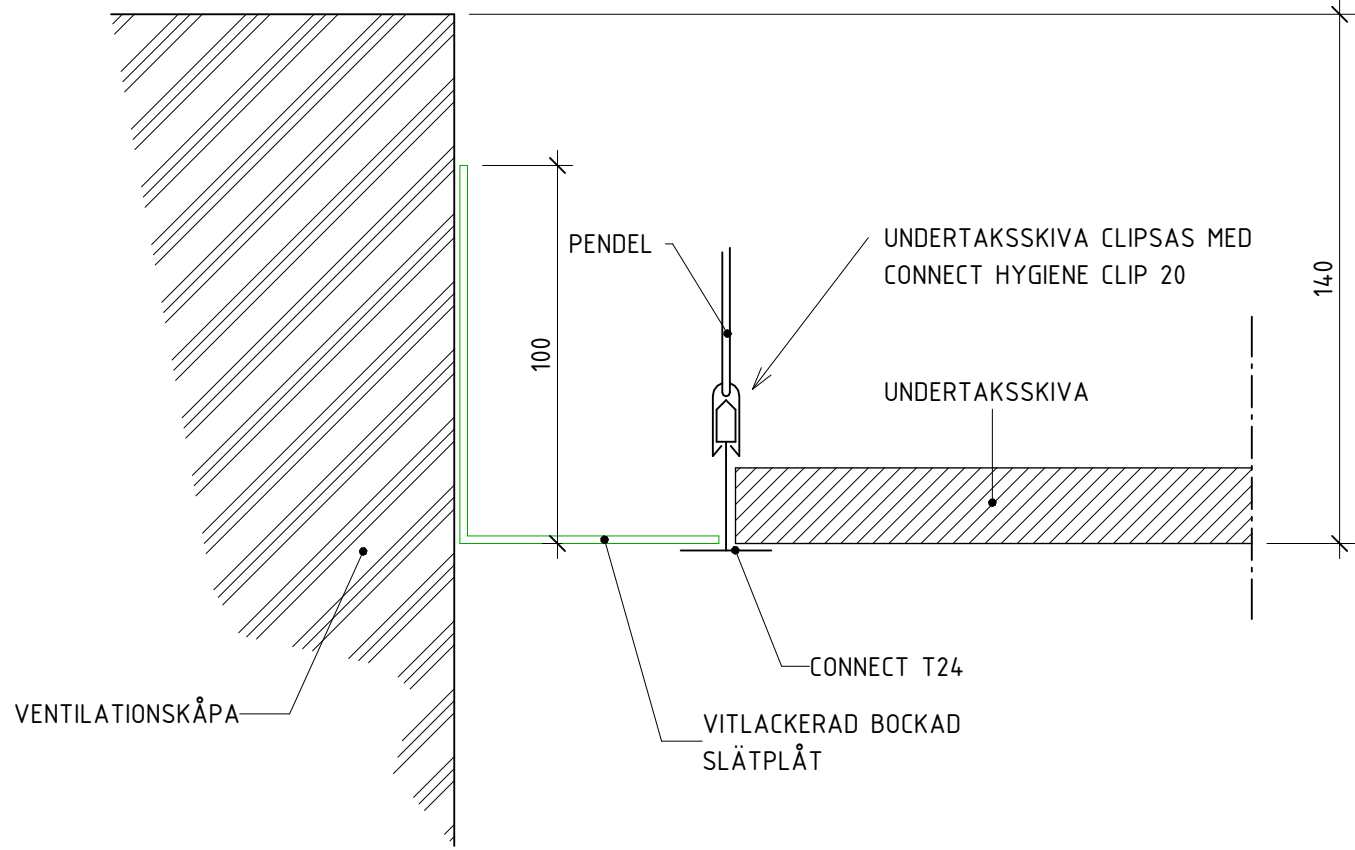

UTD04 - ANSLUTNING MOT VENTKÅPA
1 : 2

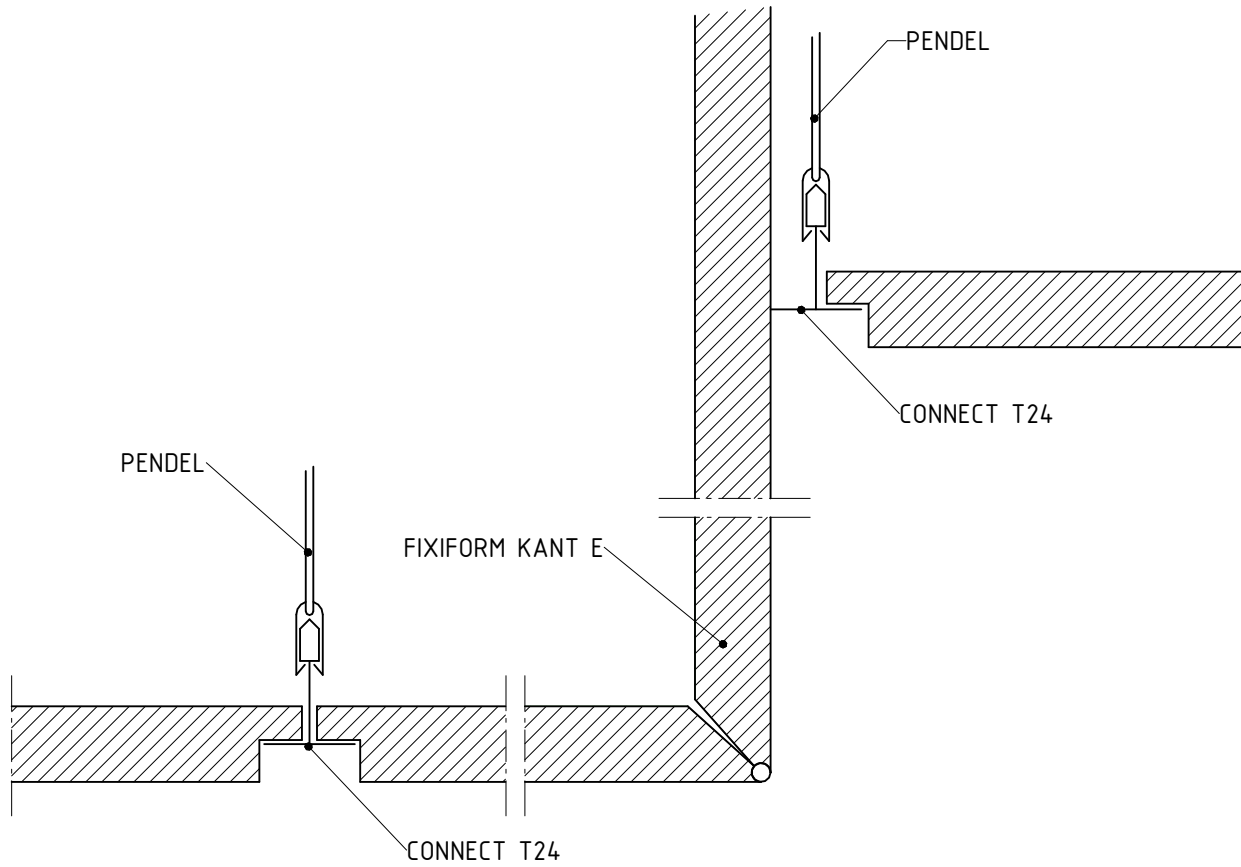

UTD05 - NIVÅSKILLNAD
1 : 2

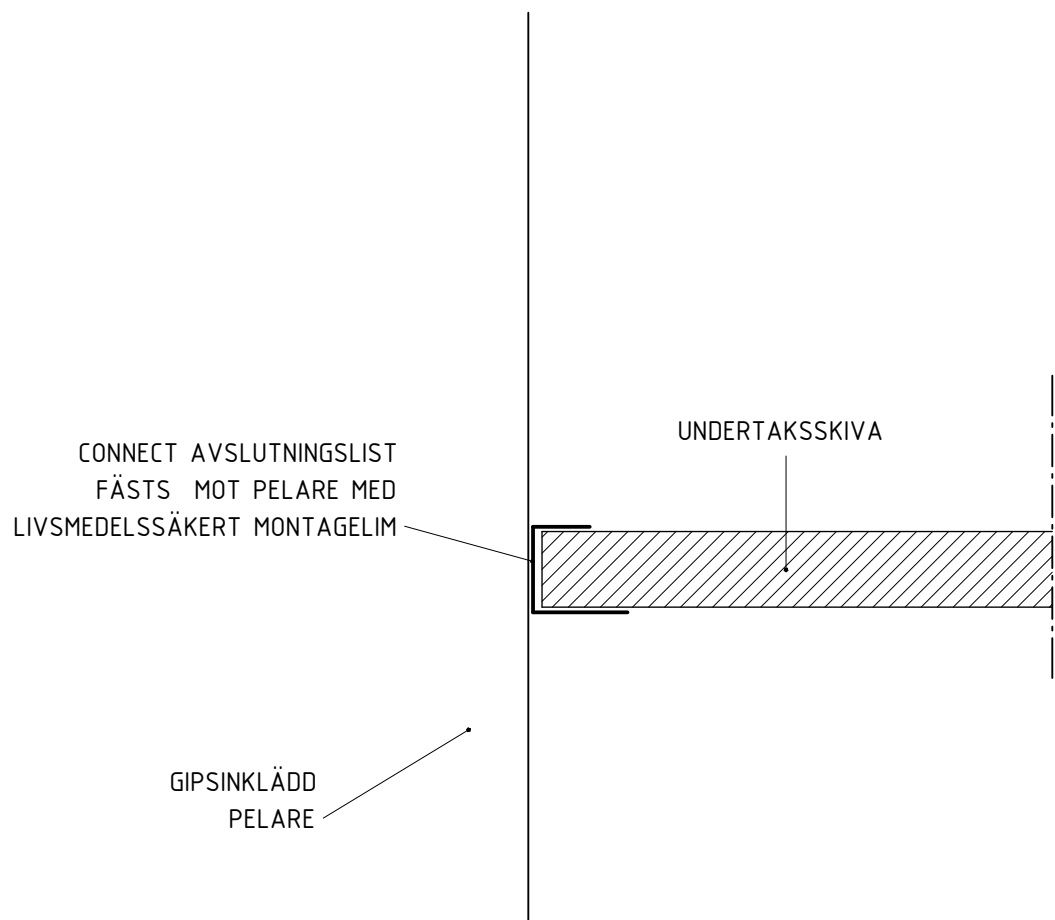

UTD06 - ANSLUTNING MOT PELARE
1 : 2

SEKTION		
ORIENTERINGSSKISS		
STATUS		
FÖRFRÅGNINGSUNDERLAG		
HANDLING		
BYGGHANDLING		
DATUM	ÖSKRÄD AV	ÄNDRINGAR PM
2025-01-31	T. BERGSTRÖM	KFU01
BESTÄLLARE		
ROBERTSFORS KOMMUN		
PROJEKTNAMN		
CENTRALEKÖK		
OMRÅDE		
ROBERTSFORS KOMMUN		
PROJEKTNUMMER	ADRESS	
	YTTRE RINGVÄGEN 4	
DIAGRAMNUMMER	FASTIGHET	
	FORDONET 1	
DISCIPLIN	FÖRETAG	
A	NORCONSULT SVERIGE AB	
UPPDRAGSNUMMER	SKAPAD AV	
108 83 71	MSR	
TELEFON	KONTAKTPERSON	
010 141 80 00	TOMAS BERGSTRÖM	
BYGGNADSTYP	FÄLLEHUS (BY 2008)	
VÄNINGSPLAN	VÄNINGSDEL	DELOMRÅDE
SYSTEM		
43 INRE RUMSBILDANDE BYGGDELAR		
SPECIFIKATION		
UNDERTAKSDetaljer		
DETALJ	SKALA	FORMAT
	1:2	A1
DOCUMENTNUMMER	ÄNDRING	
A-43-6-011	A	