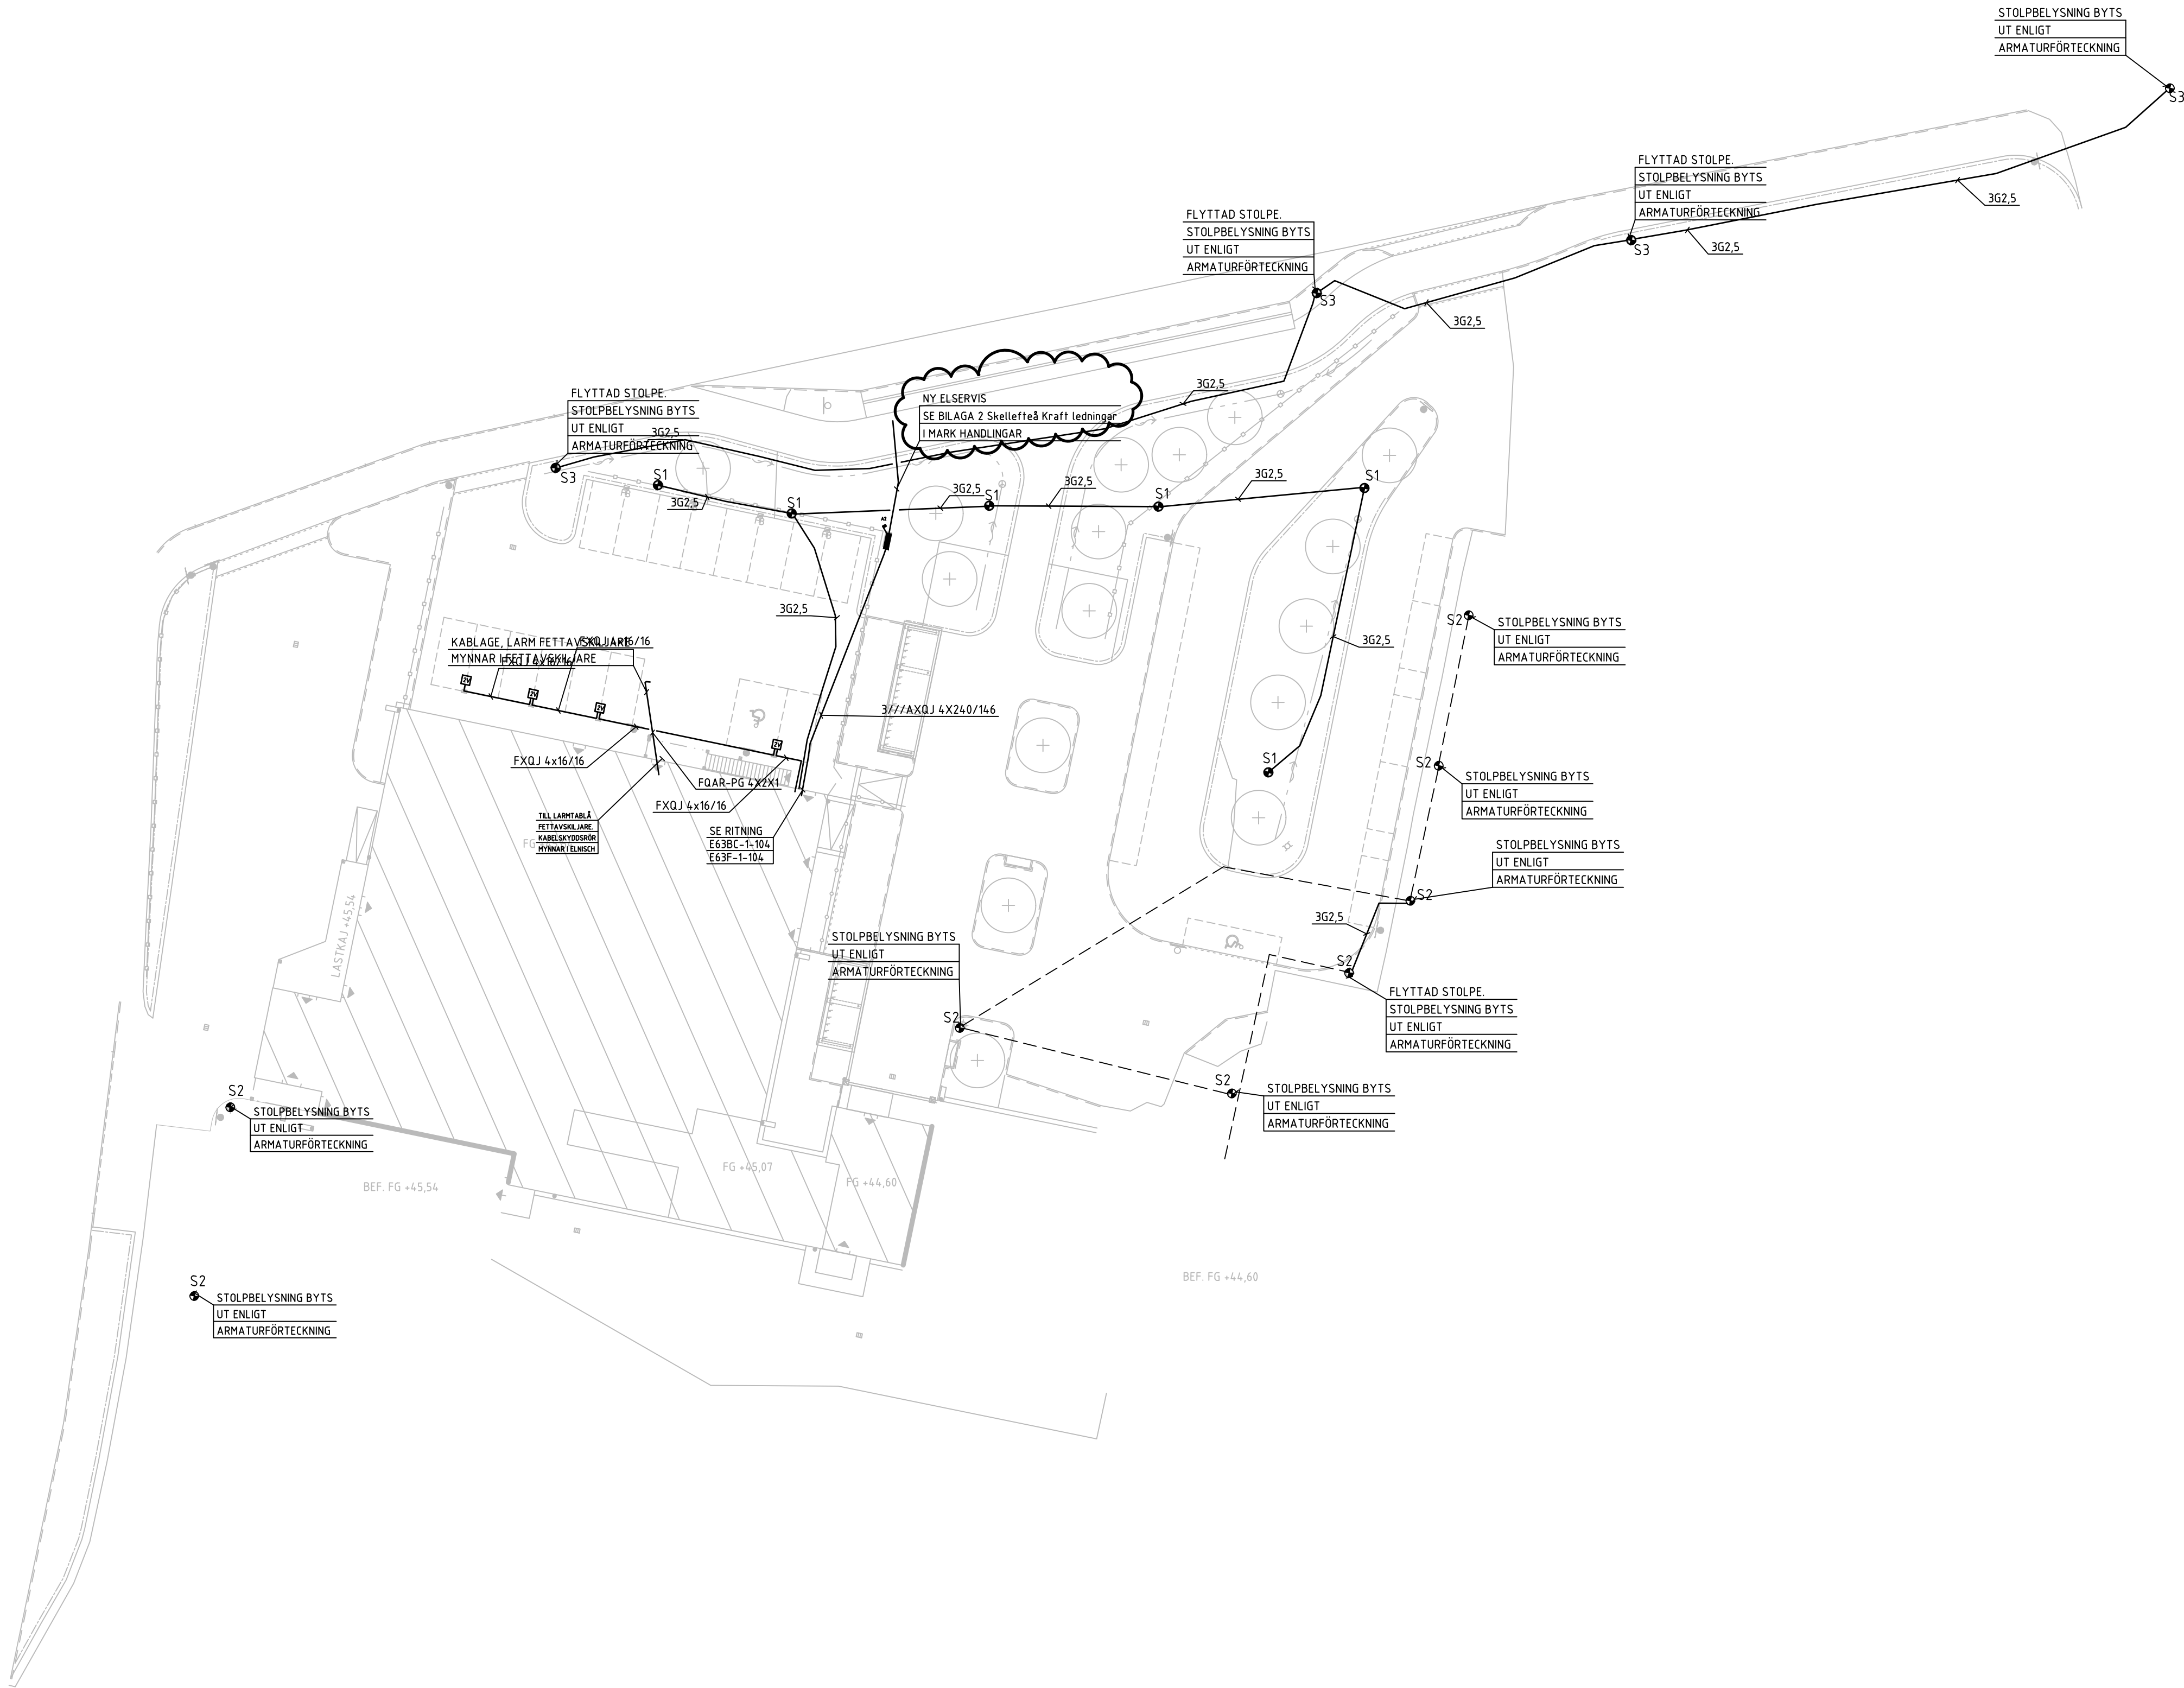


ANVISNINGAR
DÄR INGET ANNAT ANGES GÄLLER:
KABEL FÖRLÄGGS I KABELSKYDDSRÖR
HALOGENFRITT MATERIAL

SYMBOLFÖRKLARINGAR

- MARKMÄTARSKÄP
- DUBBEL MOTORVÄRMARE, TYP ENLIGT
TEKNISK BESKRIVNING
- BELYSNINGSTOLPE TYP
ENLIGT ARMATURFÖRTECKNING
- KABEL

HÄNVISNINGAR

- SE ÄVEN
- TEKNISK BESKRIVNING EL
- ARMATURFÖRTECKNING

STATUS		
FÖRFRÅGNINGSUNDERLAG		
HANDLING		
BYGGHANDLING		
DATUM	2025-01-31	ADRESS
DAGENSNUMMER	GIN	ANDERINGAR PM
BESTÄLLARE		KFU01
 ROBERTSFORS KOMMUN		
PROJEKTNAMN		
CENTRALEKÖK		
OMRÅDE		
ROBERTSFORS KOMMUN		
PROJEKTNUMMER	108 83 71	ADRESS
FASTIGHET	YTTRE RINGVÄGEN 4	
DISCIPLIN	E	FORDONET 1
UPPDRAGSNUMMER	1088371	FORETAG
TELEFON	010 141 80 00	NORCONSULT SVERIGE AB
BYGGNADSVÄRK		KONTAKTPERSON
		TOMAS BERGSTRÖM
		PÅLÖSNING (ROT 2008)
VÄNINGSPLAN	VÄNINGSDEL	DELOMRÅDE
SYSTEM		
KRAFT & BELYSNING		
SITUATIONSPLAN		
PLANER	SKALA	FORMAT
E-63-1-001	1:300	A1
		ÄNDRING
		A